





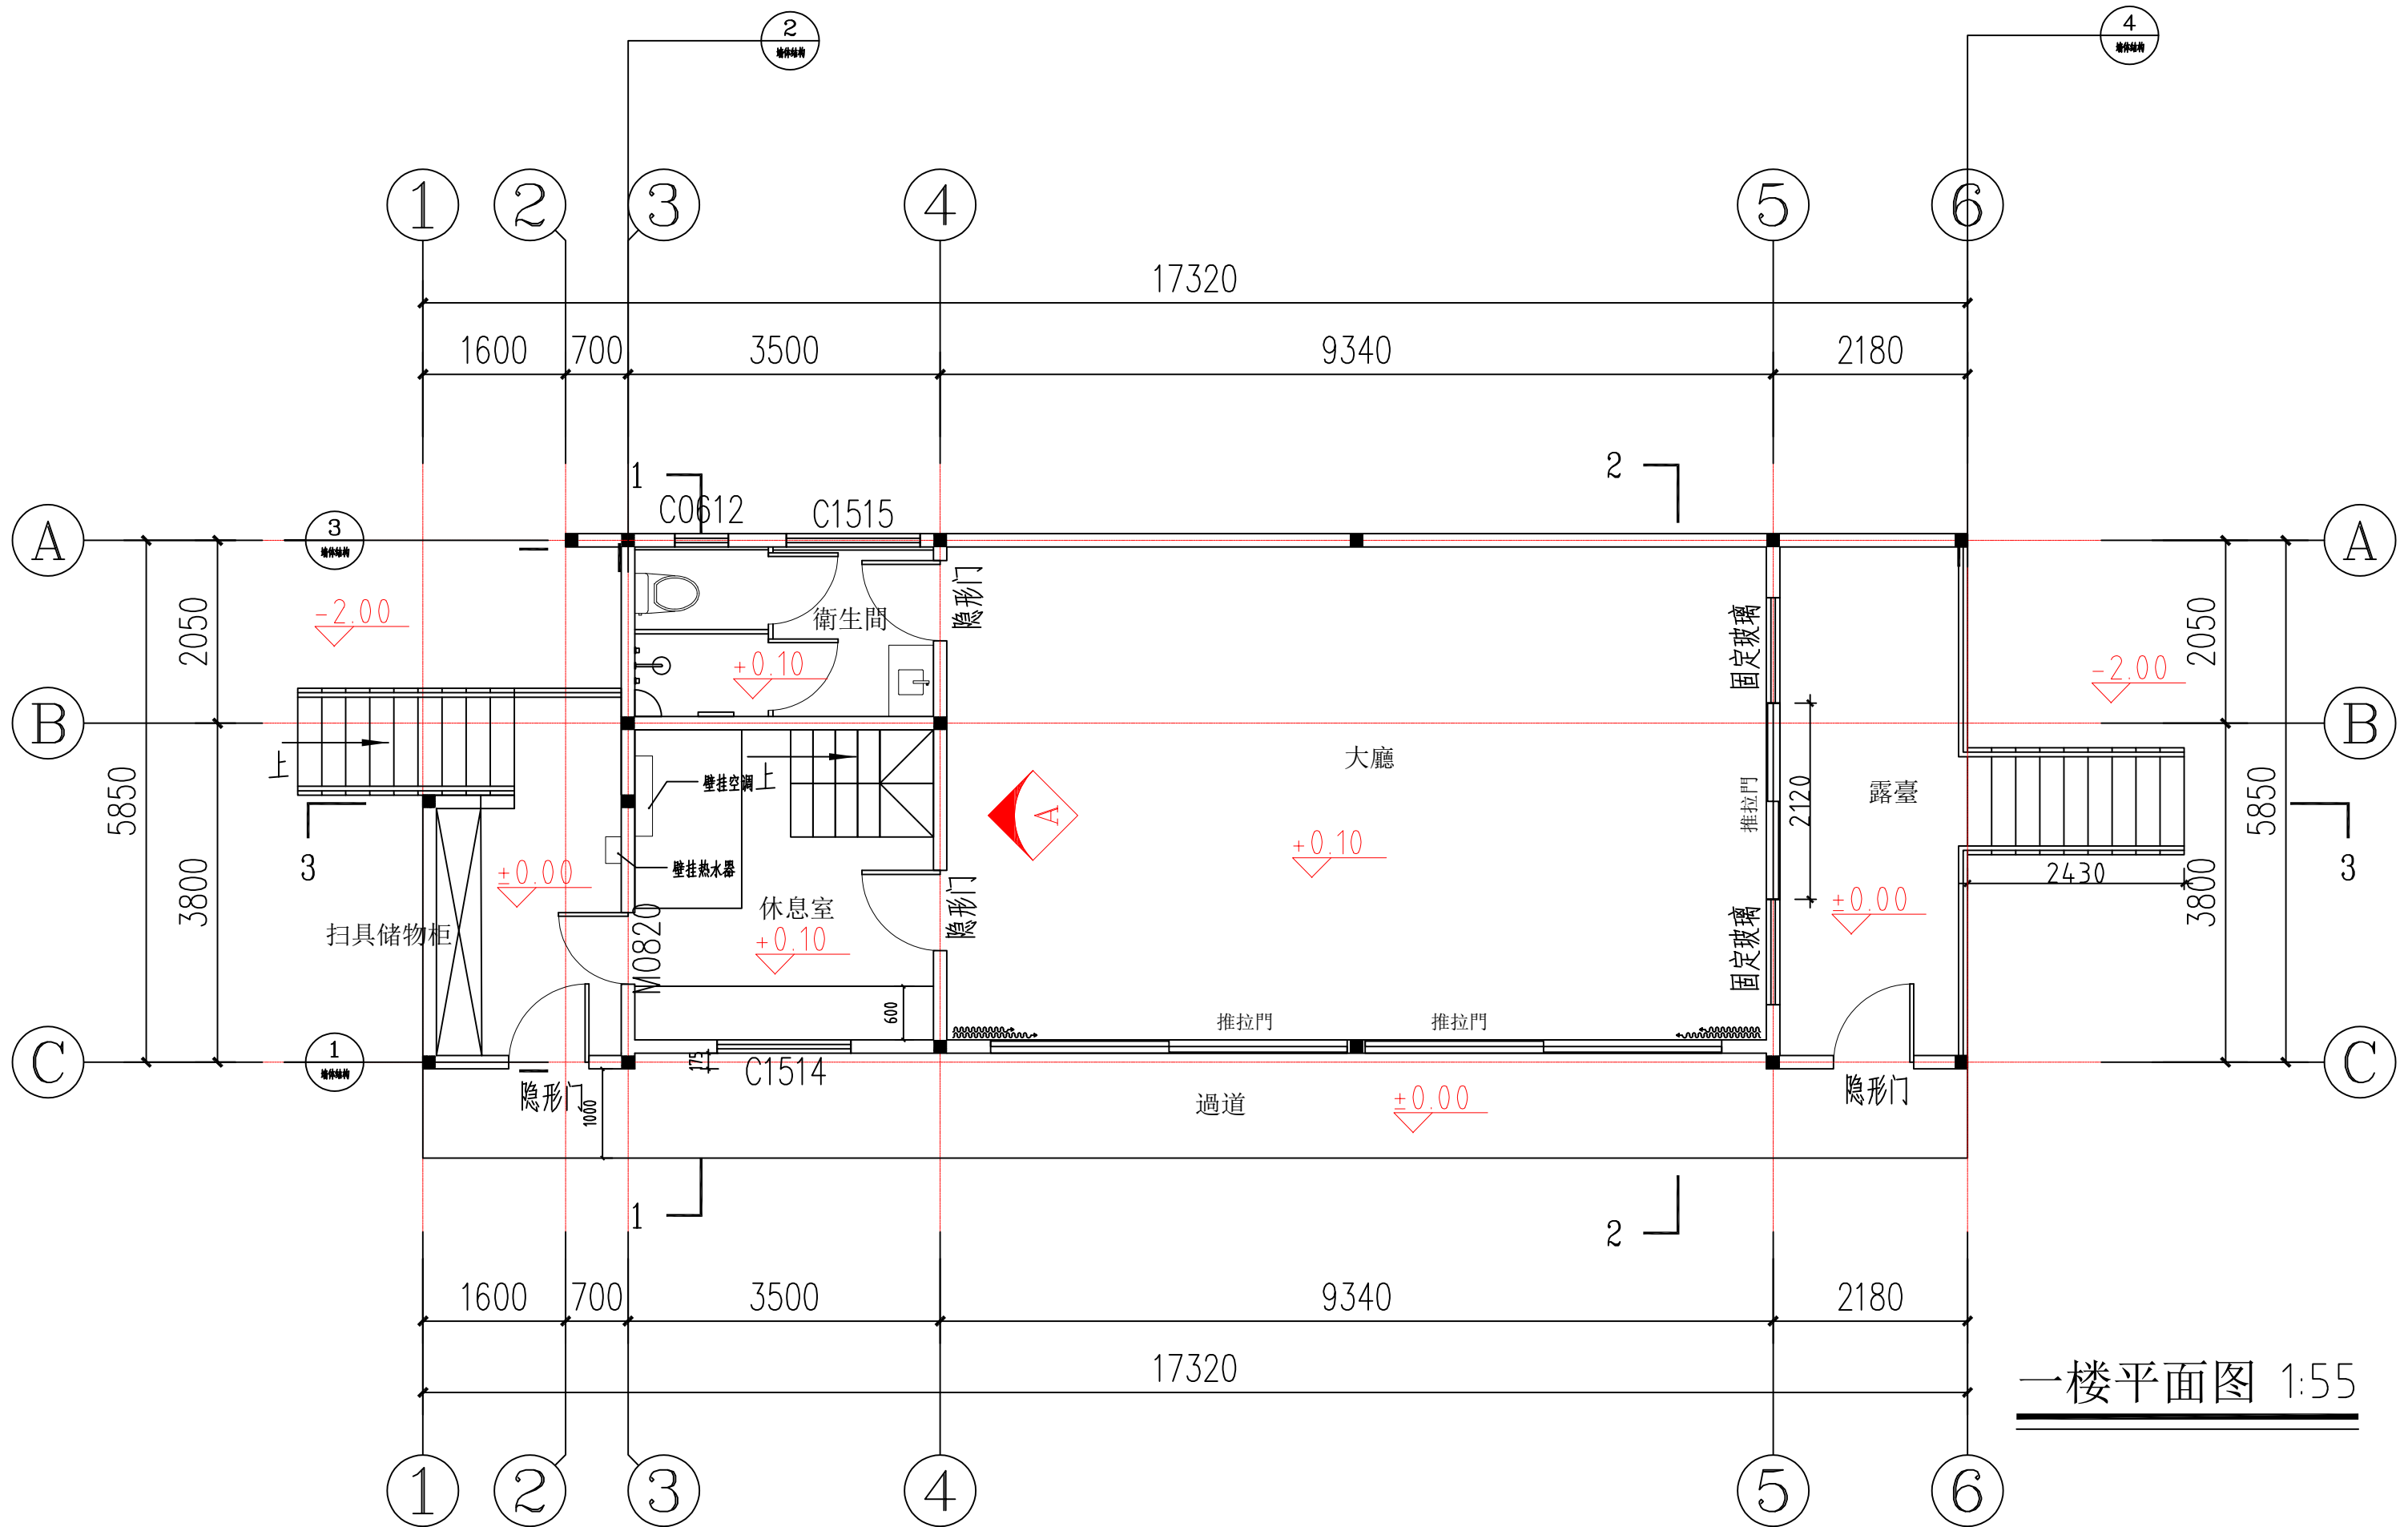


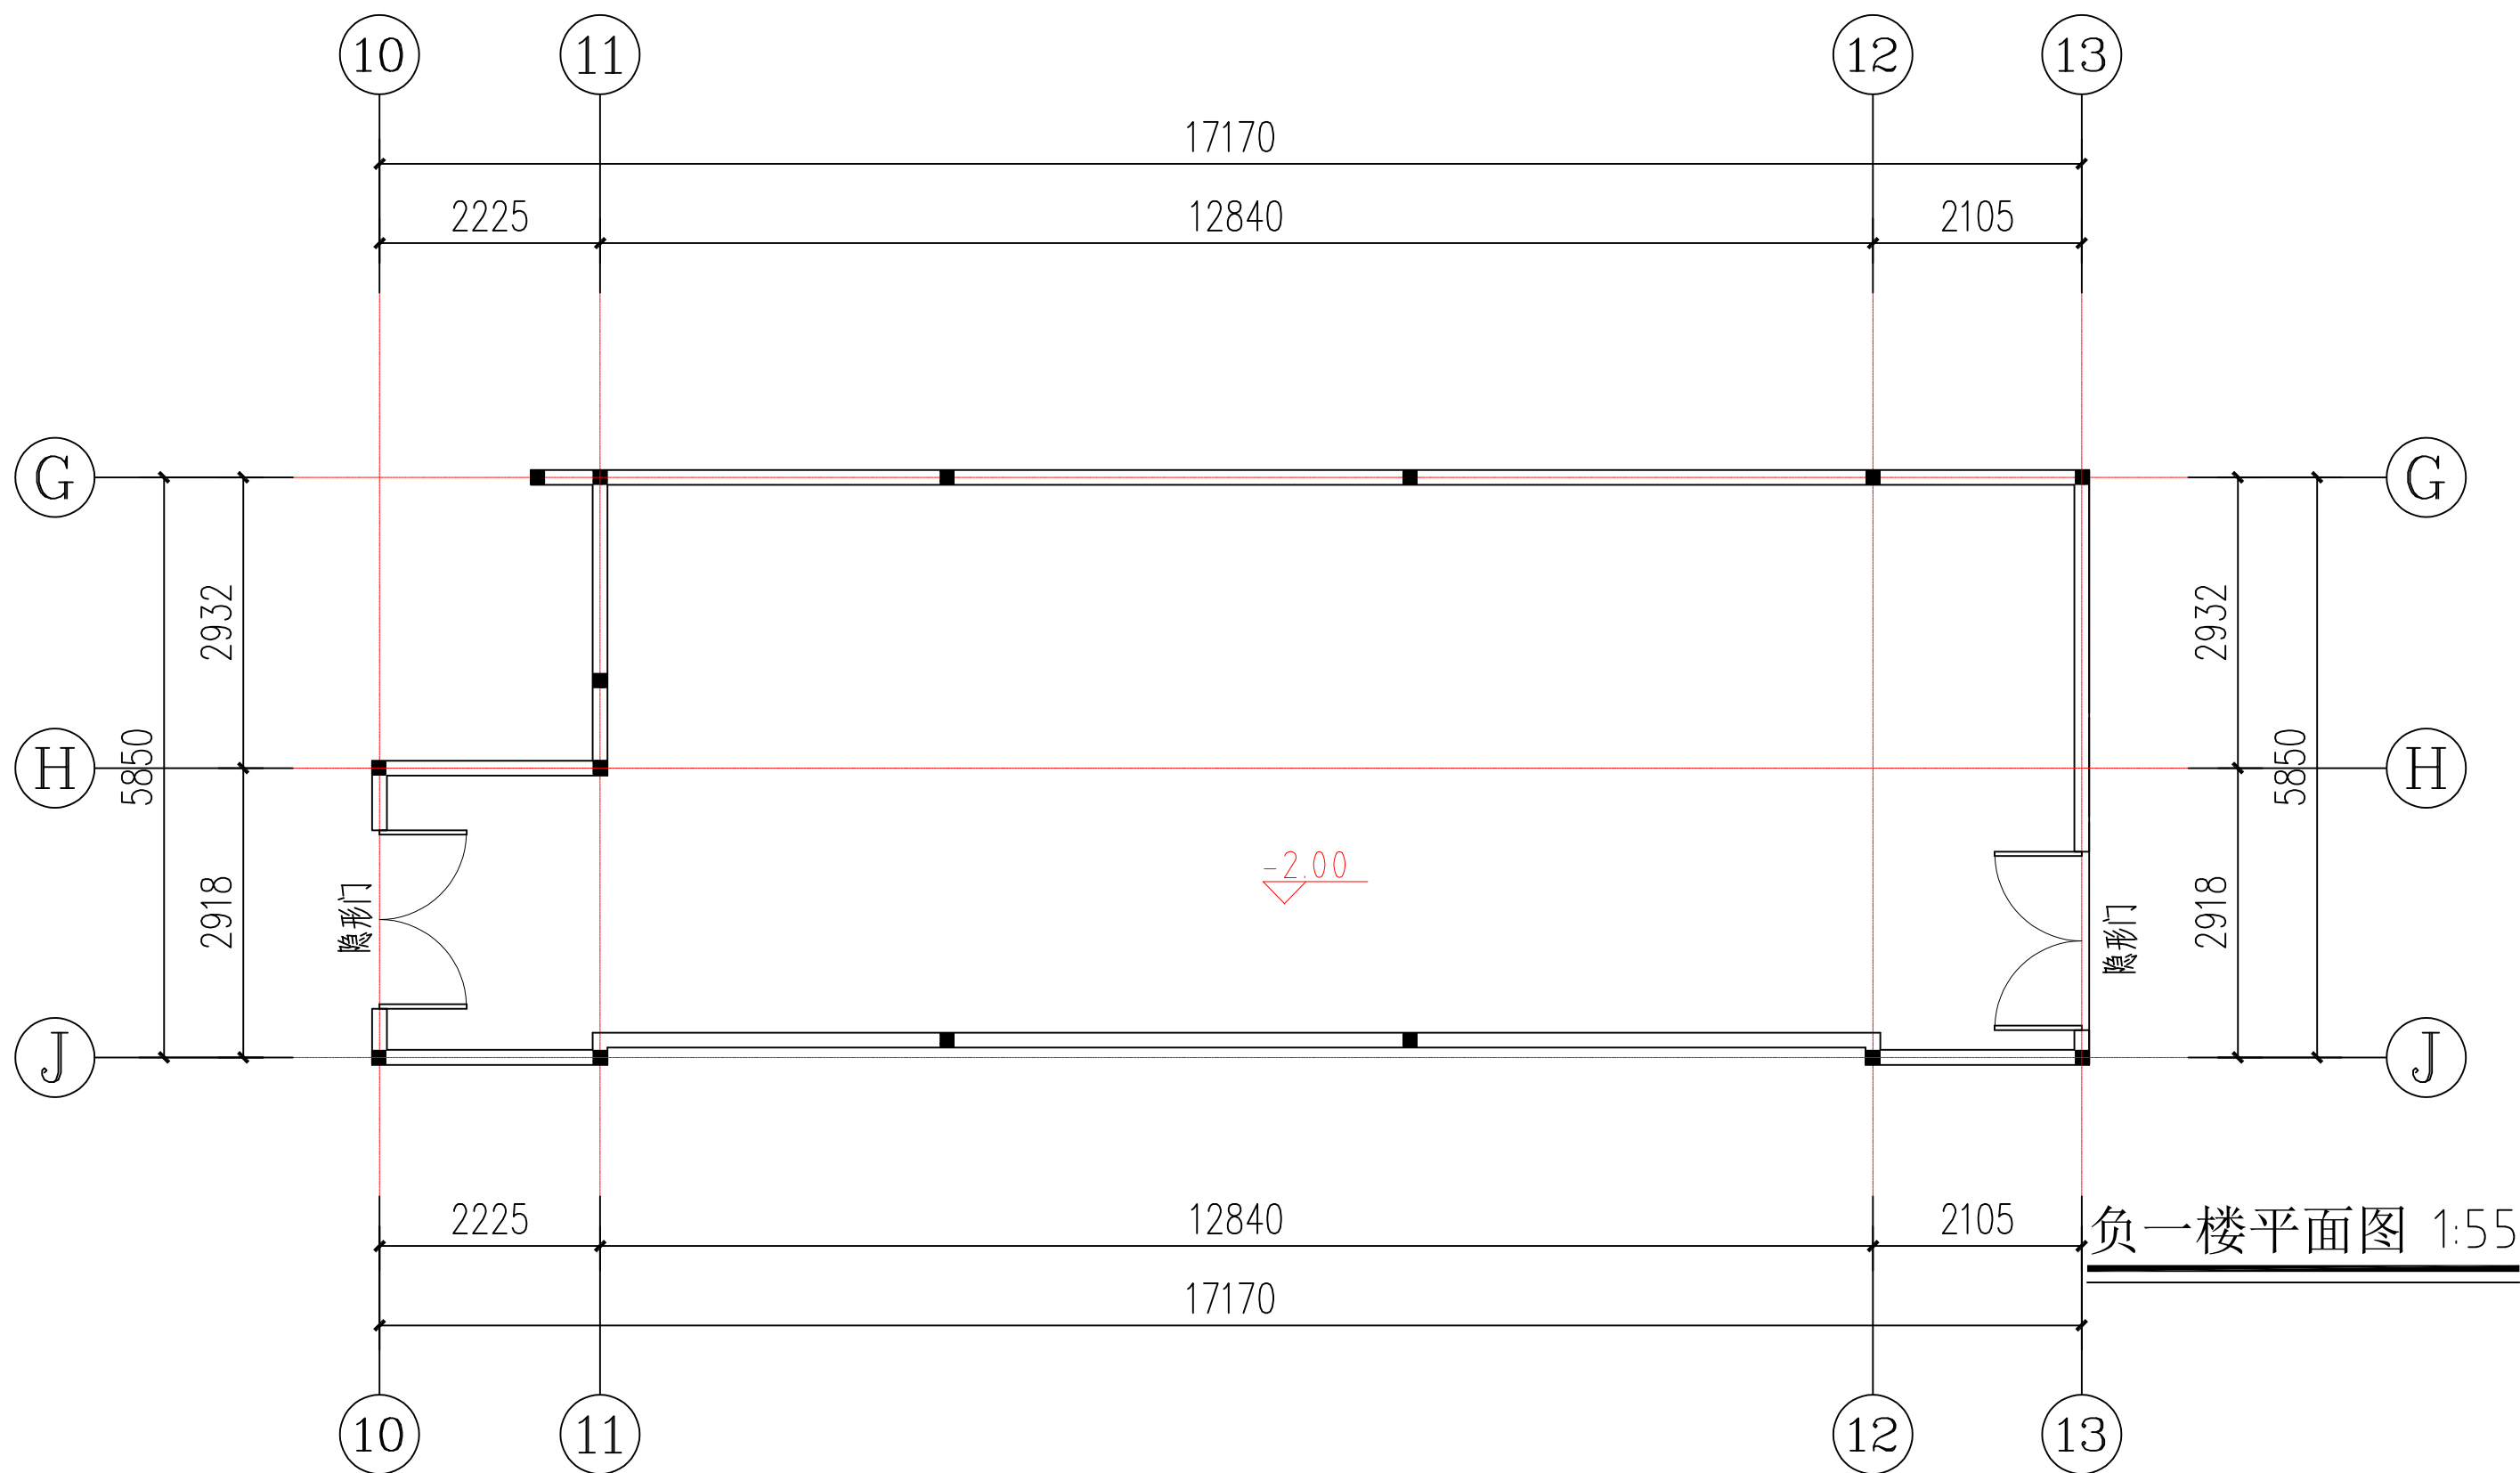

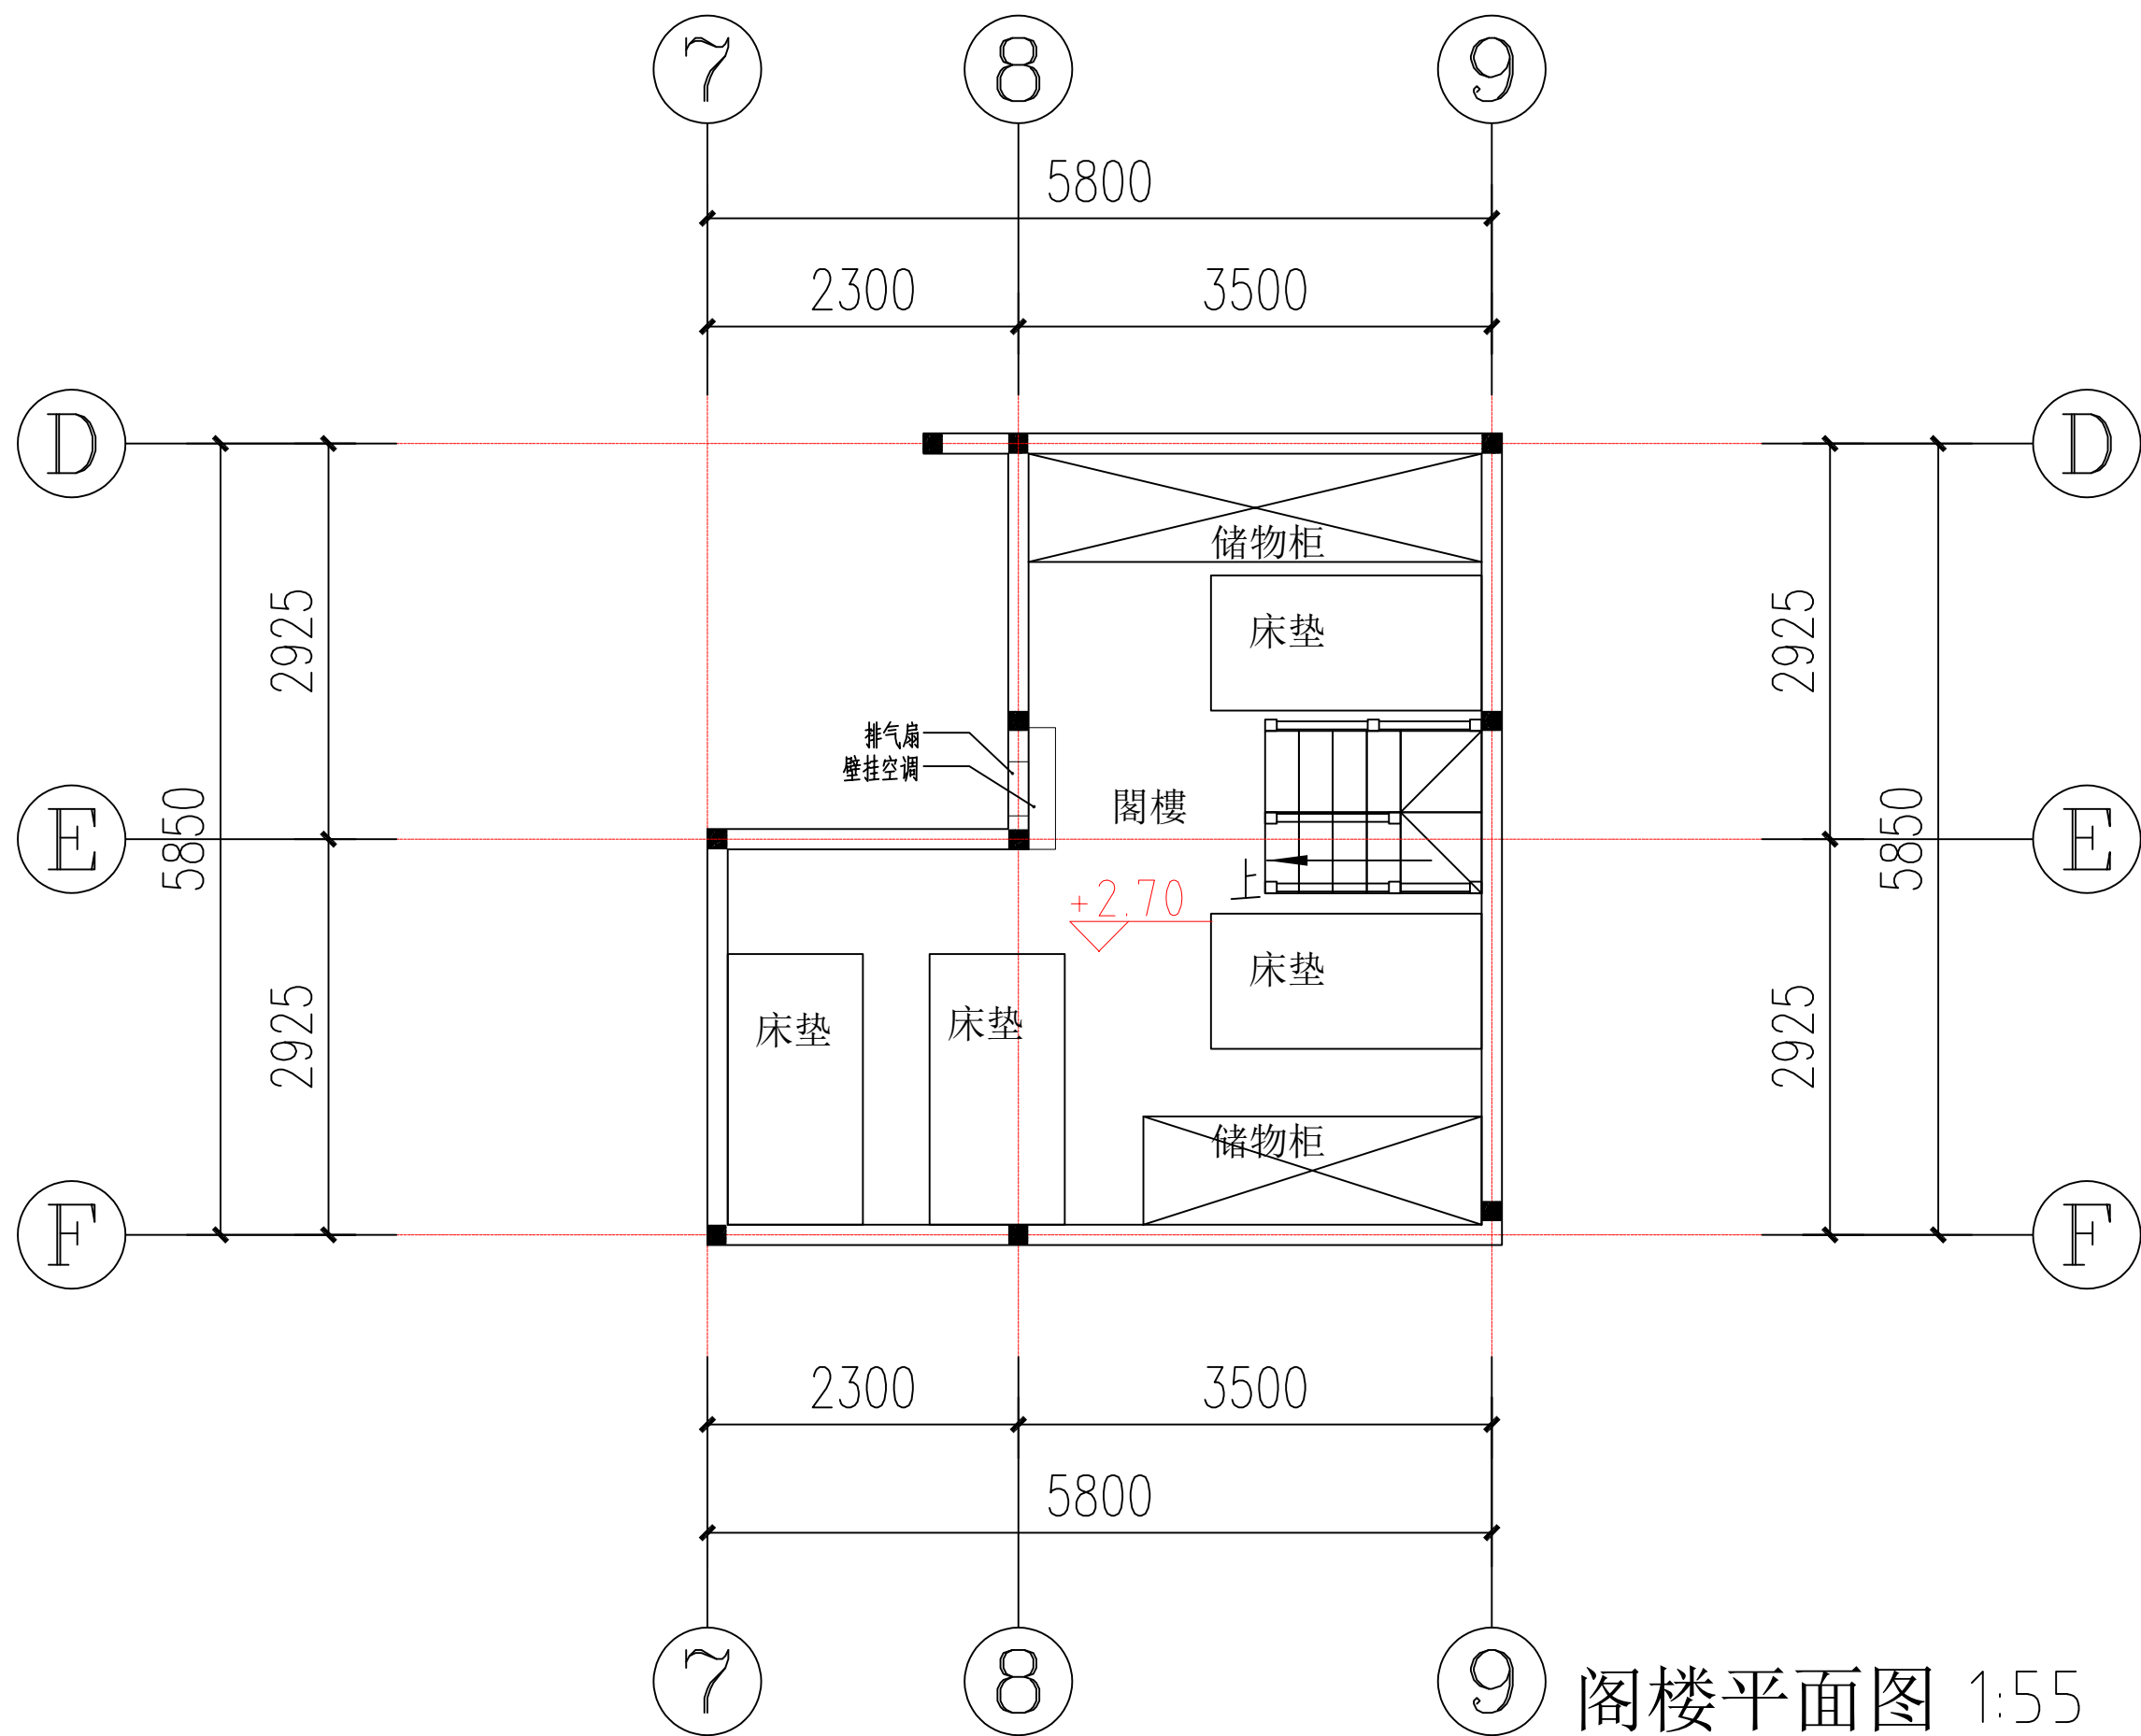


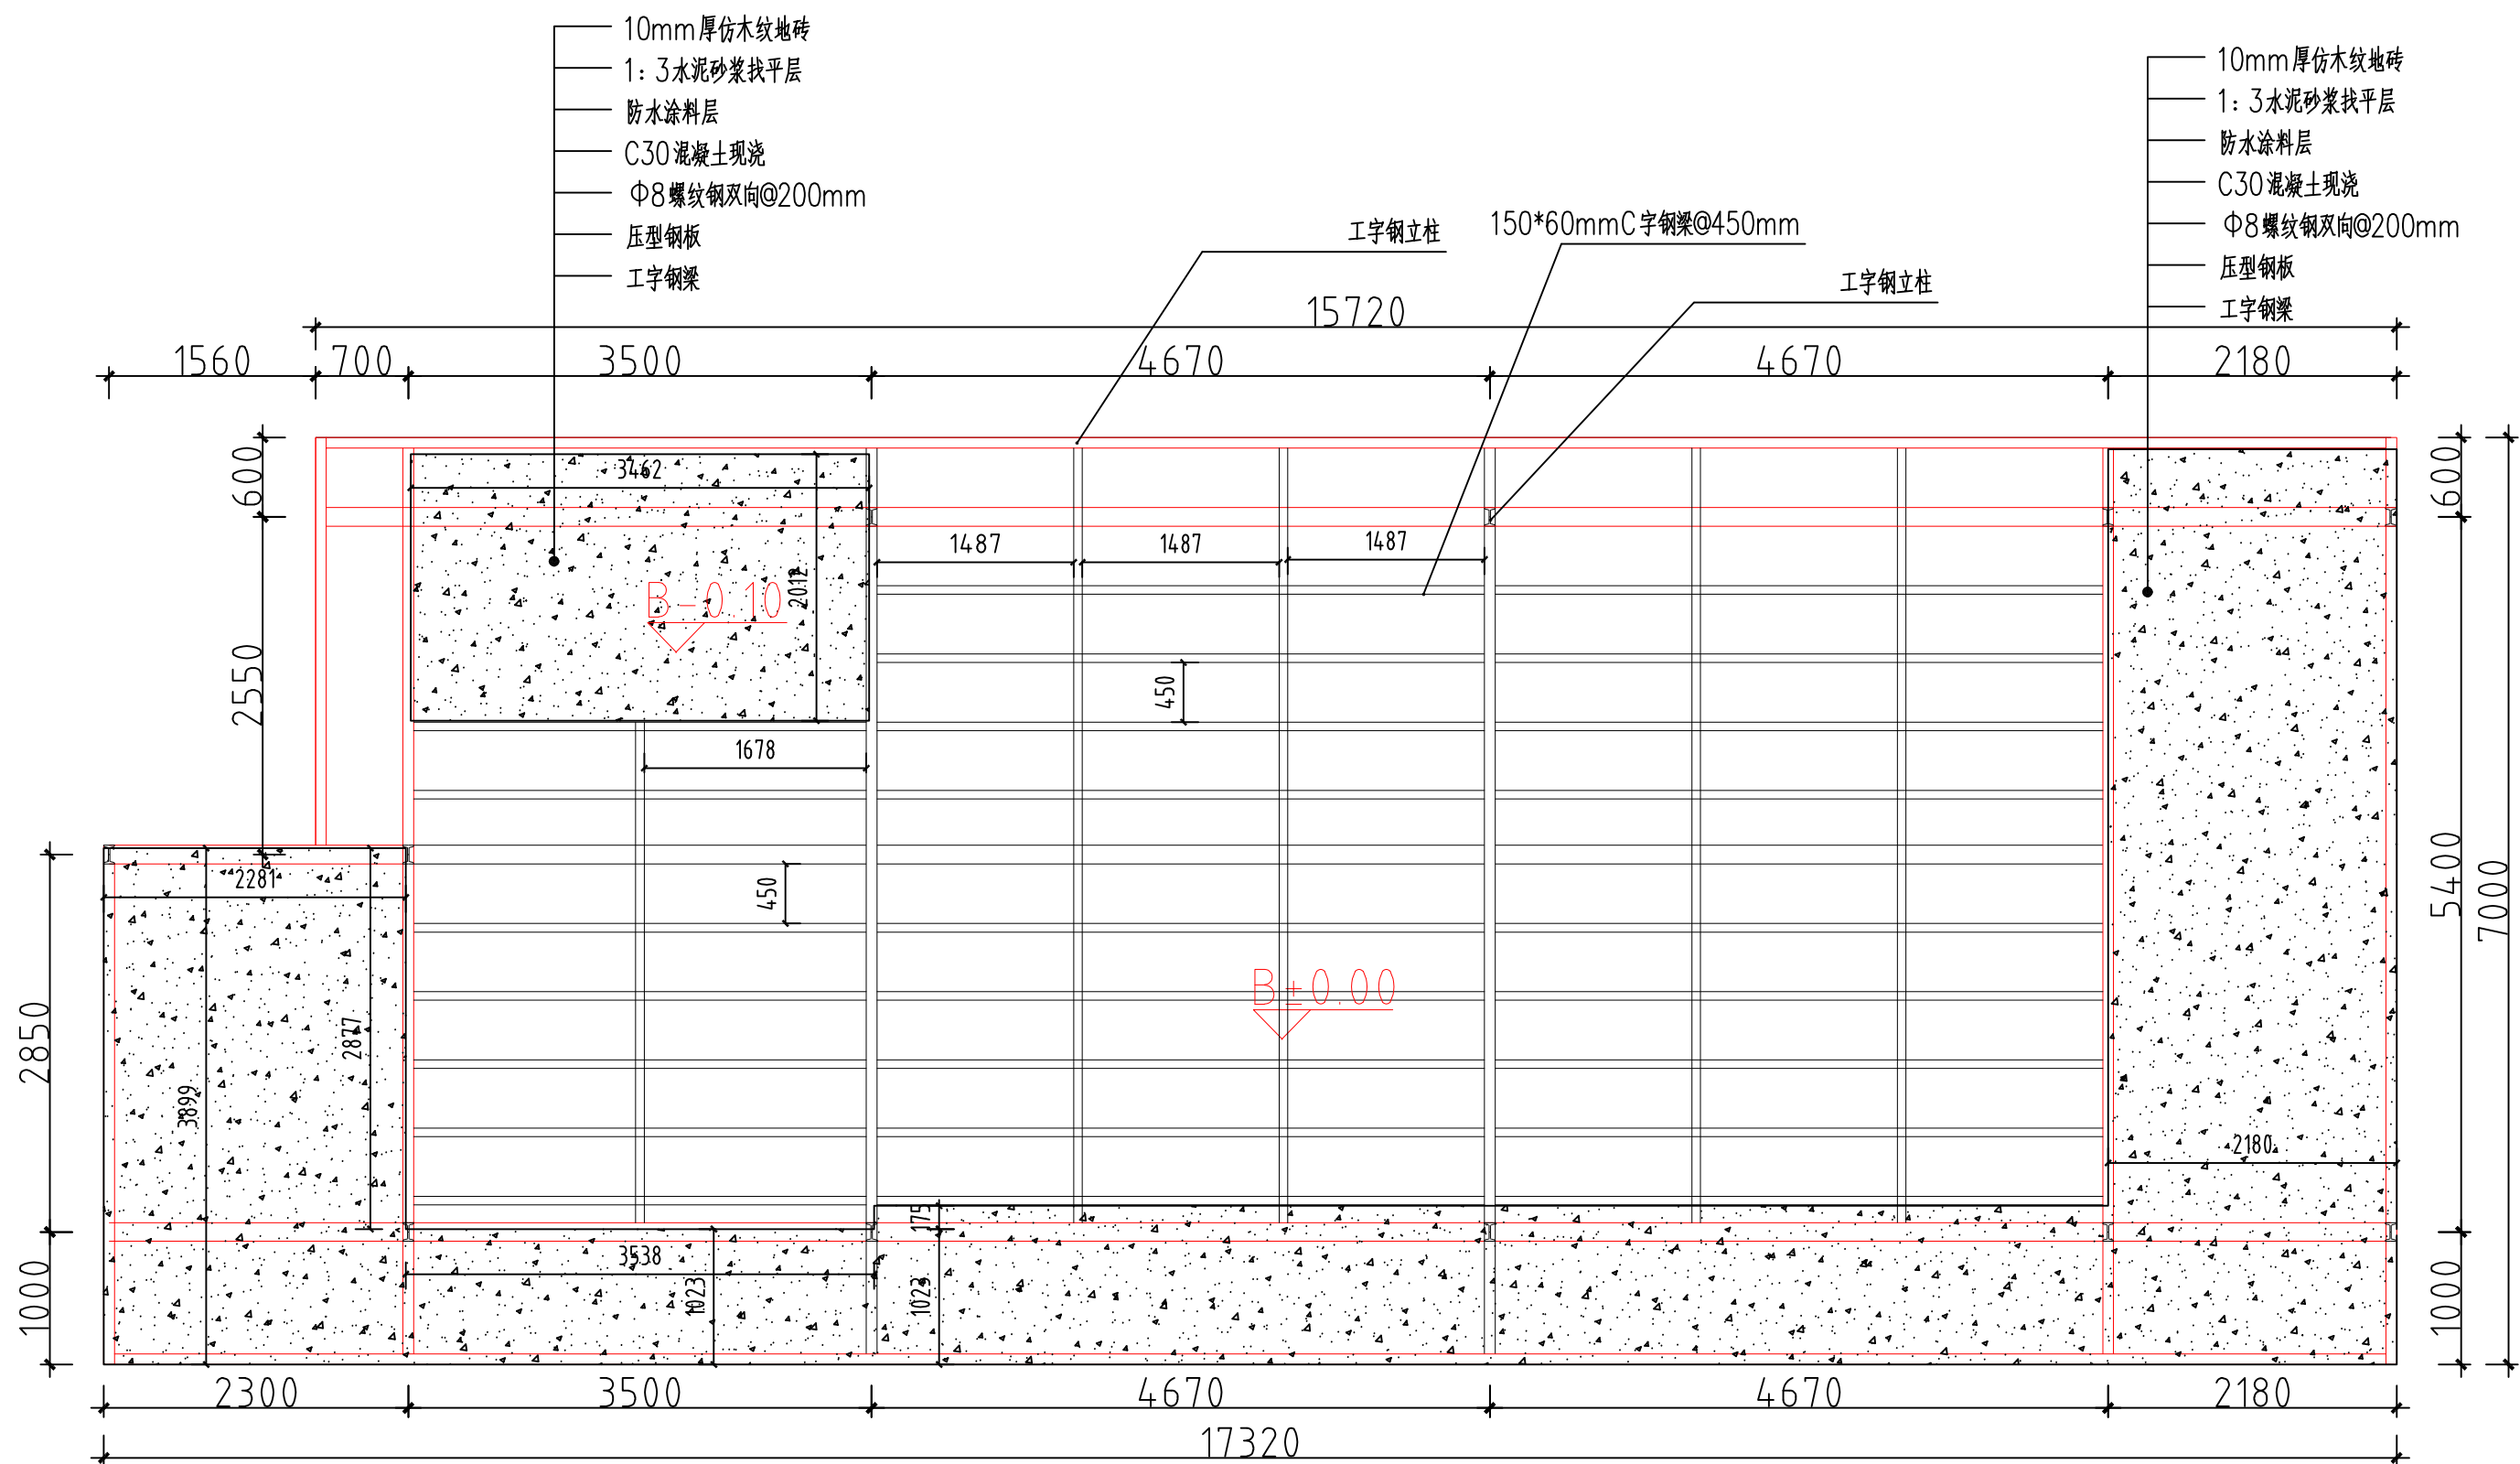


钢结构平面图 1:50

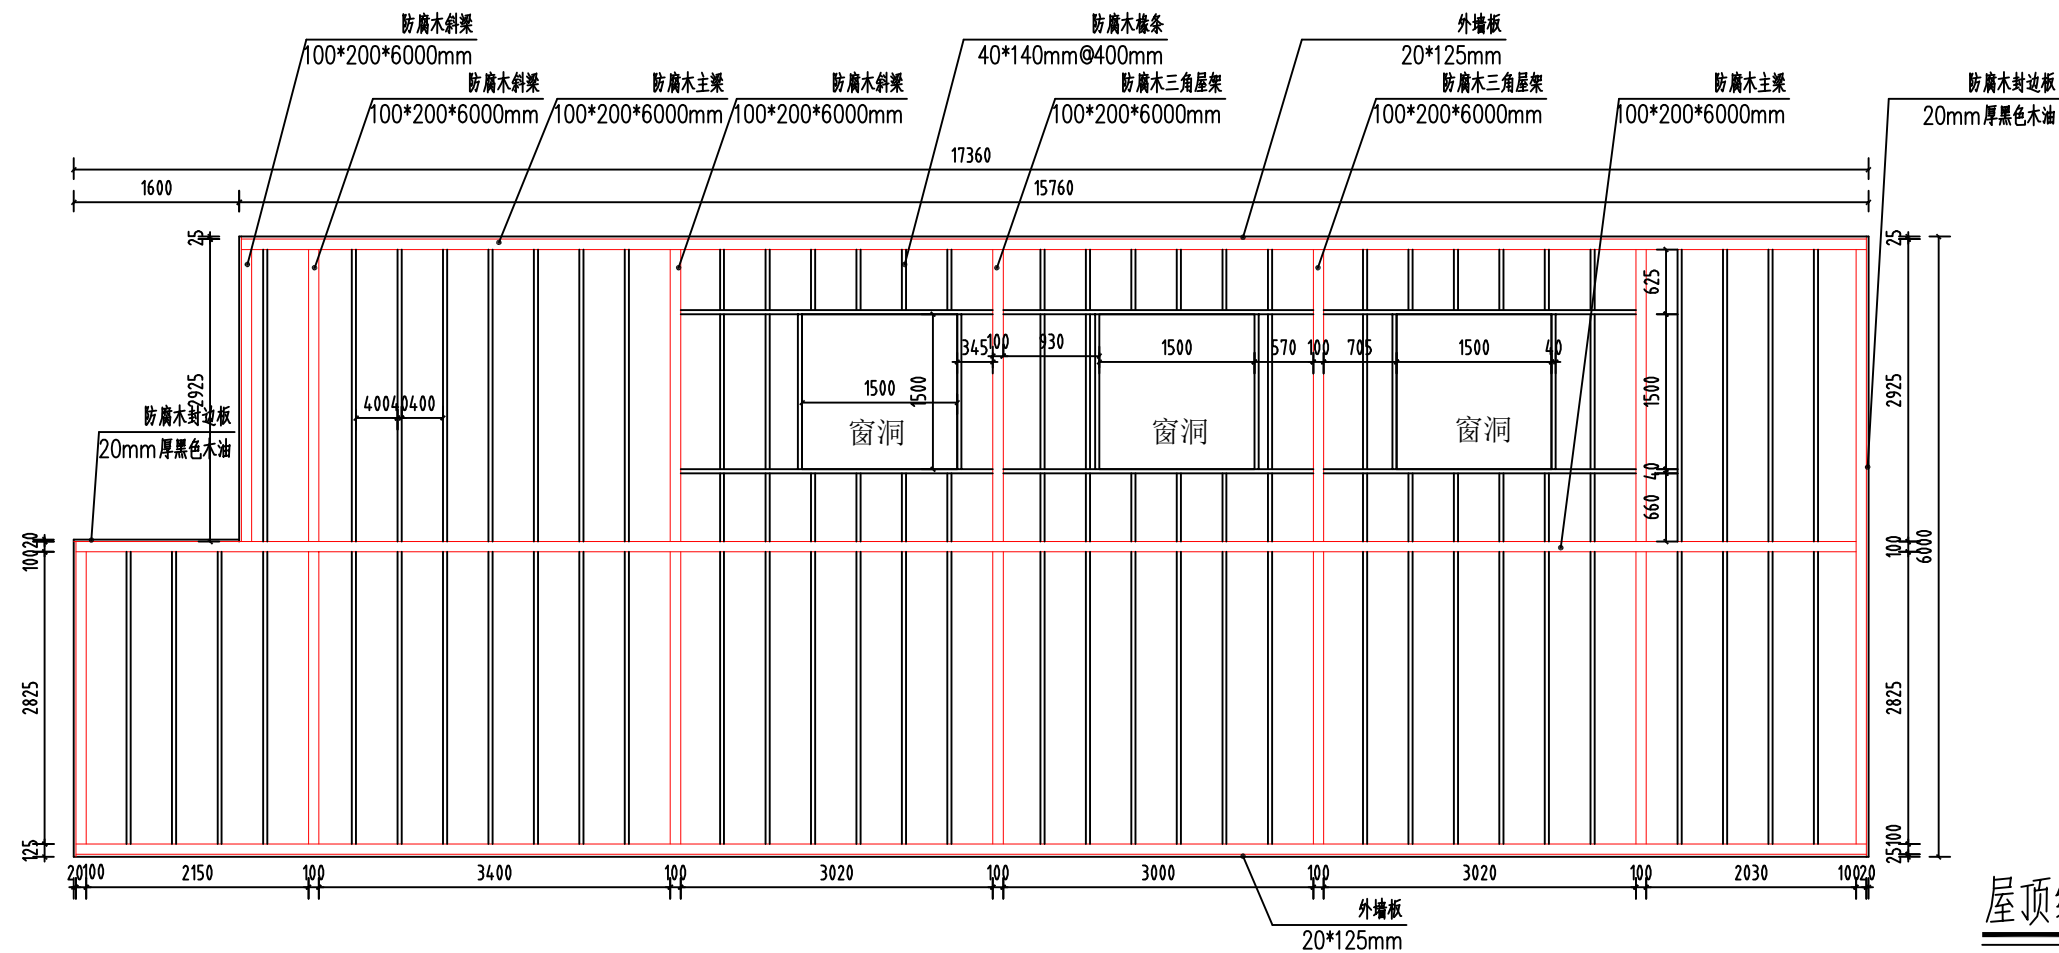


屋顶结构平面图 1: 70

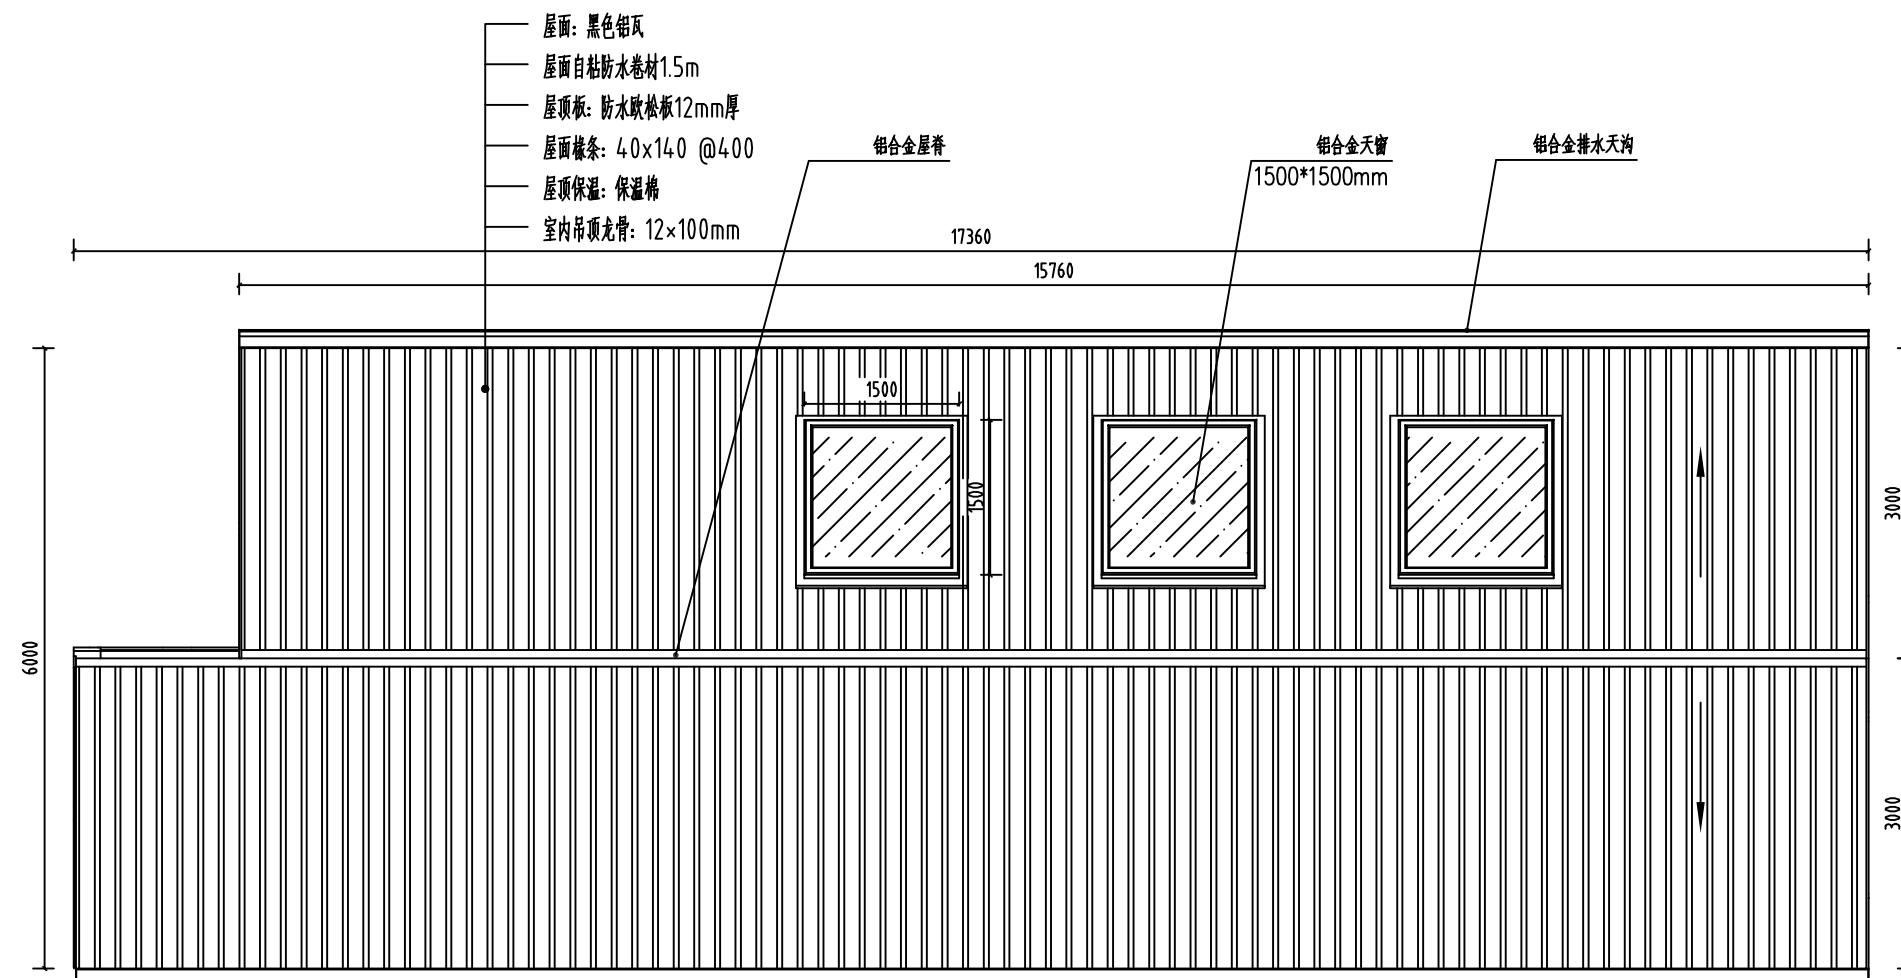


屋顶平面图 1: 70

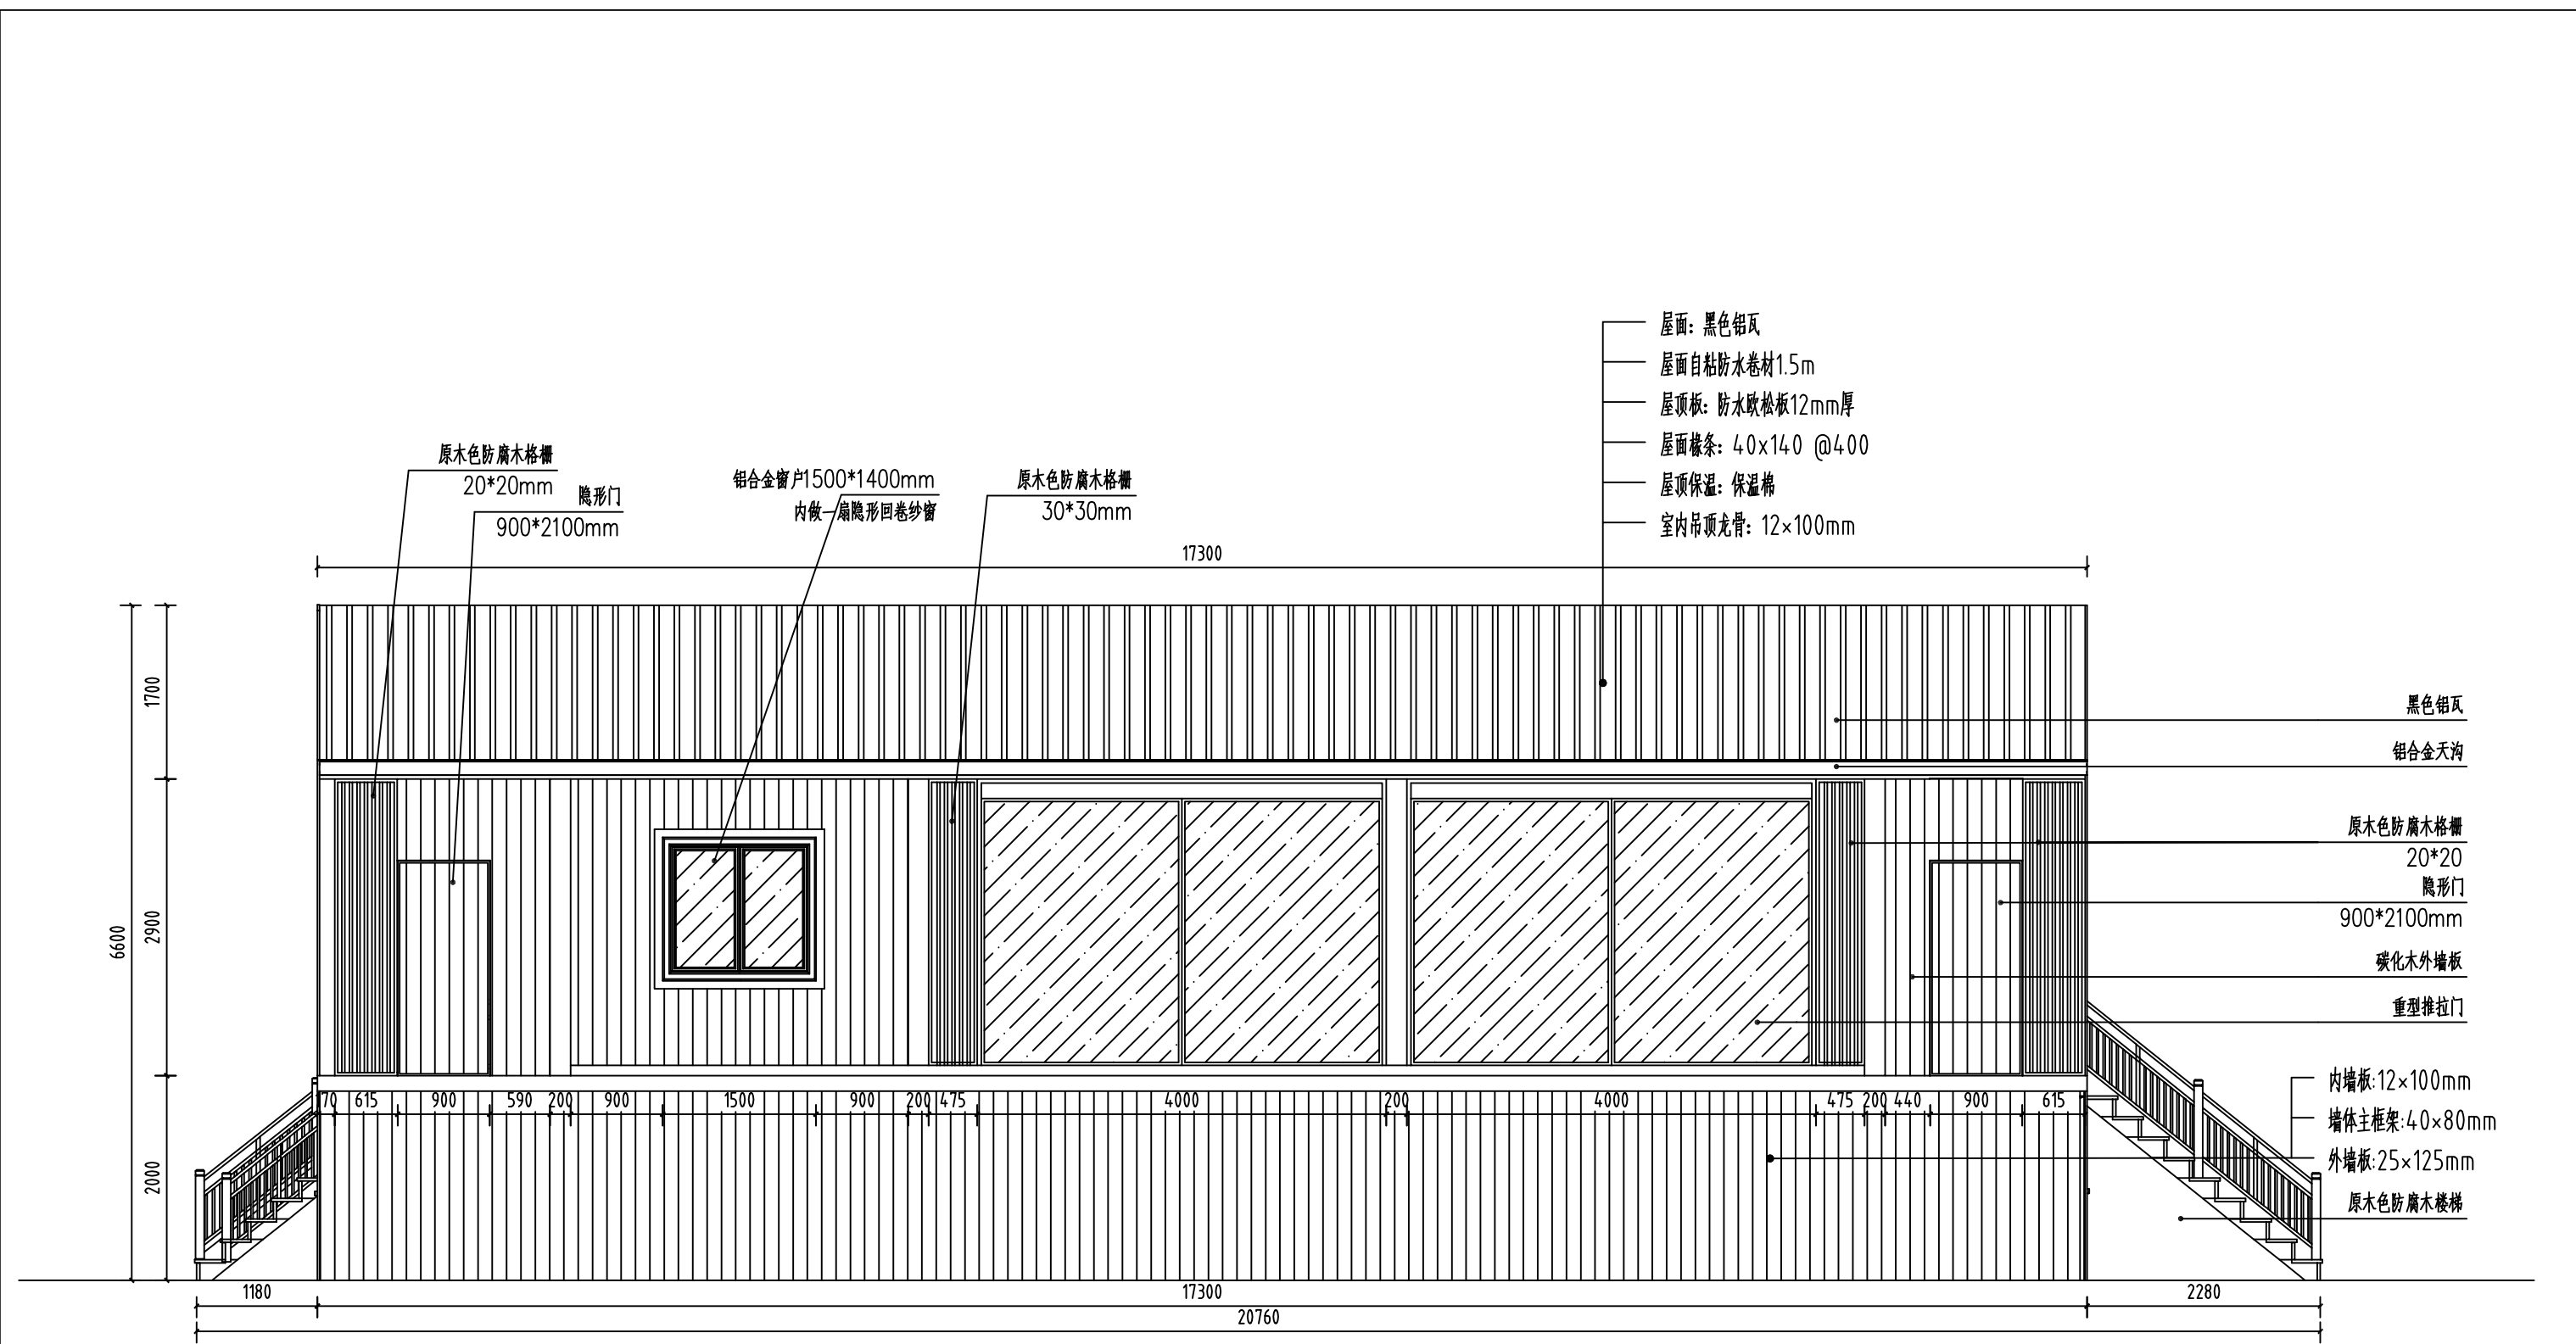


前立面图 1: 60

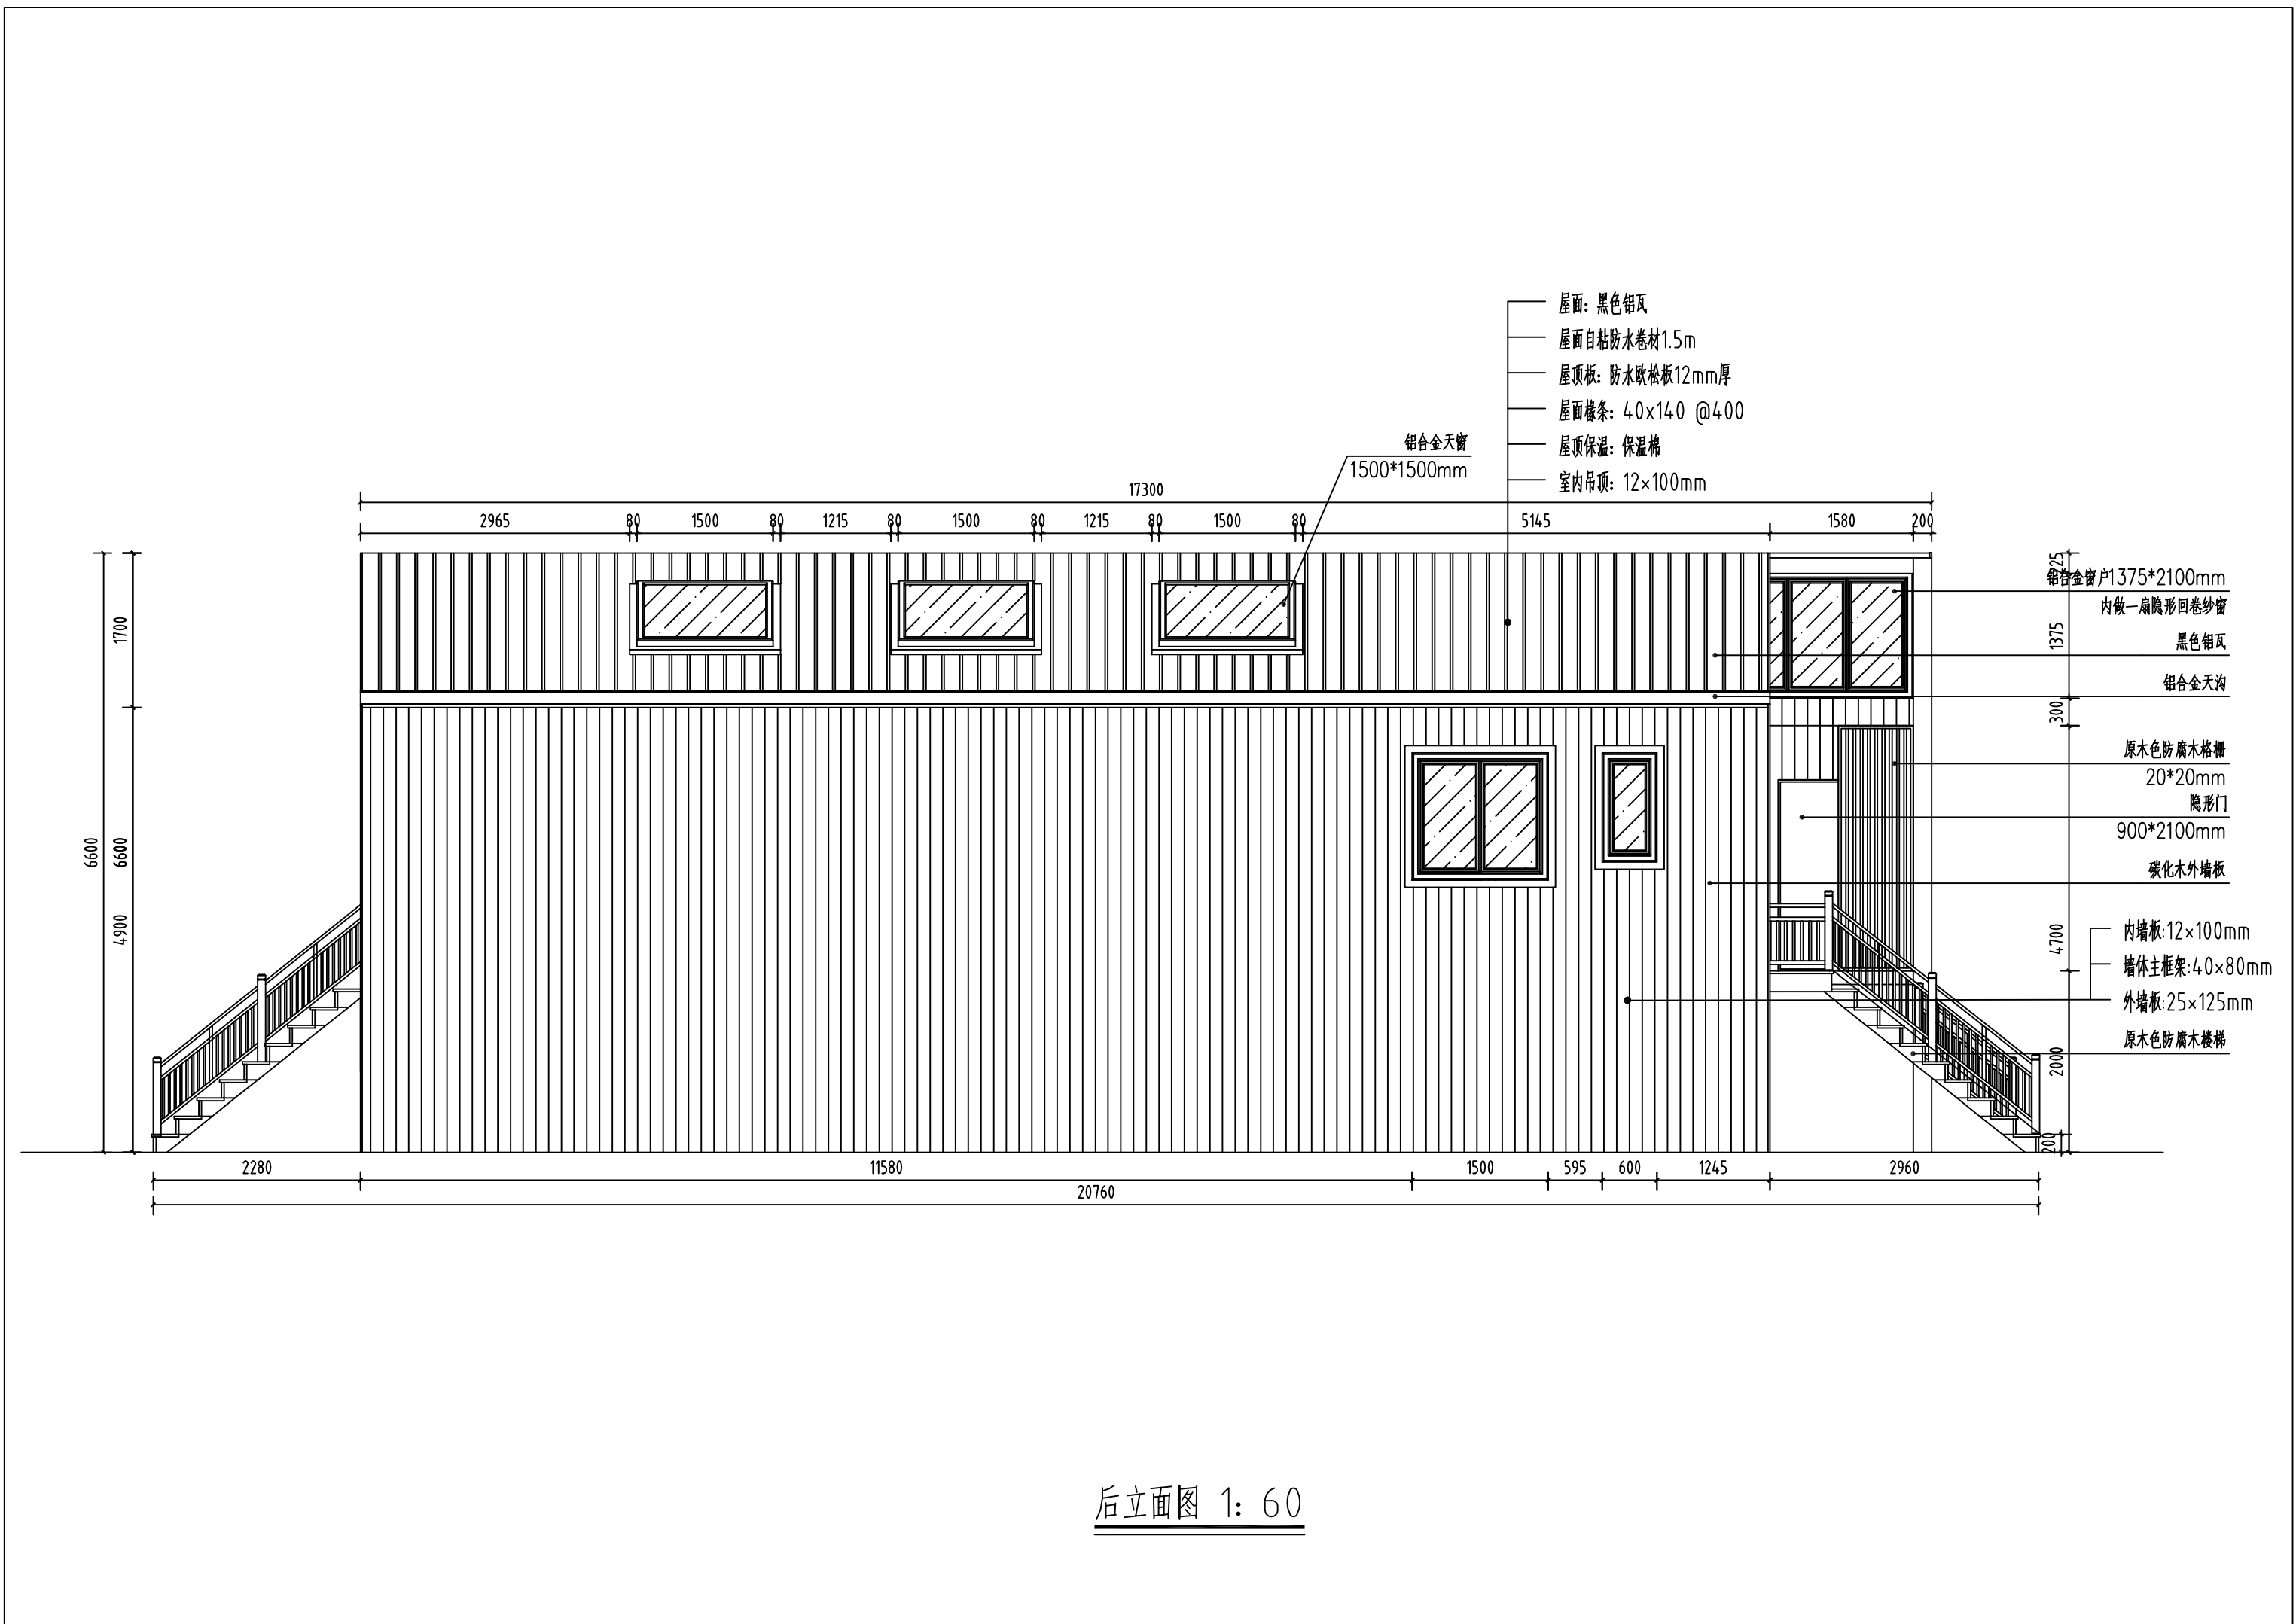


后立面图 1: 60

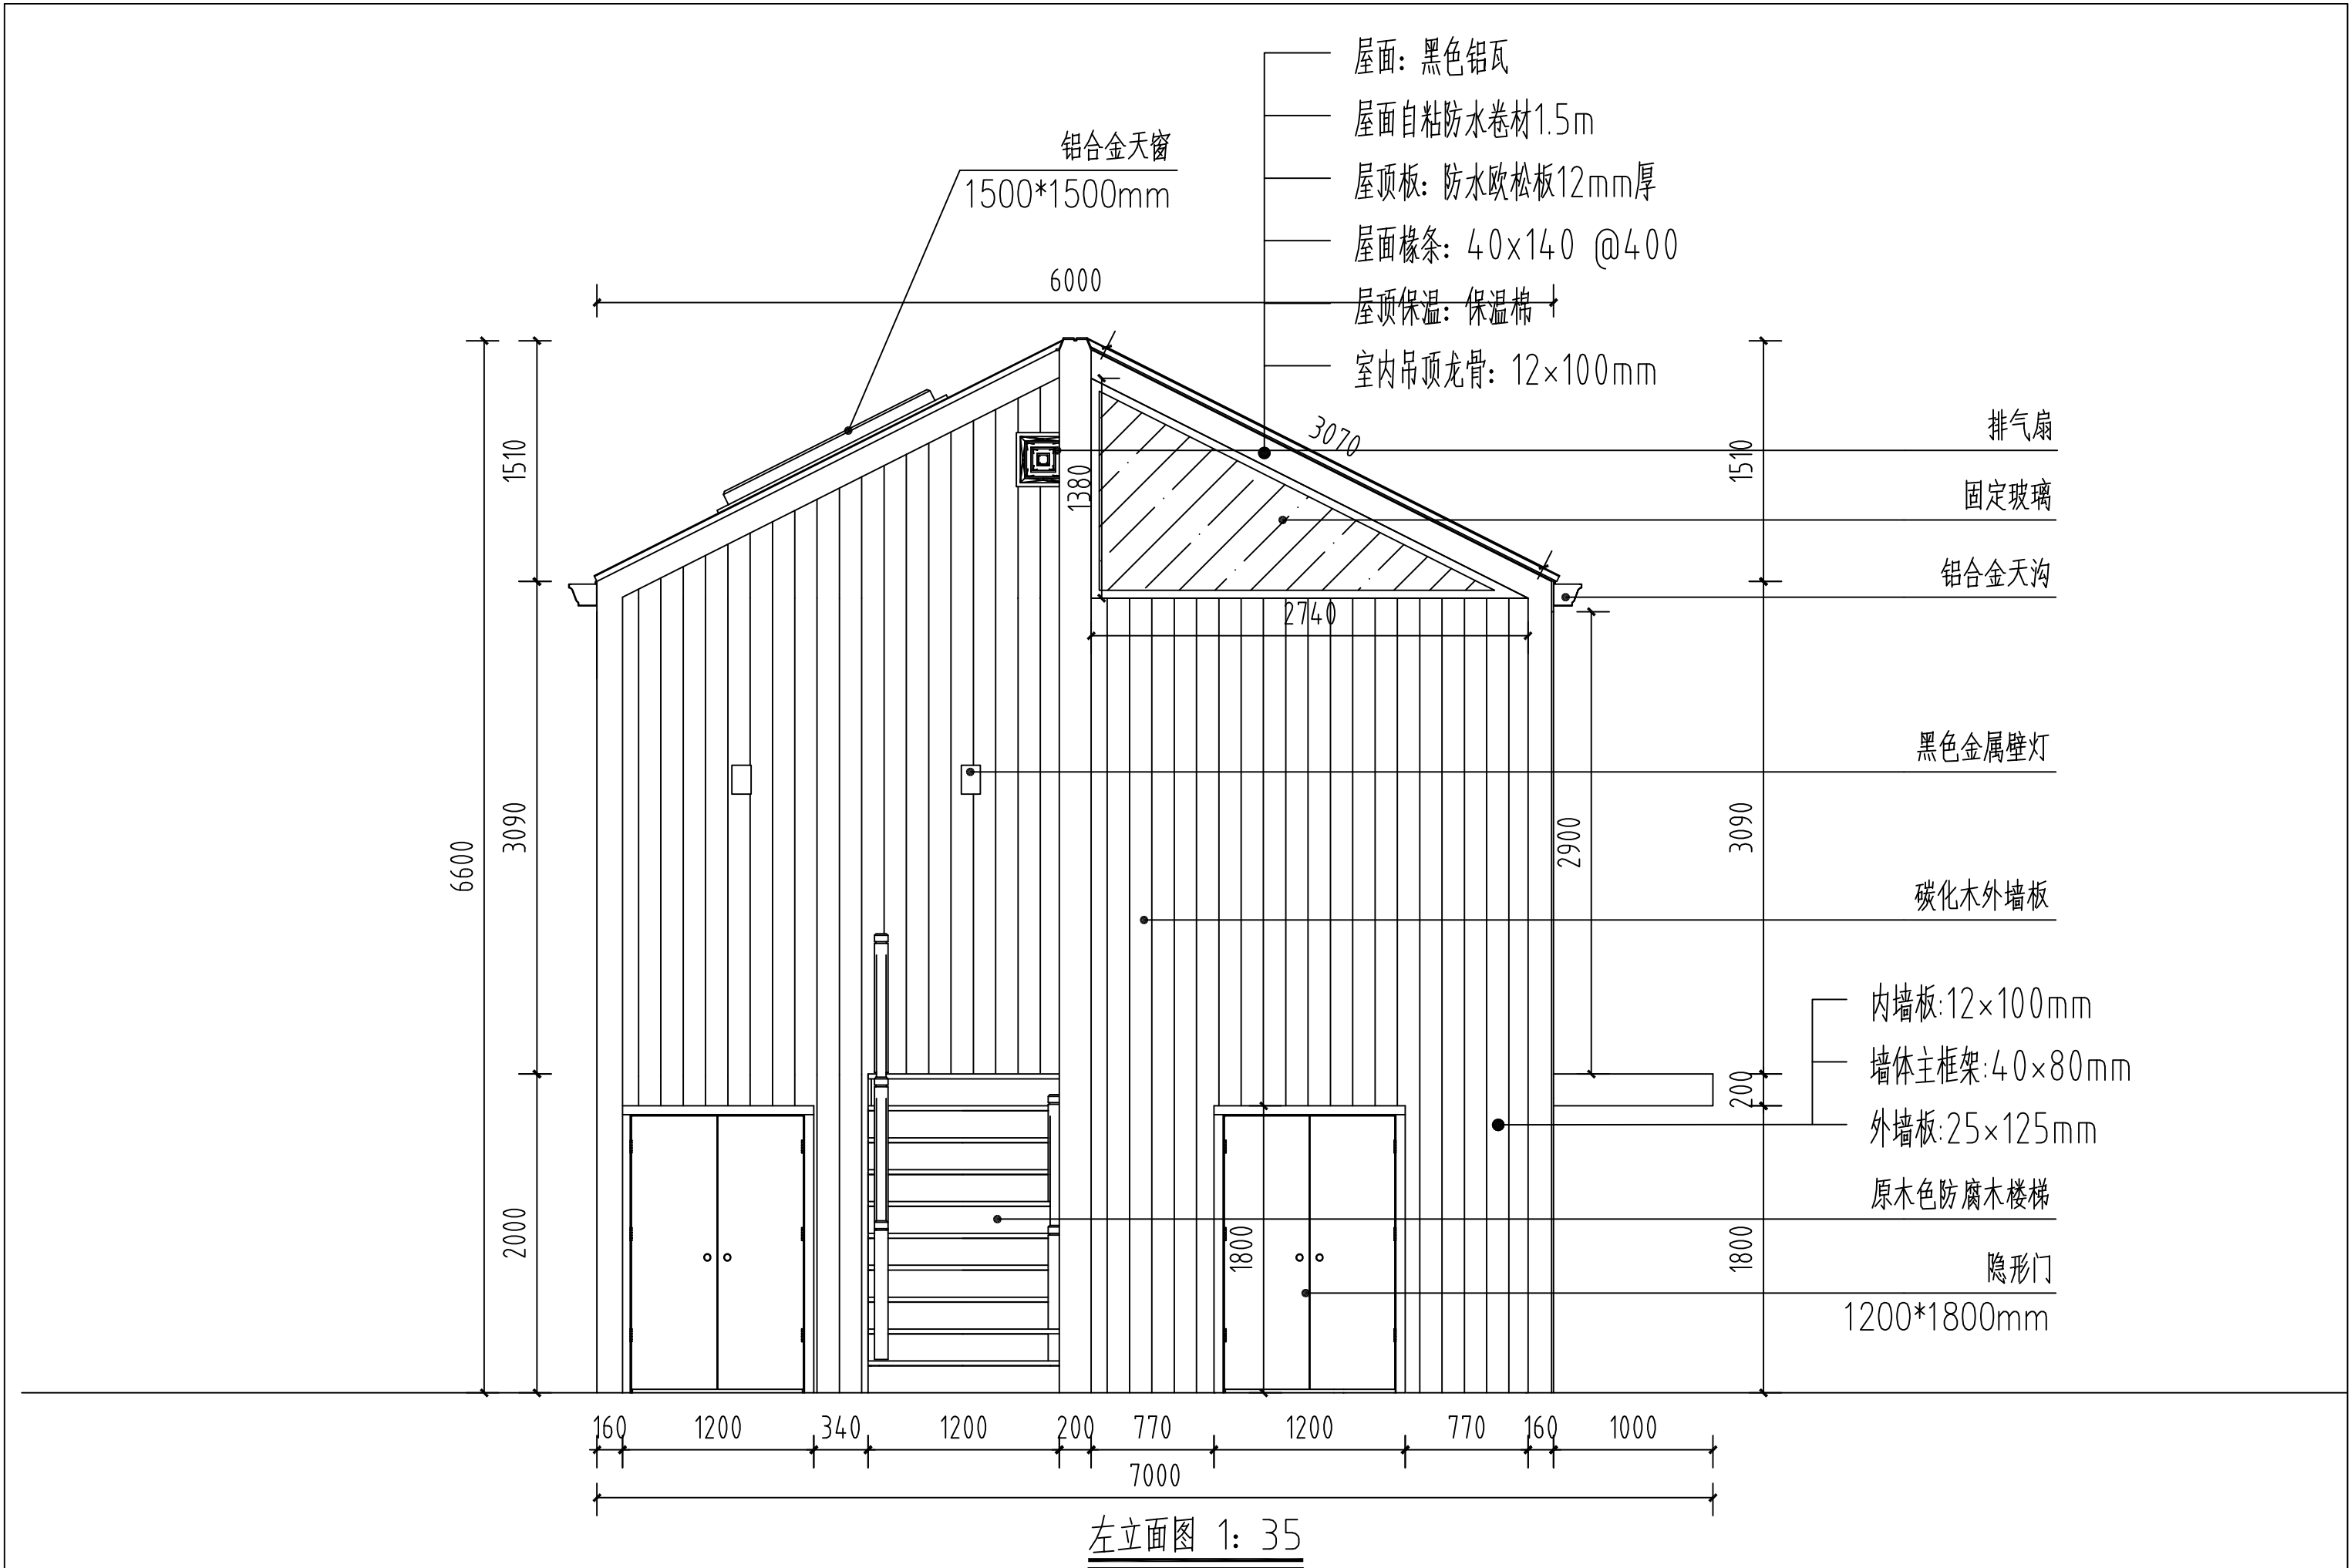


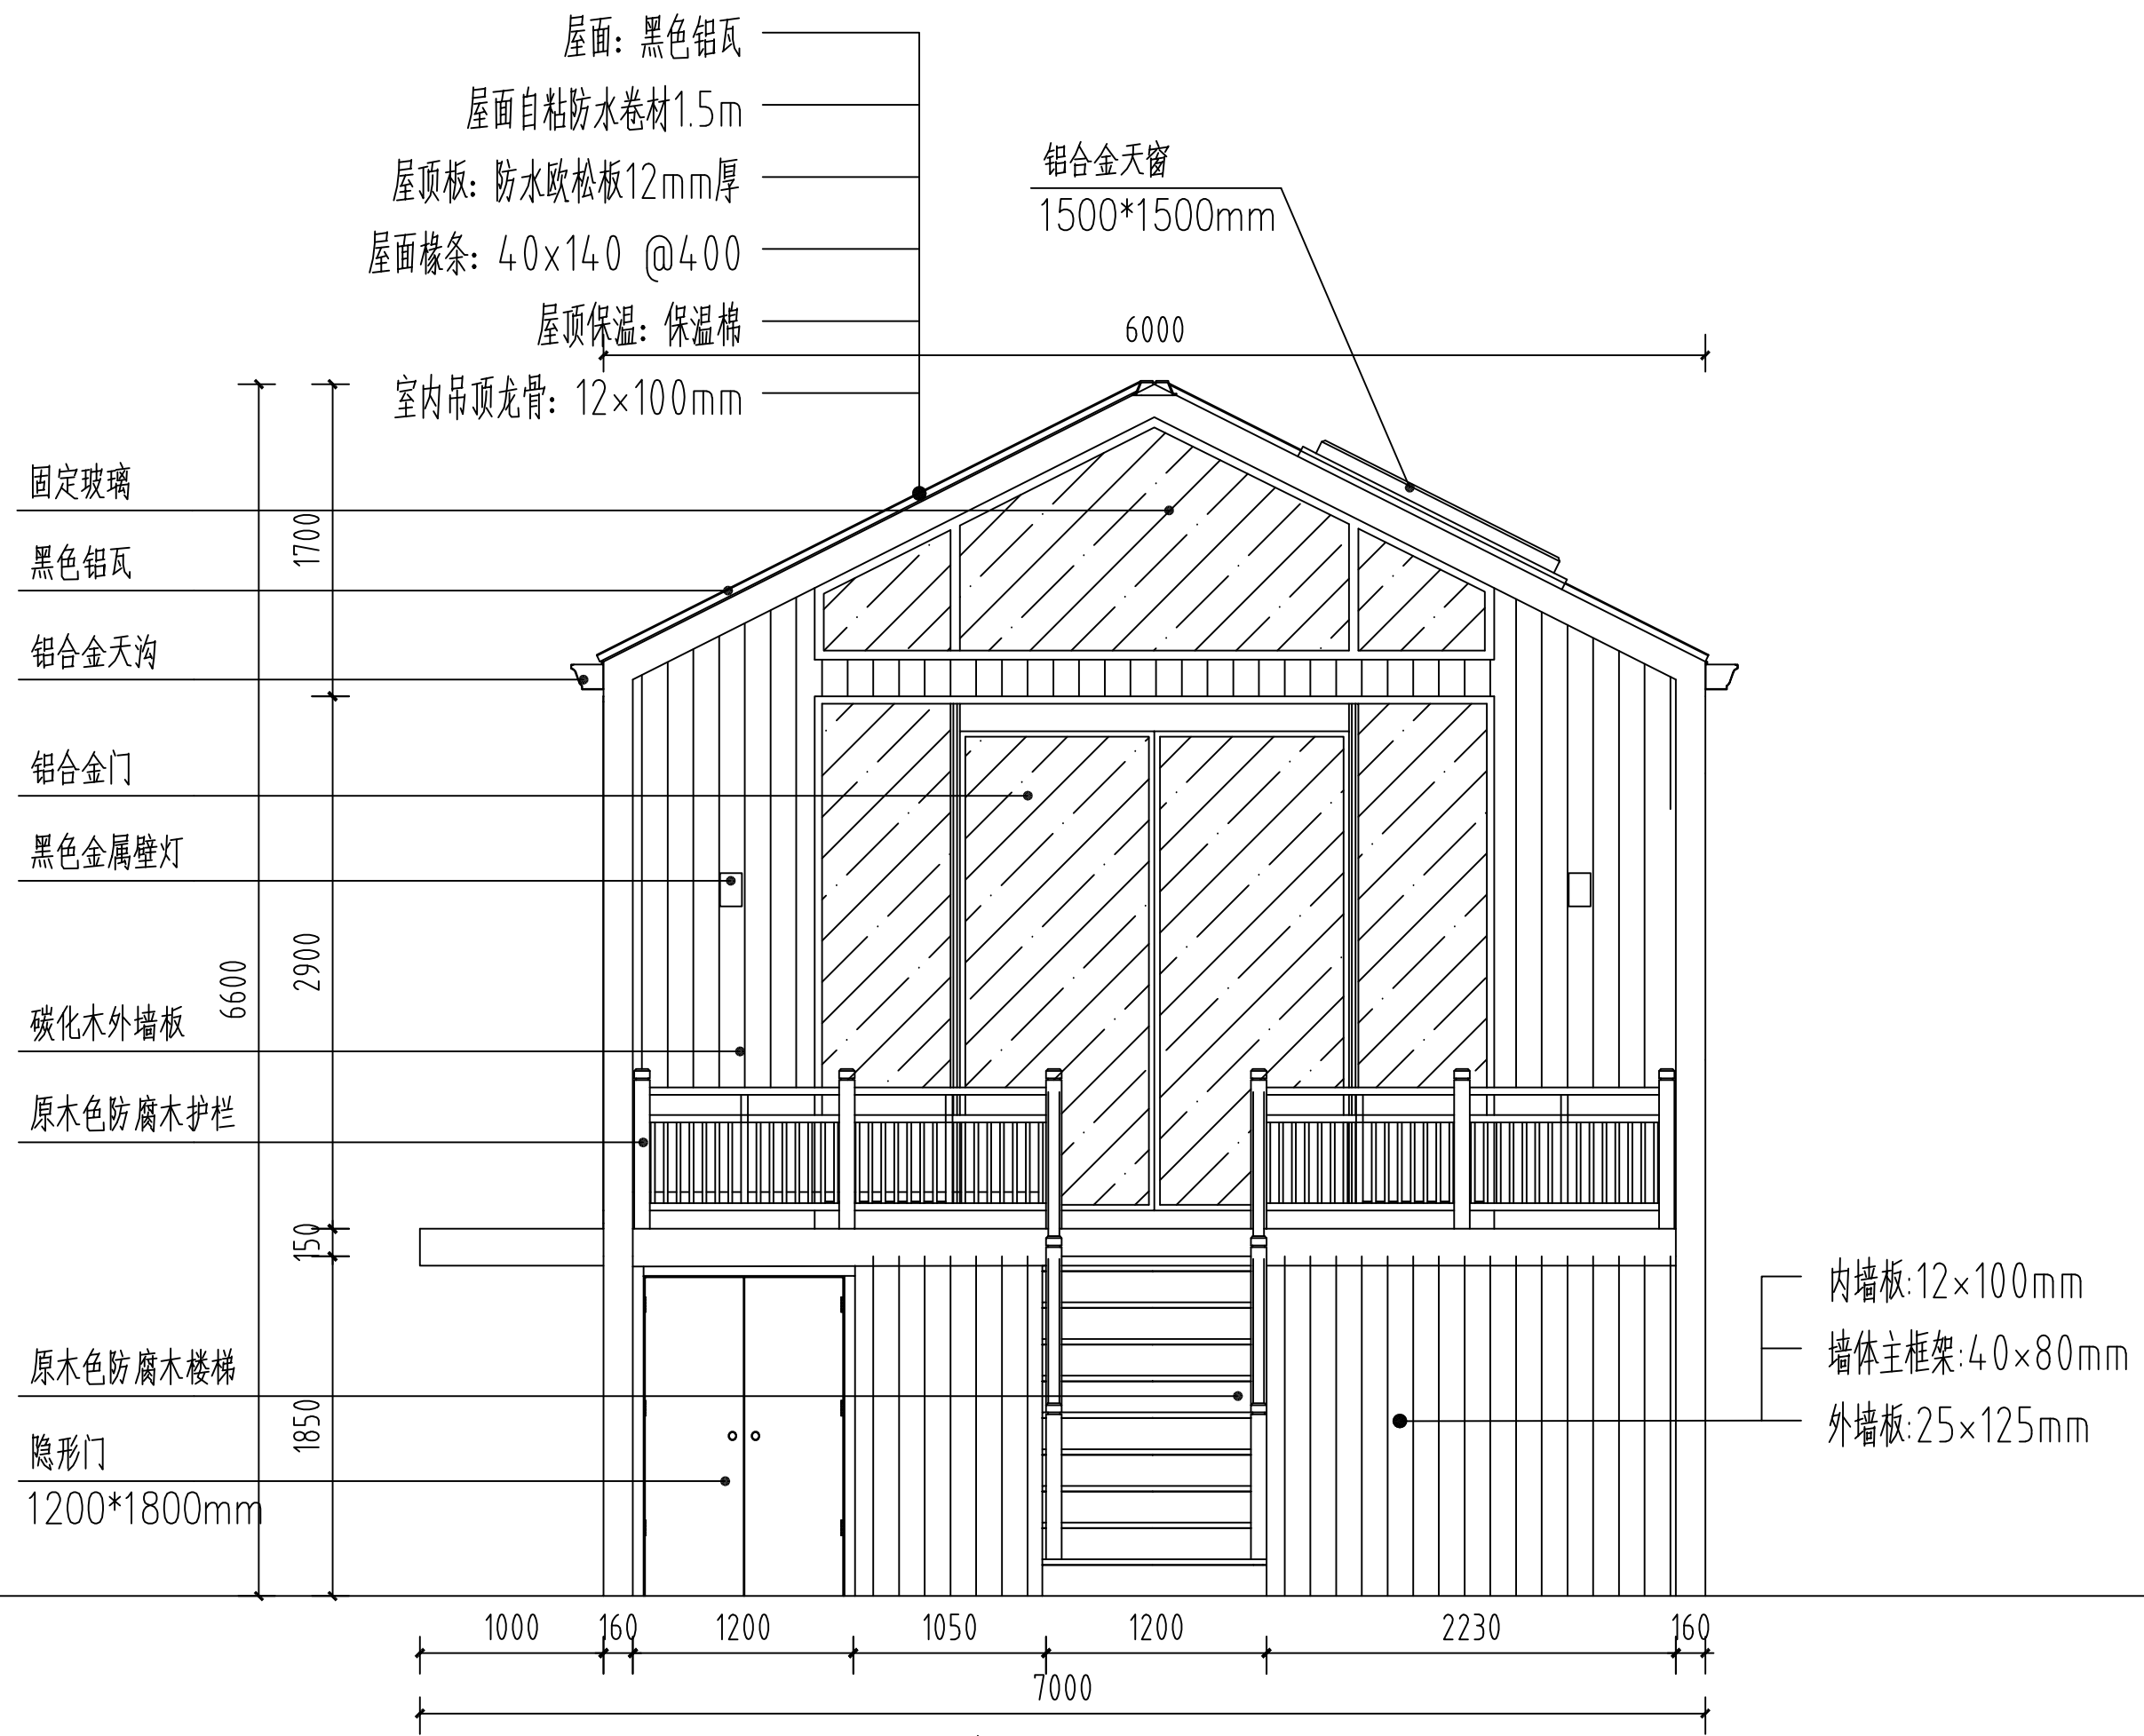


右立面图 1: 35

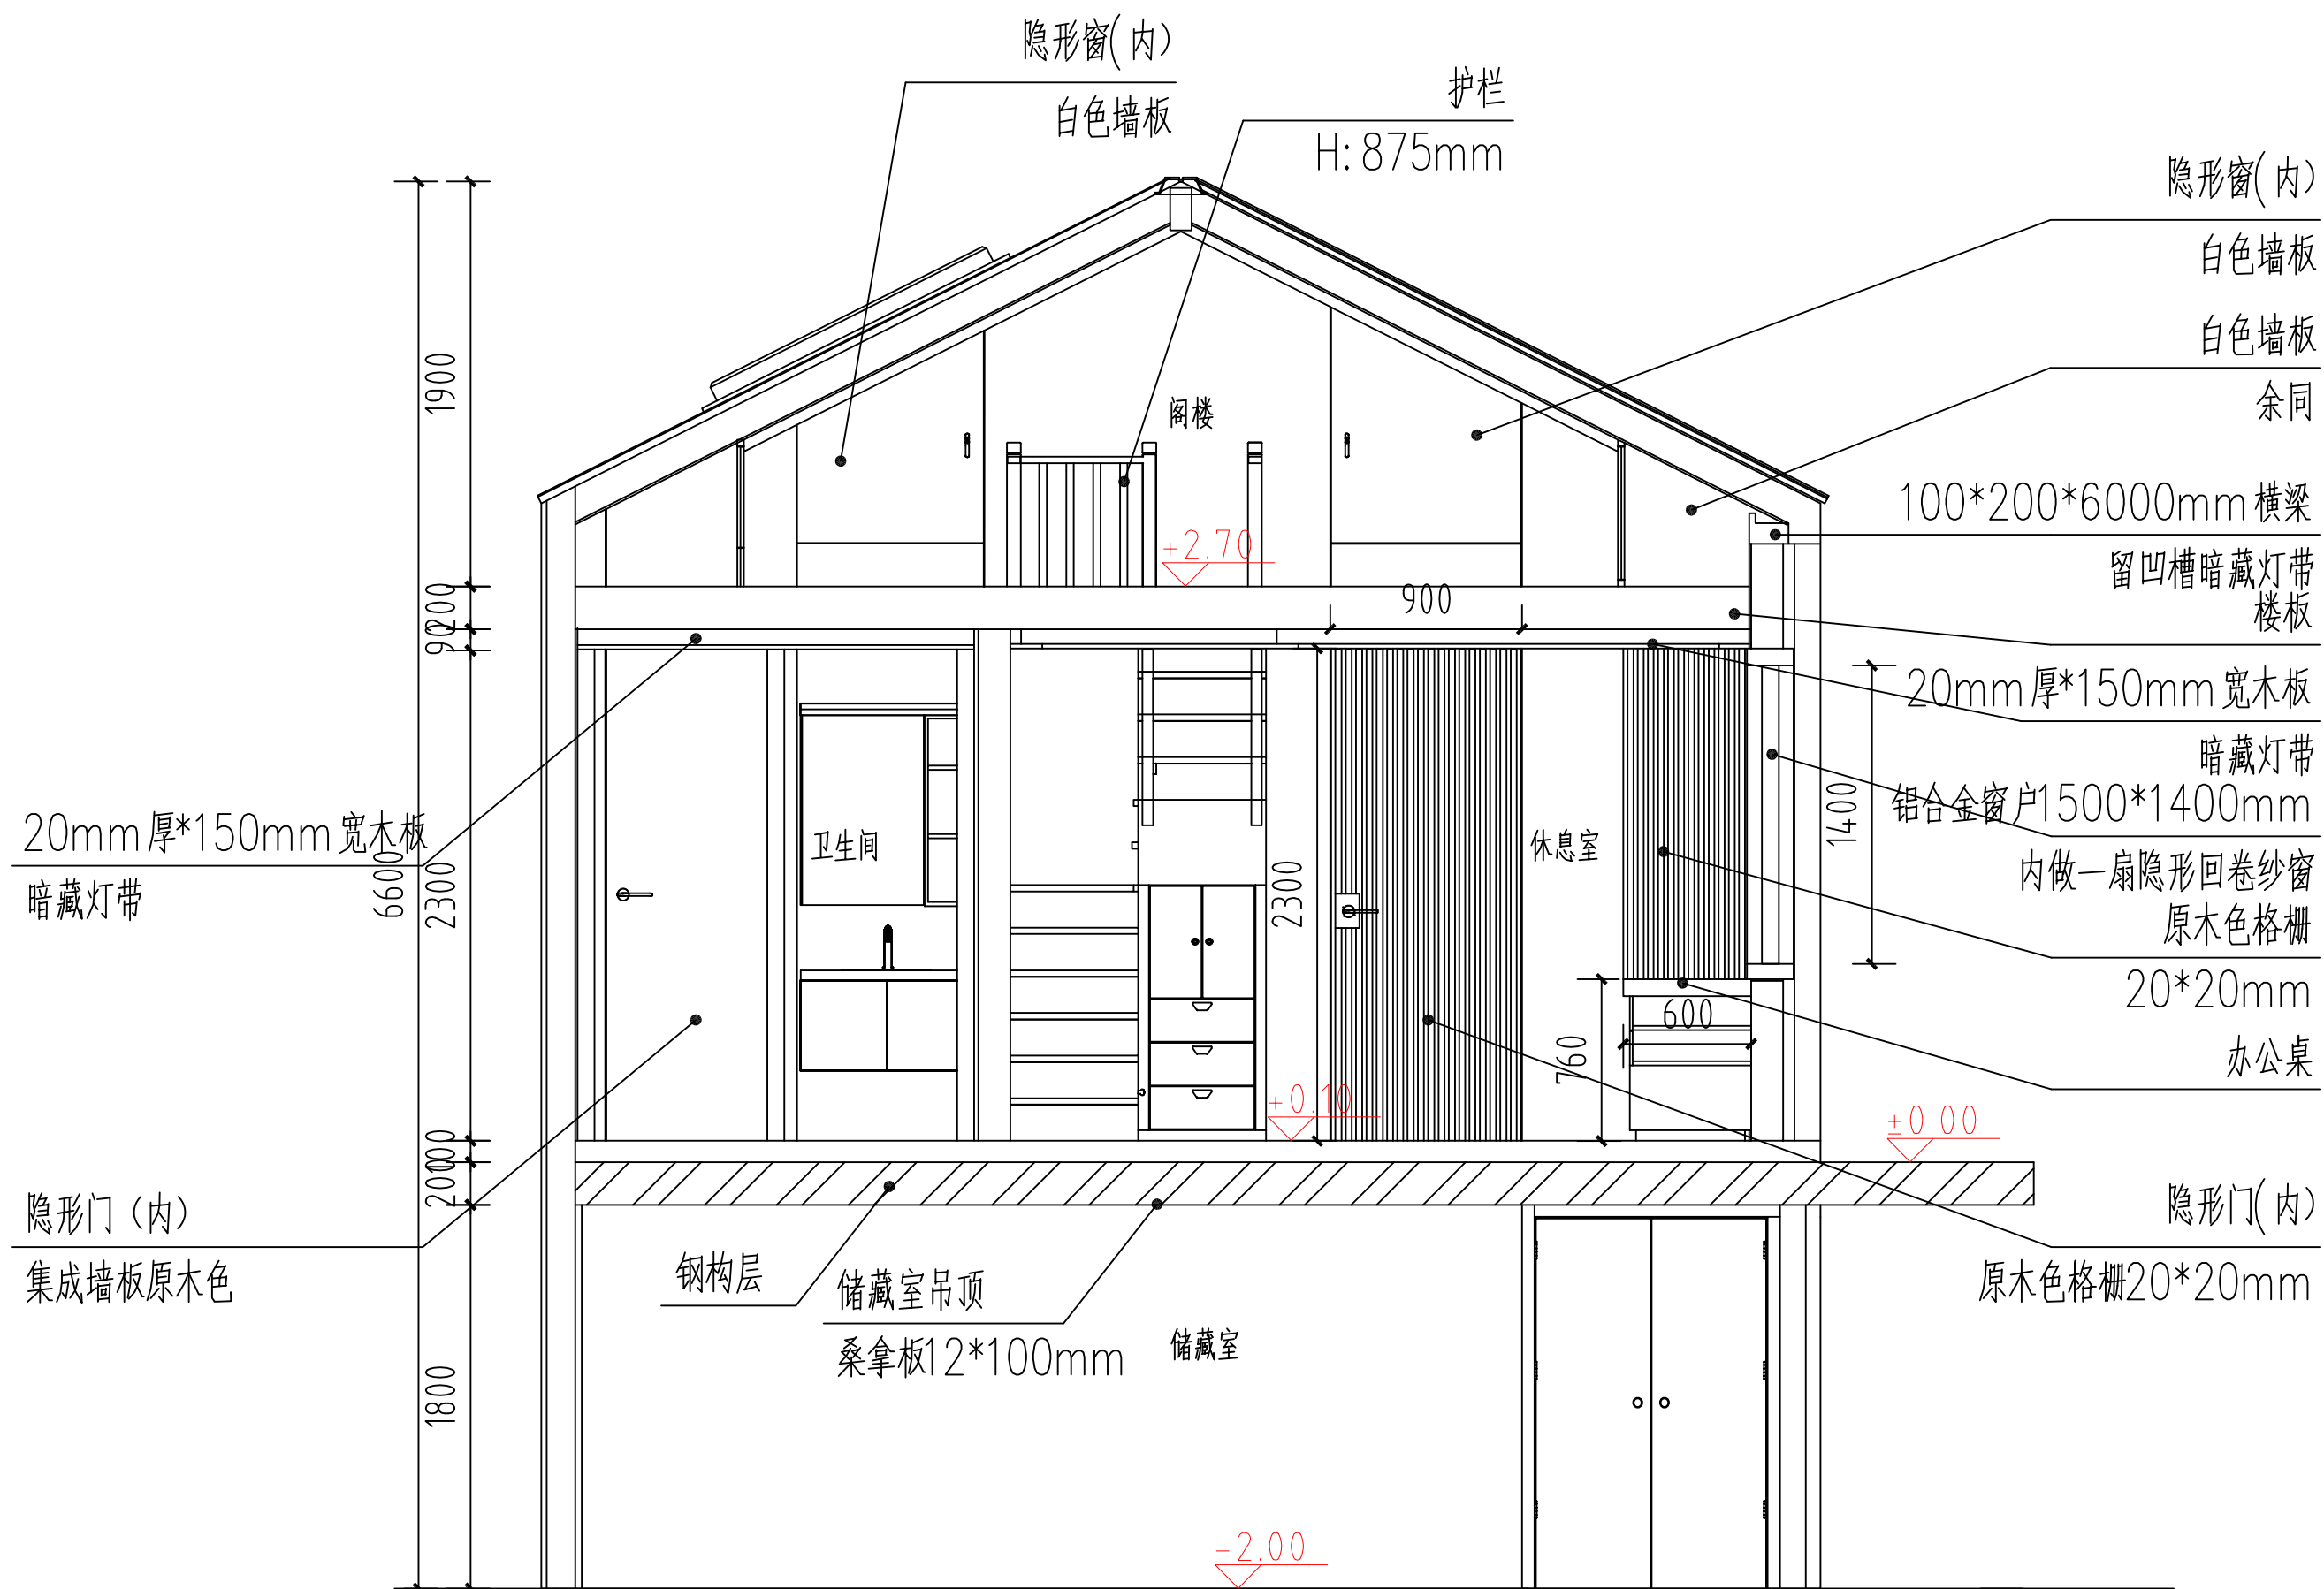


1-1剖面图 1:30

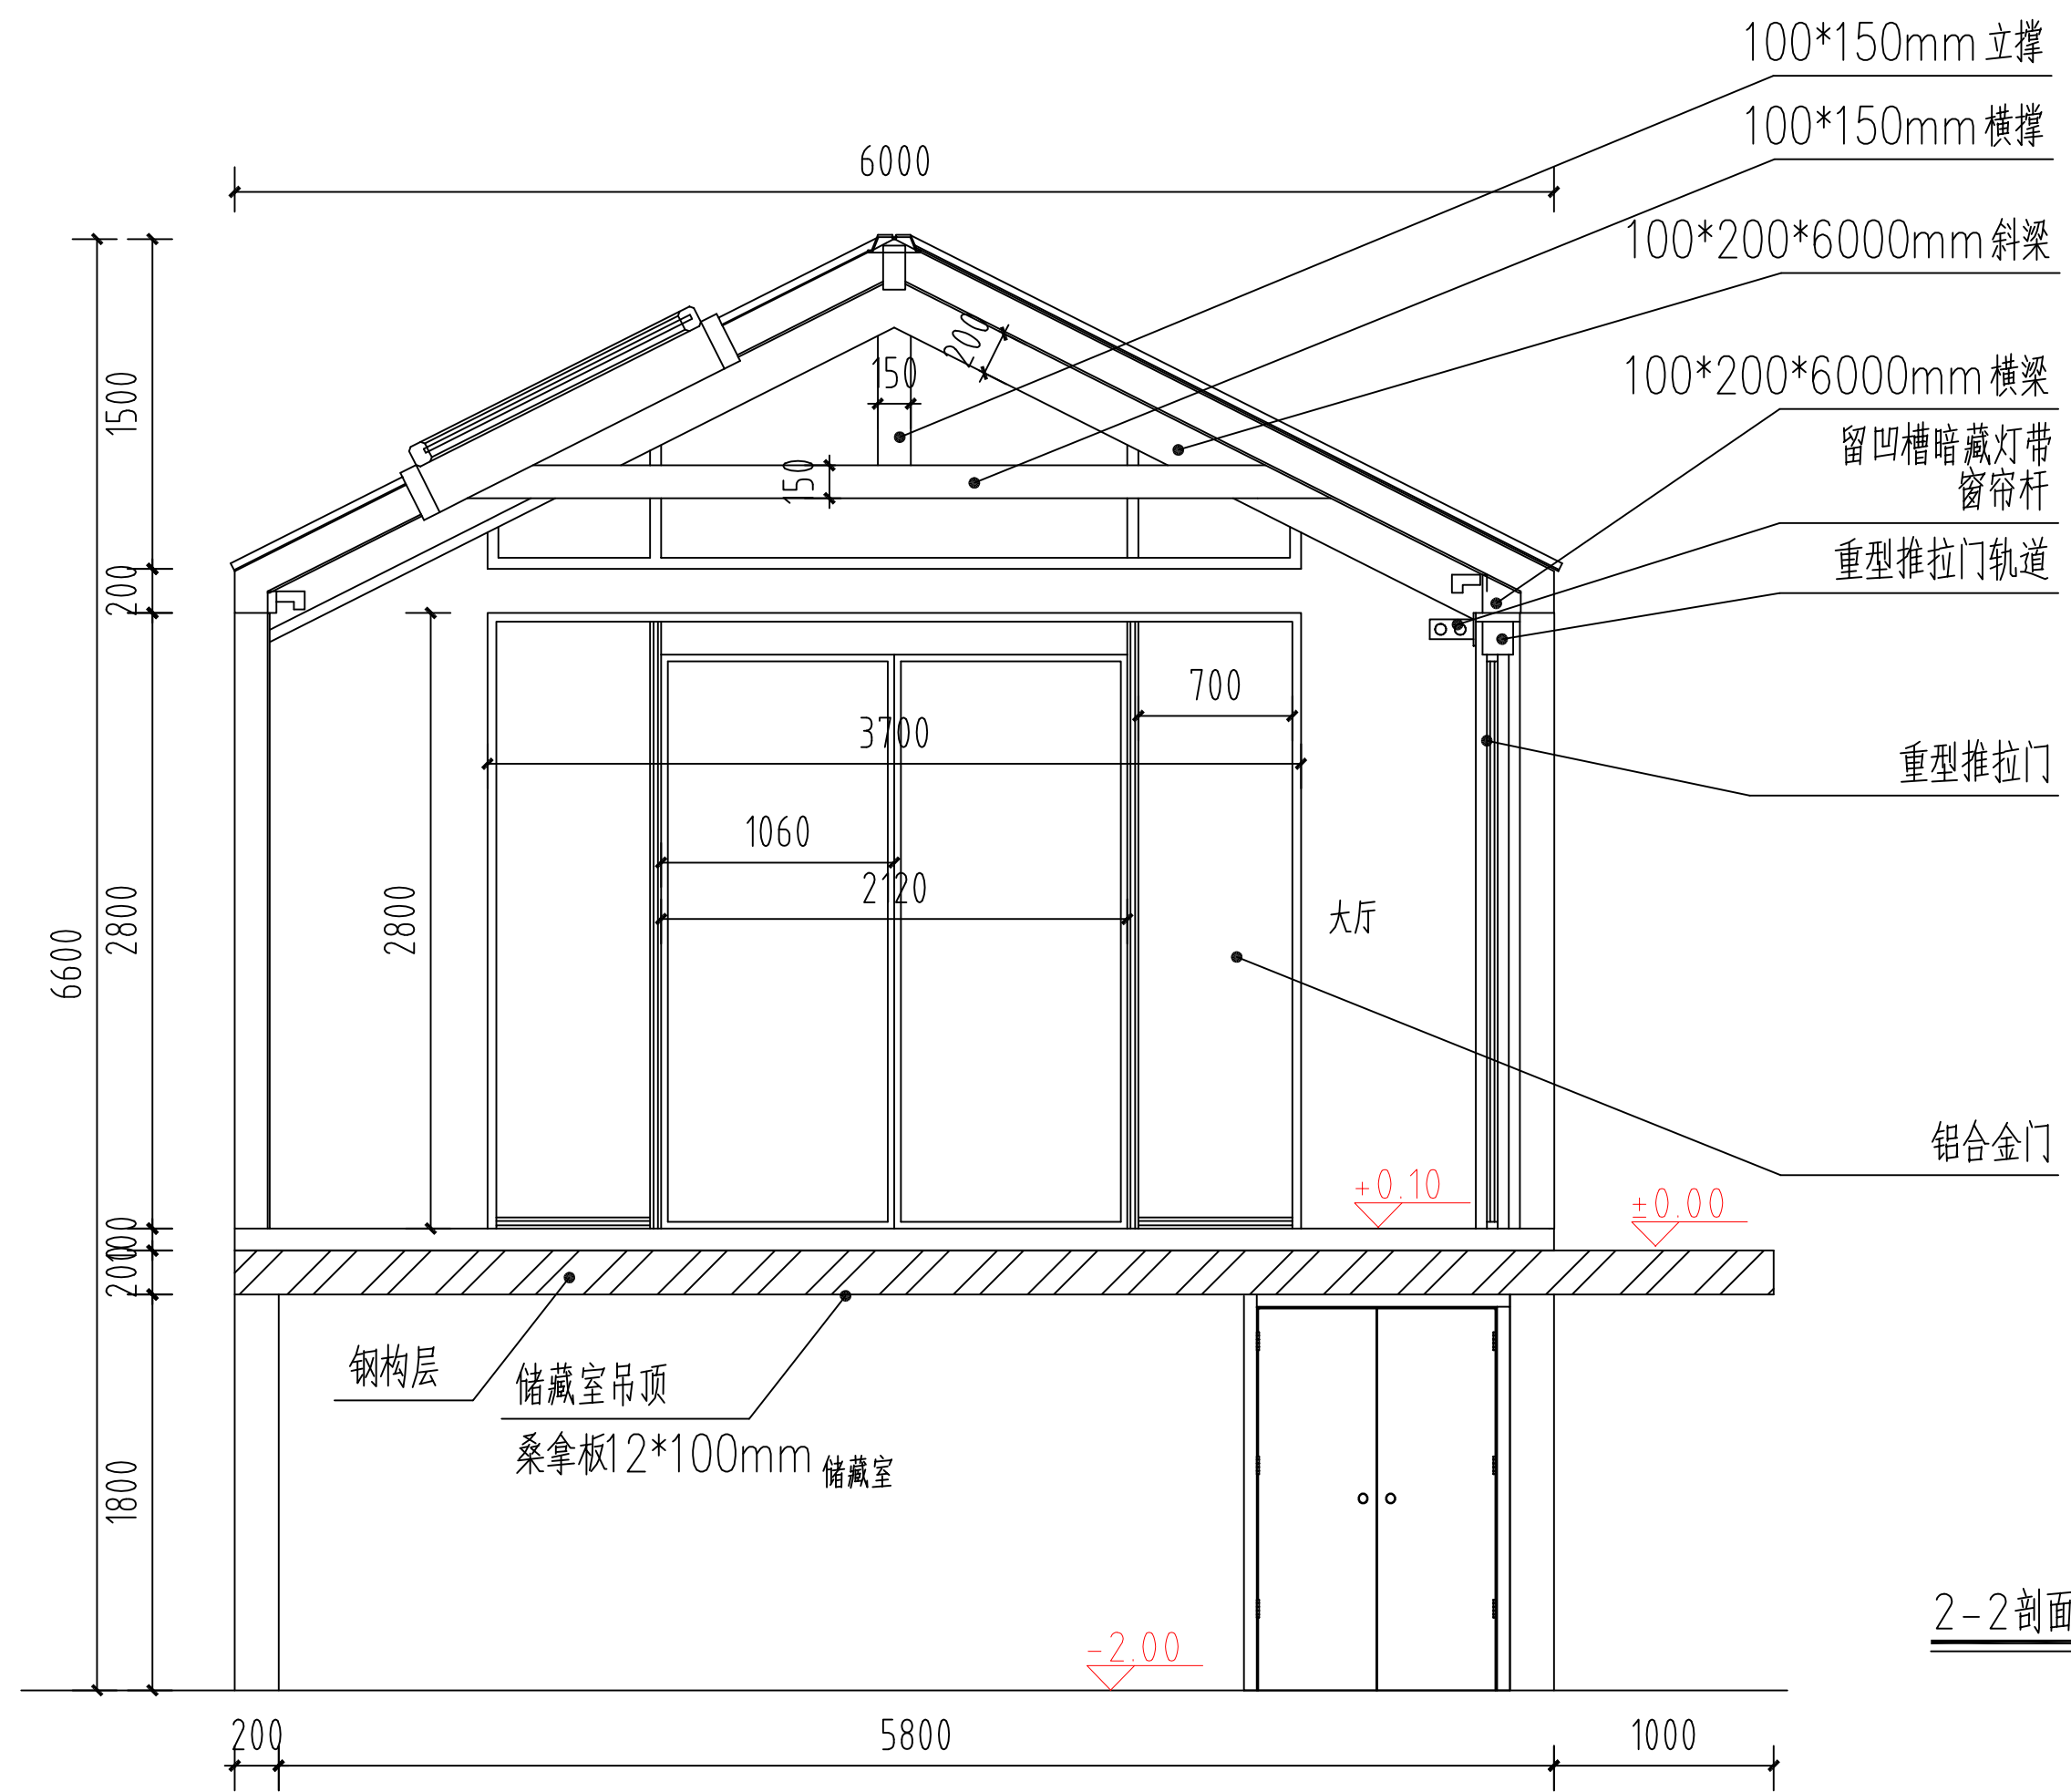


2-2剖面图 1: 30

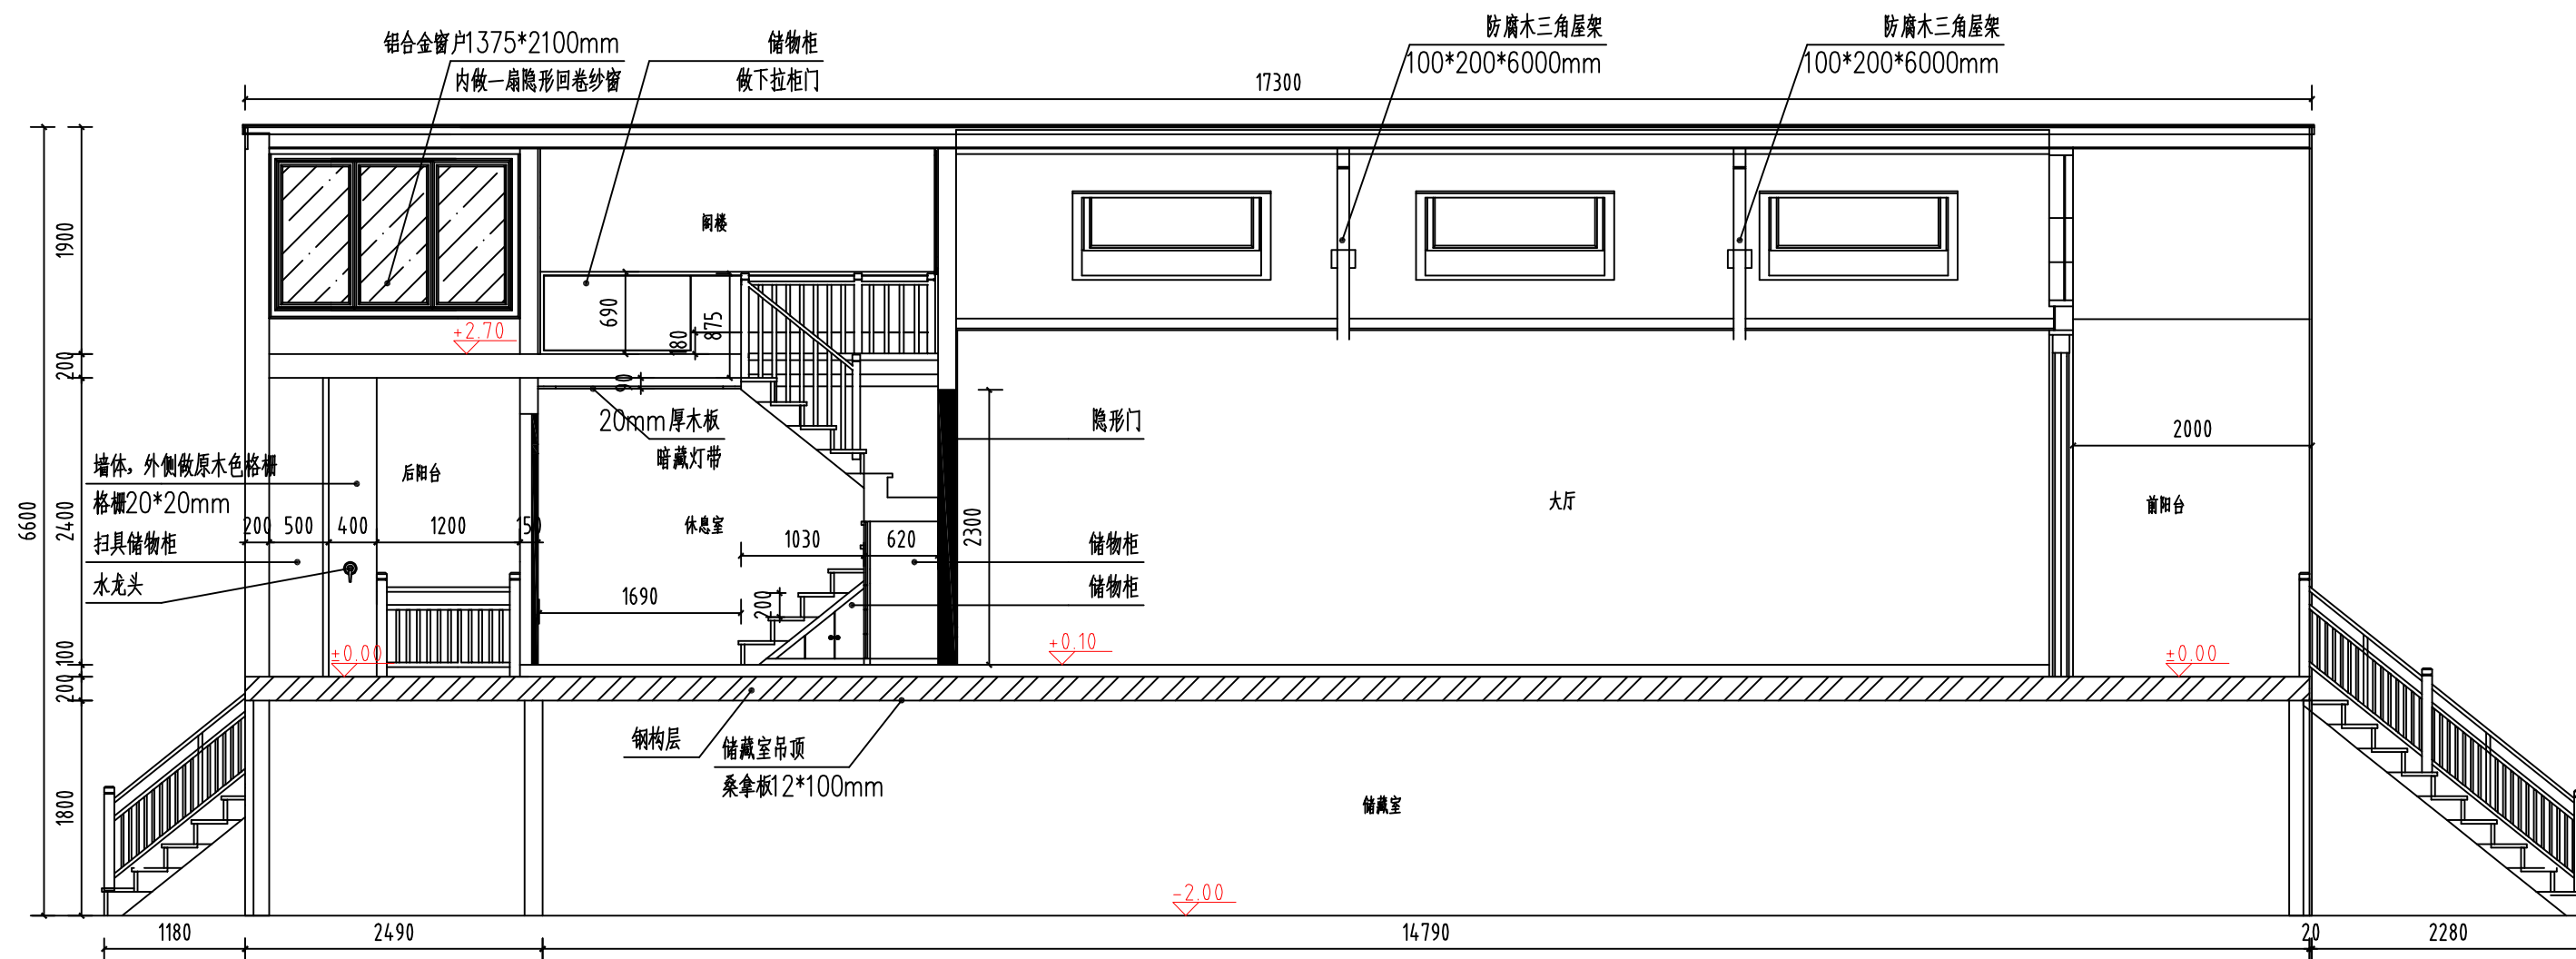


3-3剖面图 1: 55

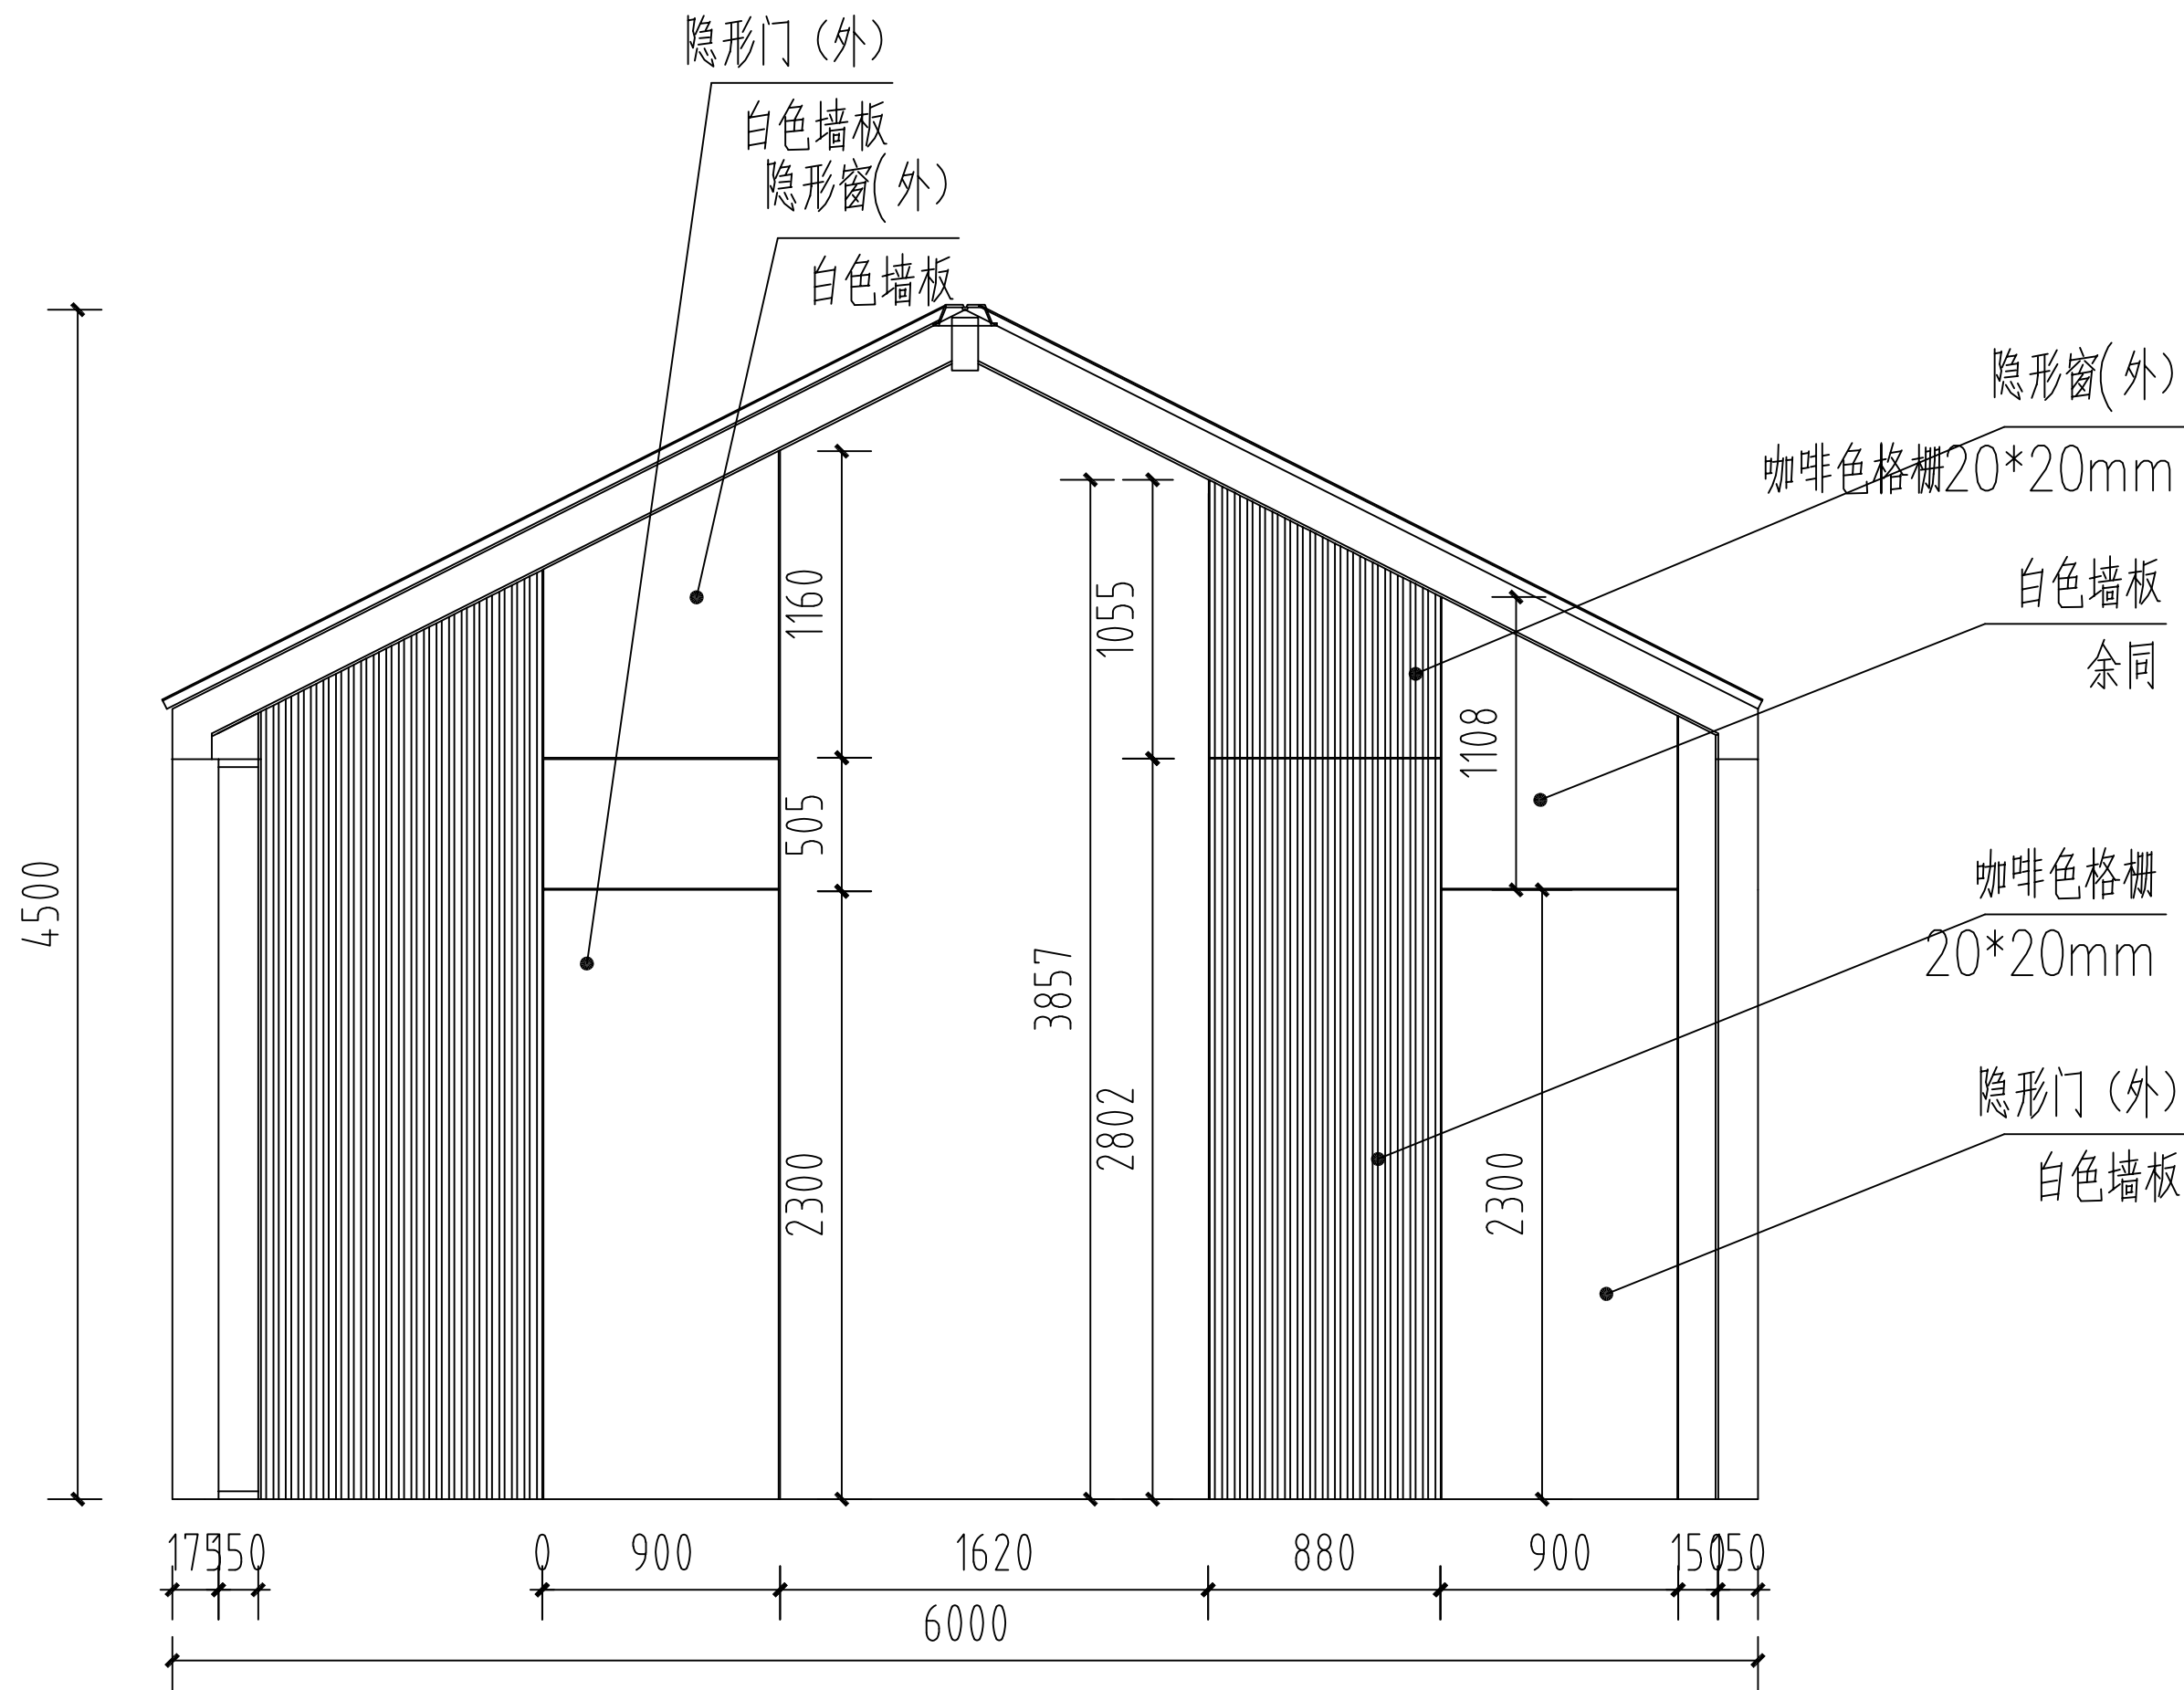


A内视图 1: 25

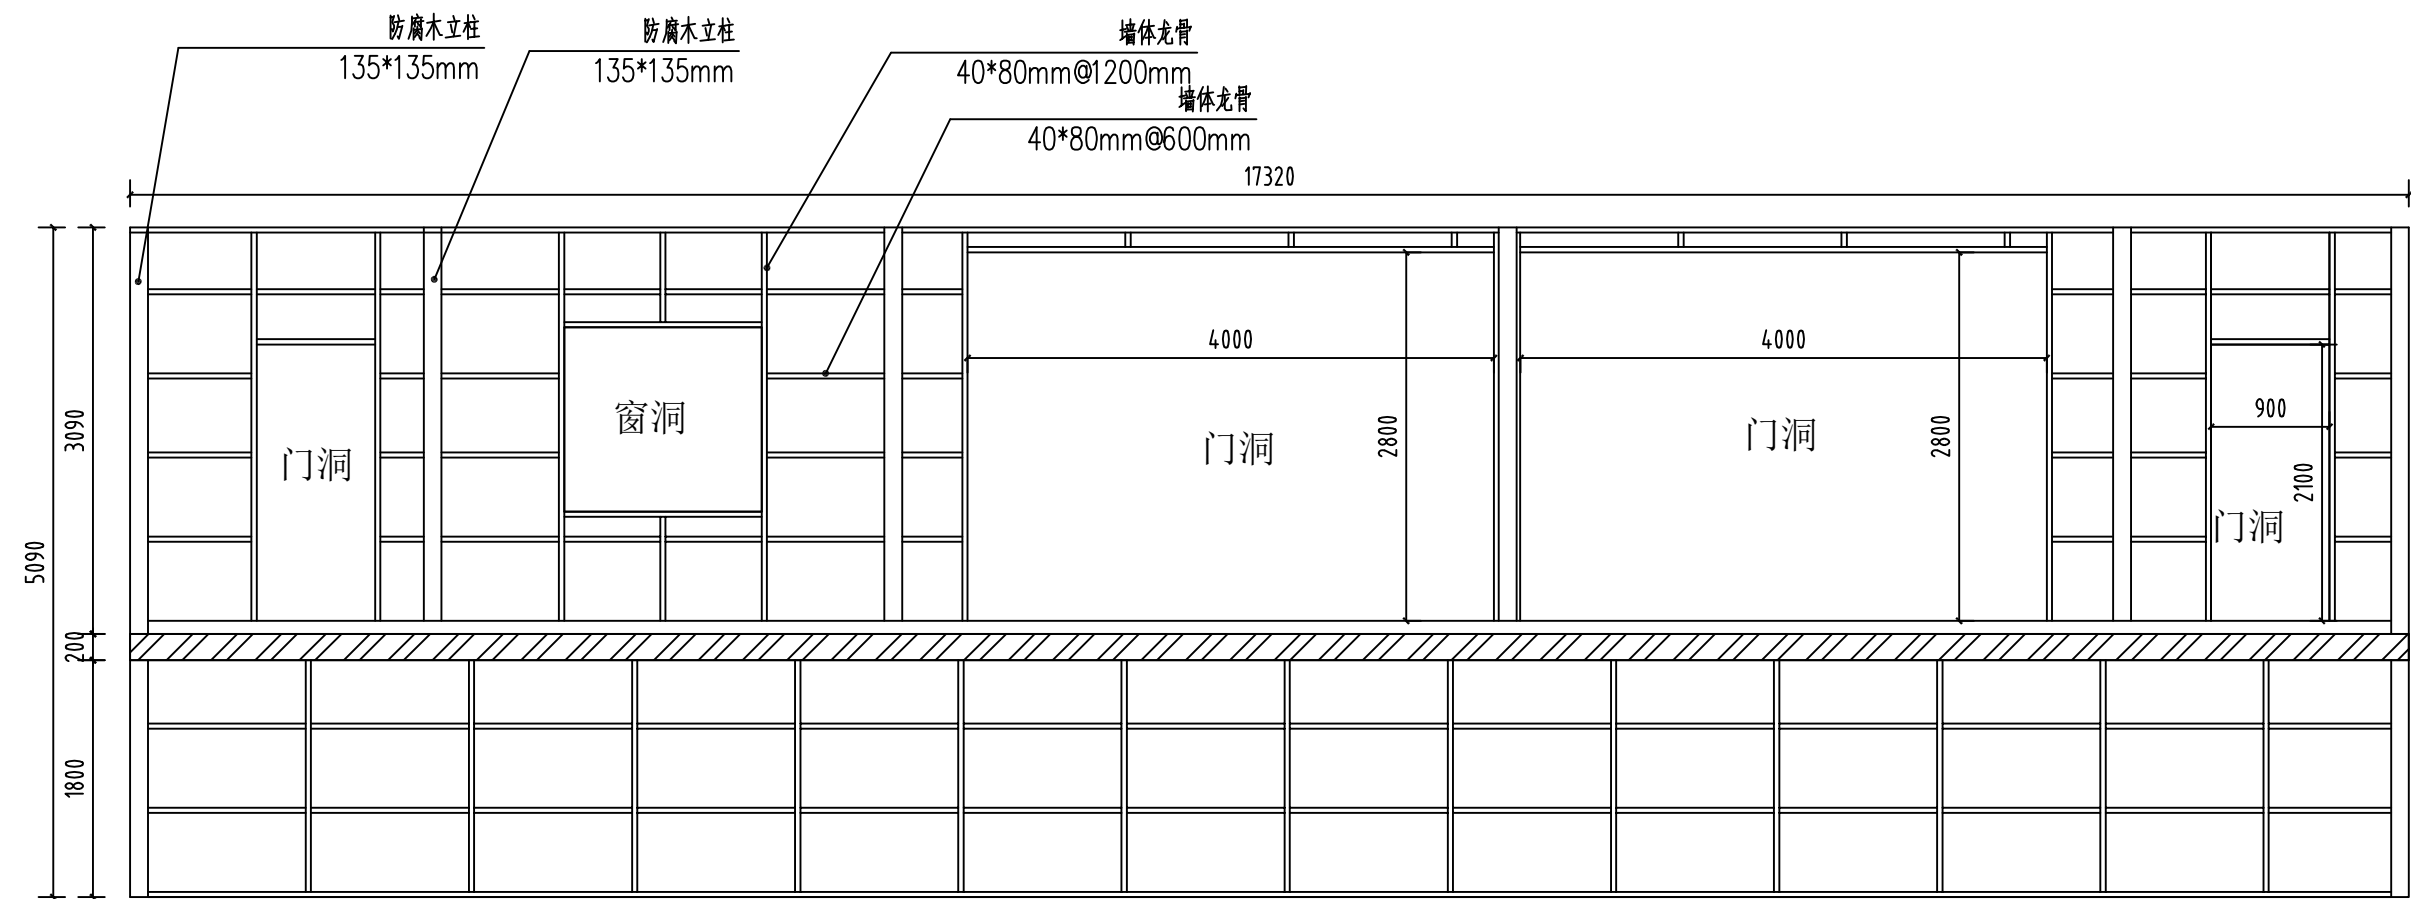


①墙体结构图 1: 30

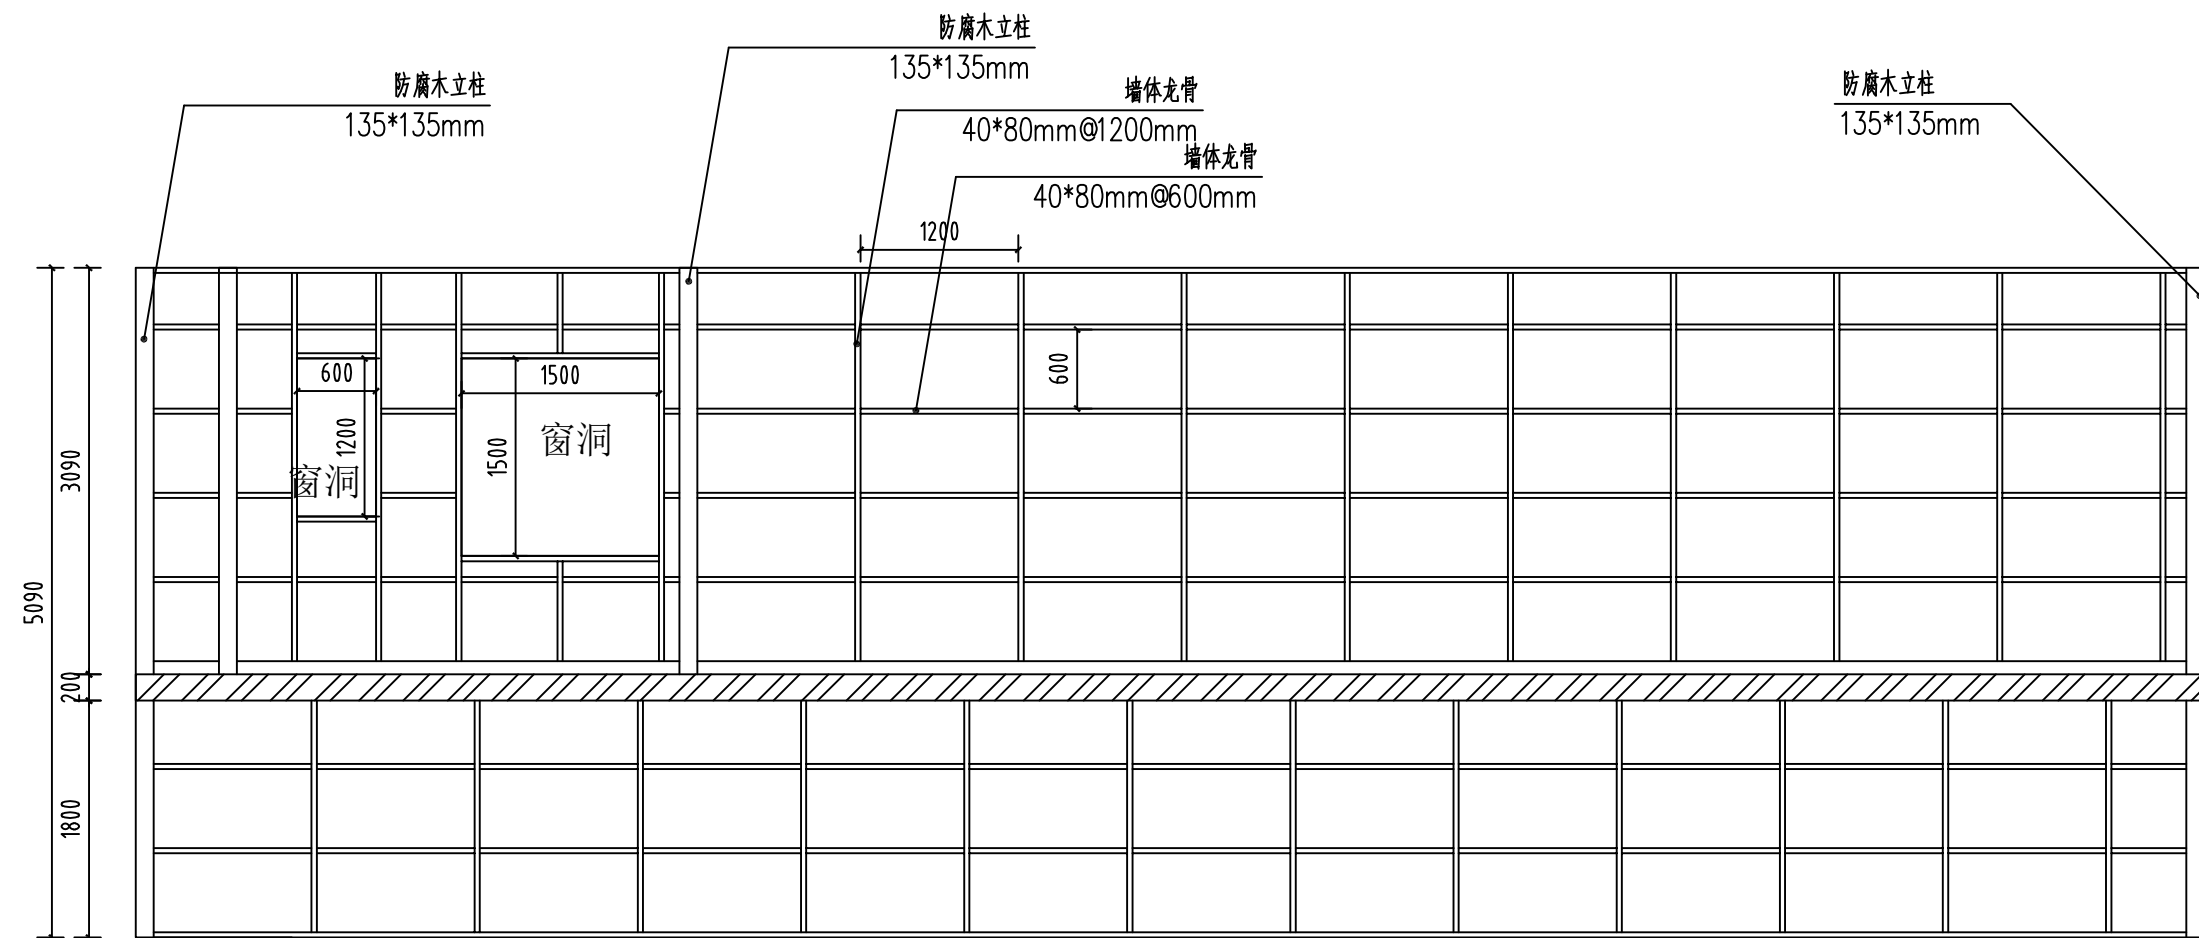


③墙体结构图 1: 30

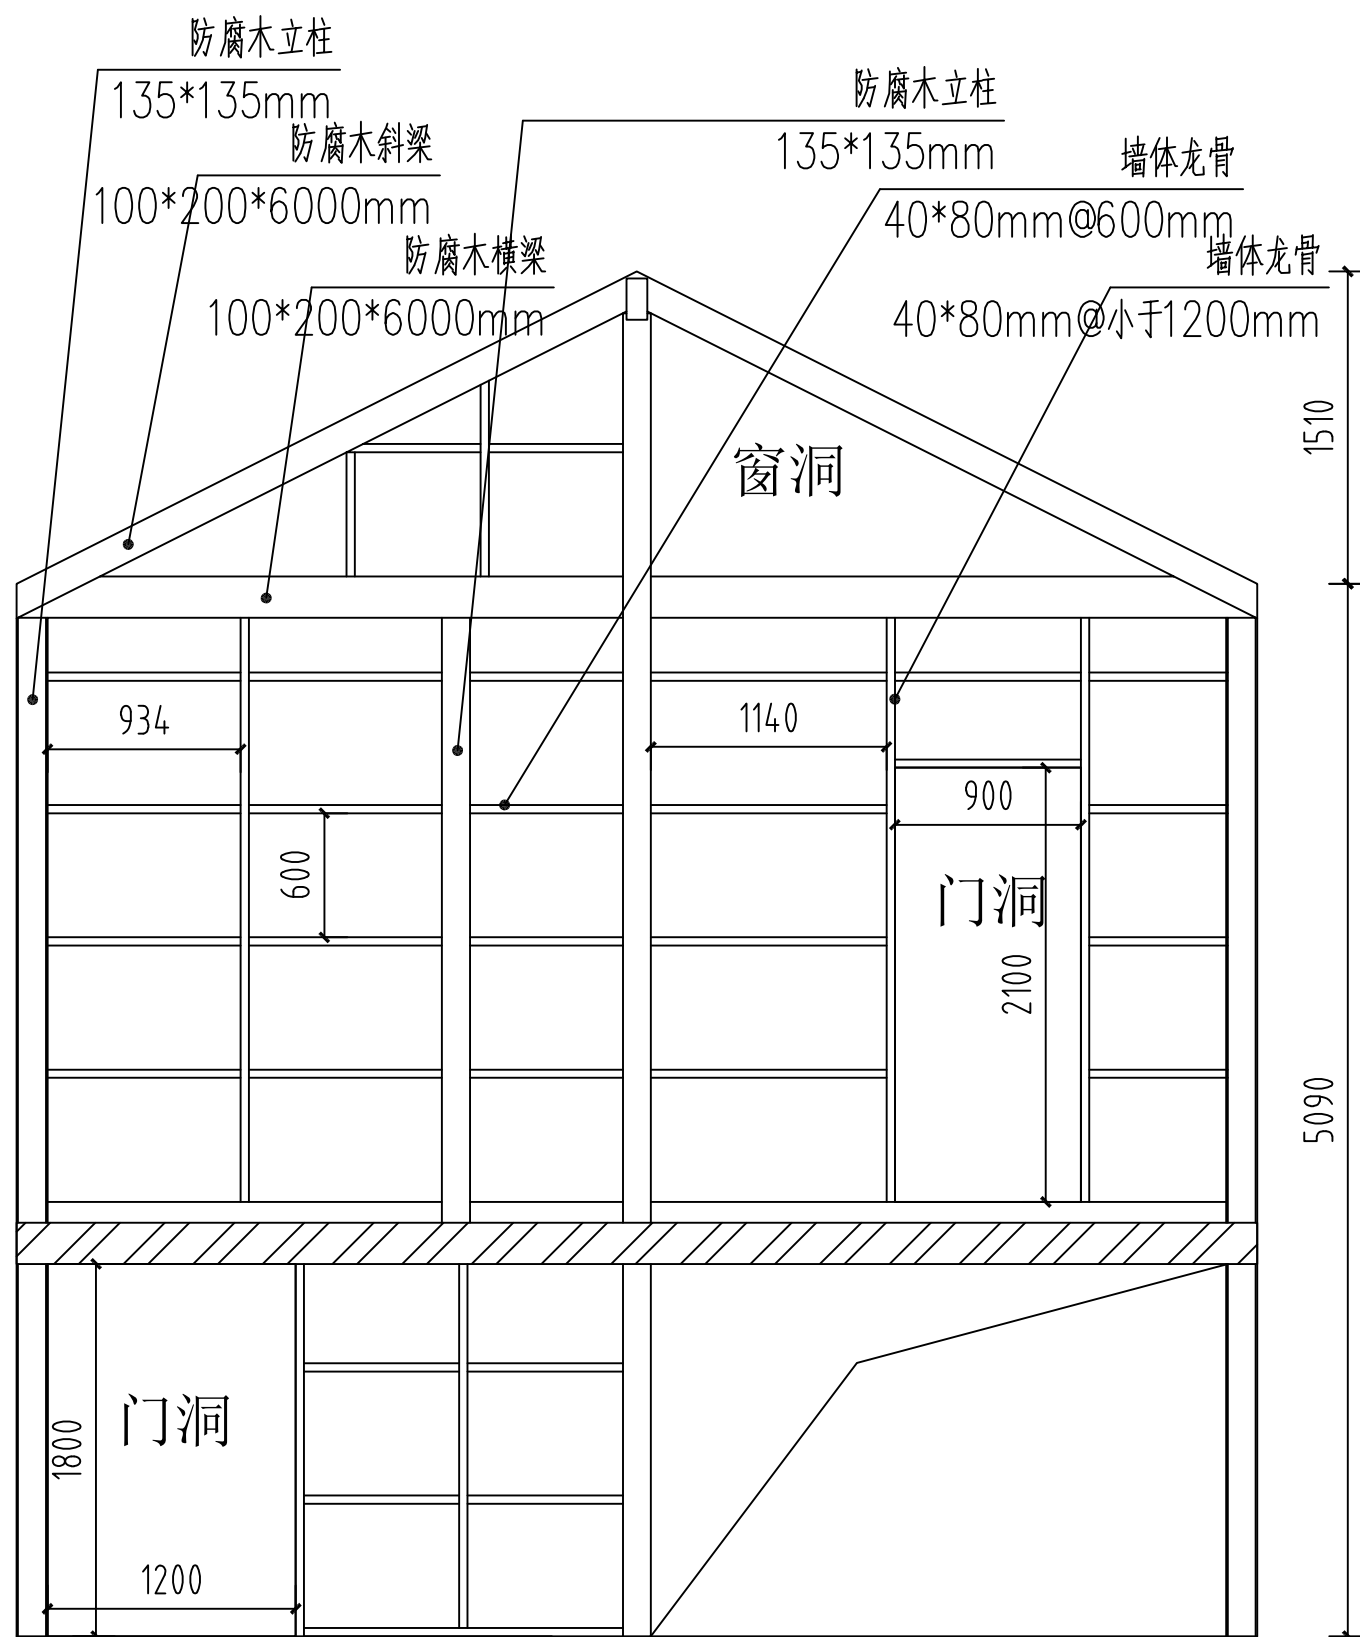


②墙体结构图 1: 30

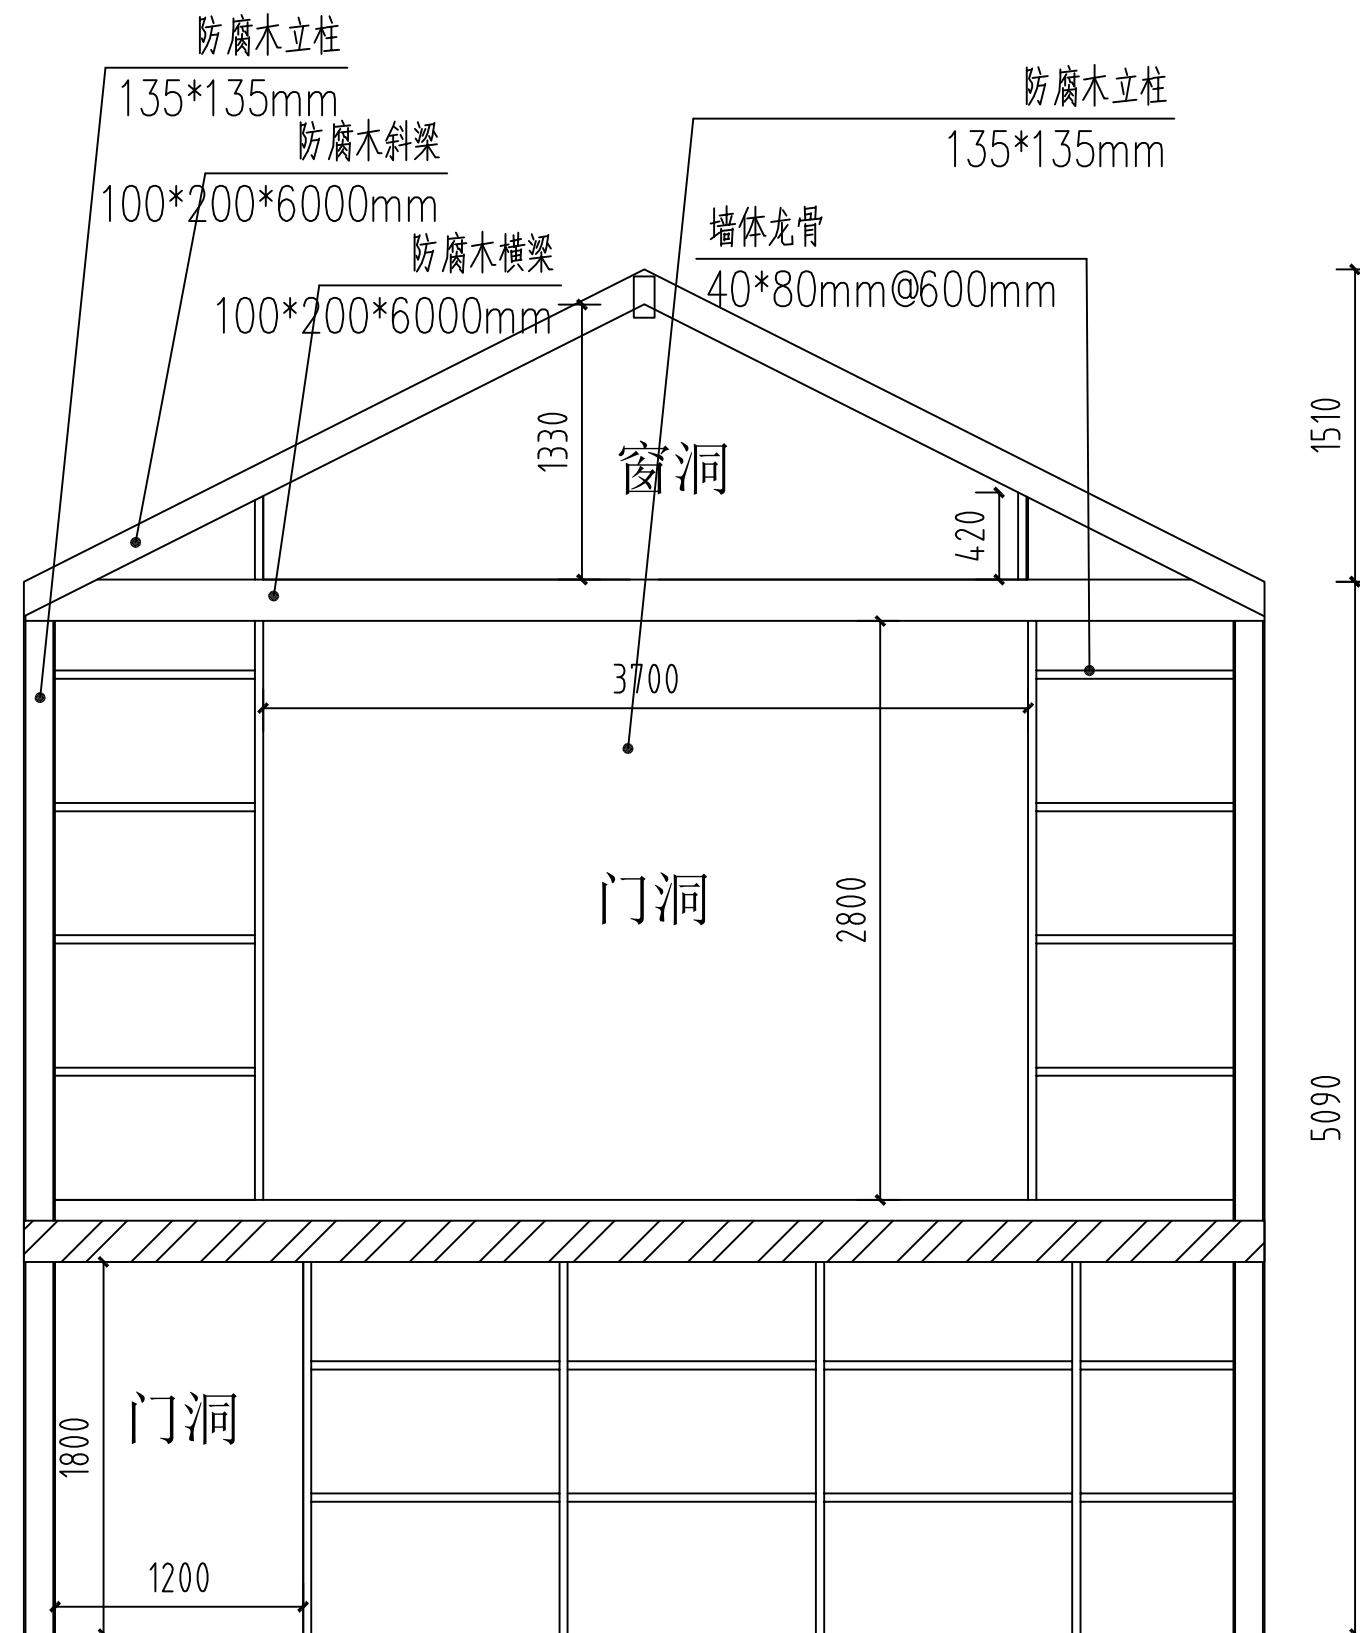


④墙体结构图 1: 30

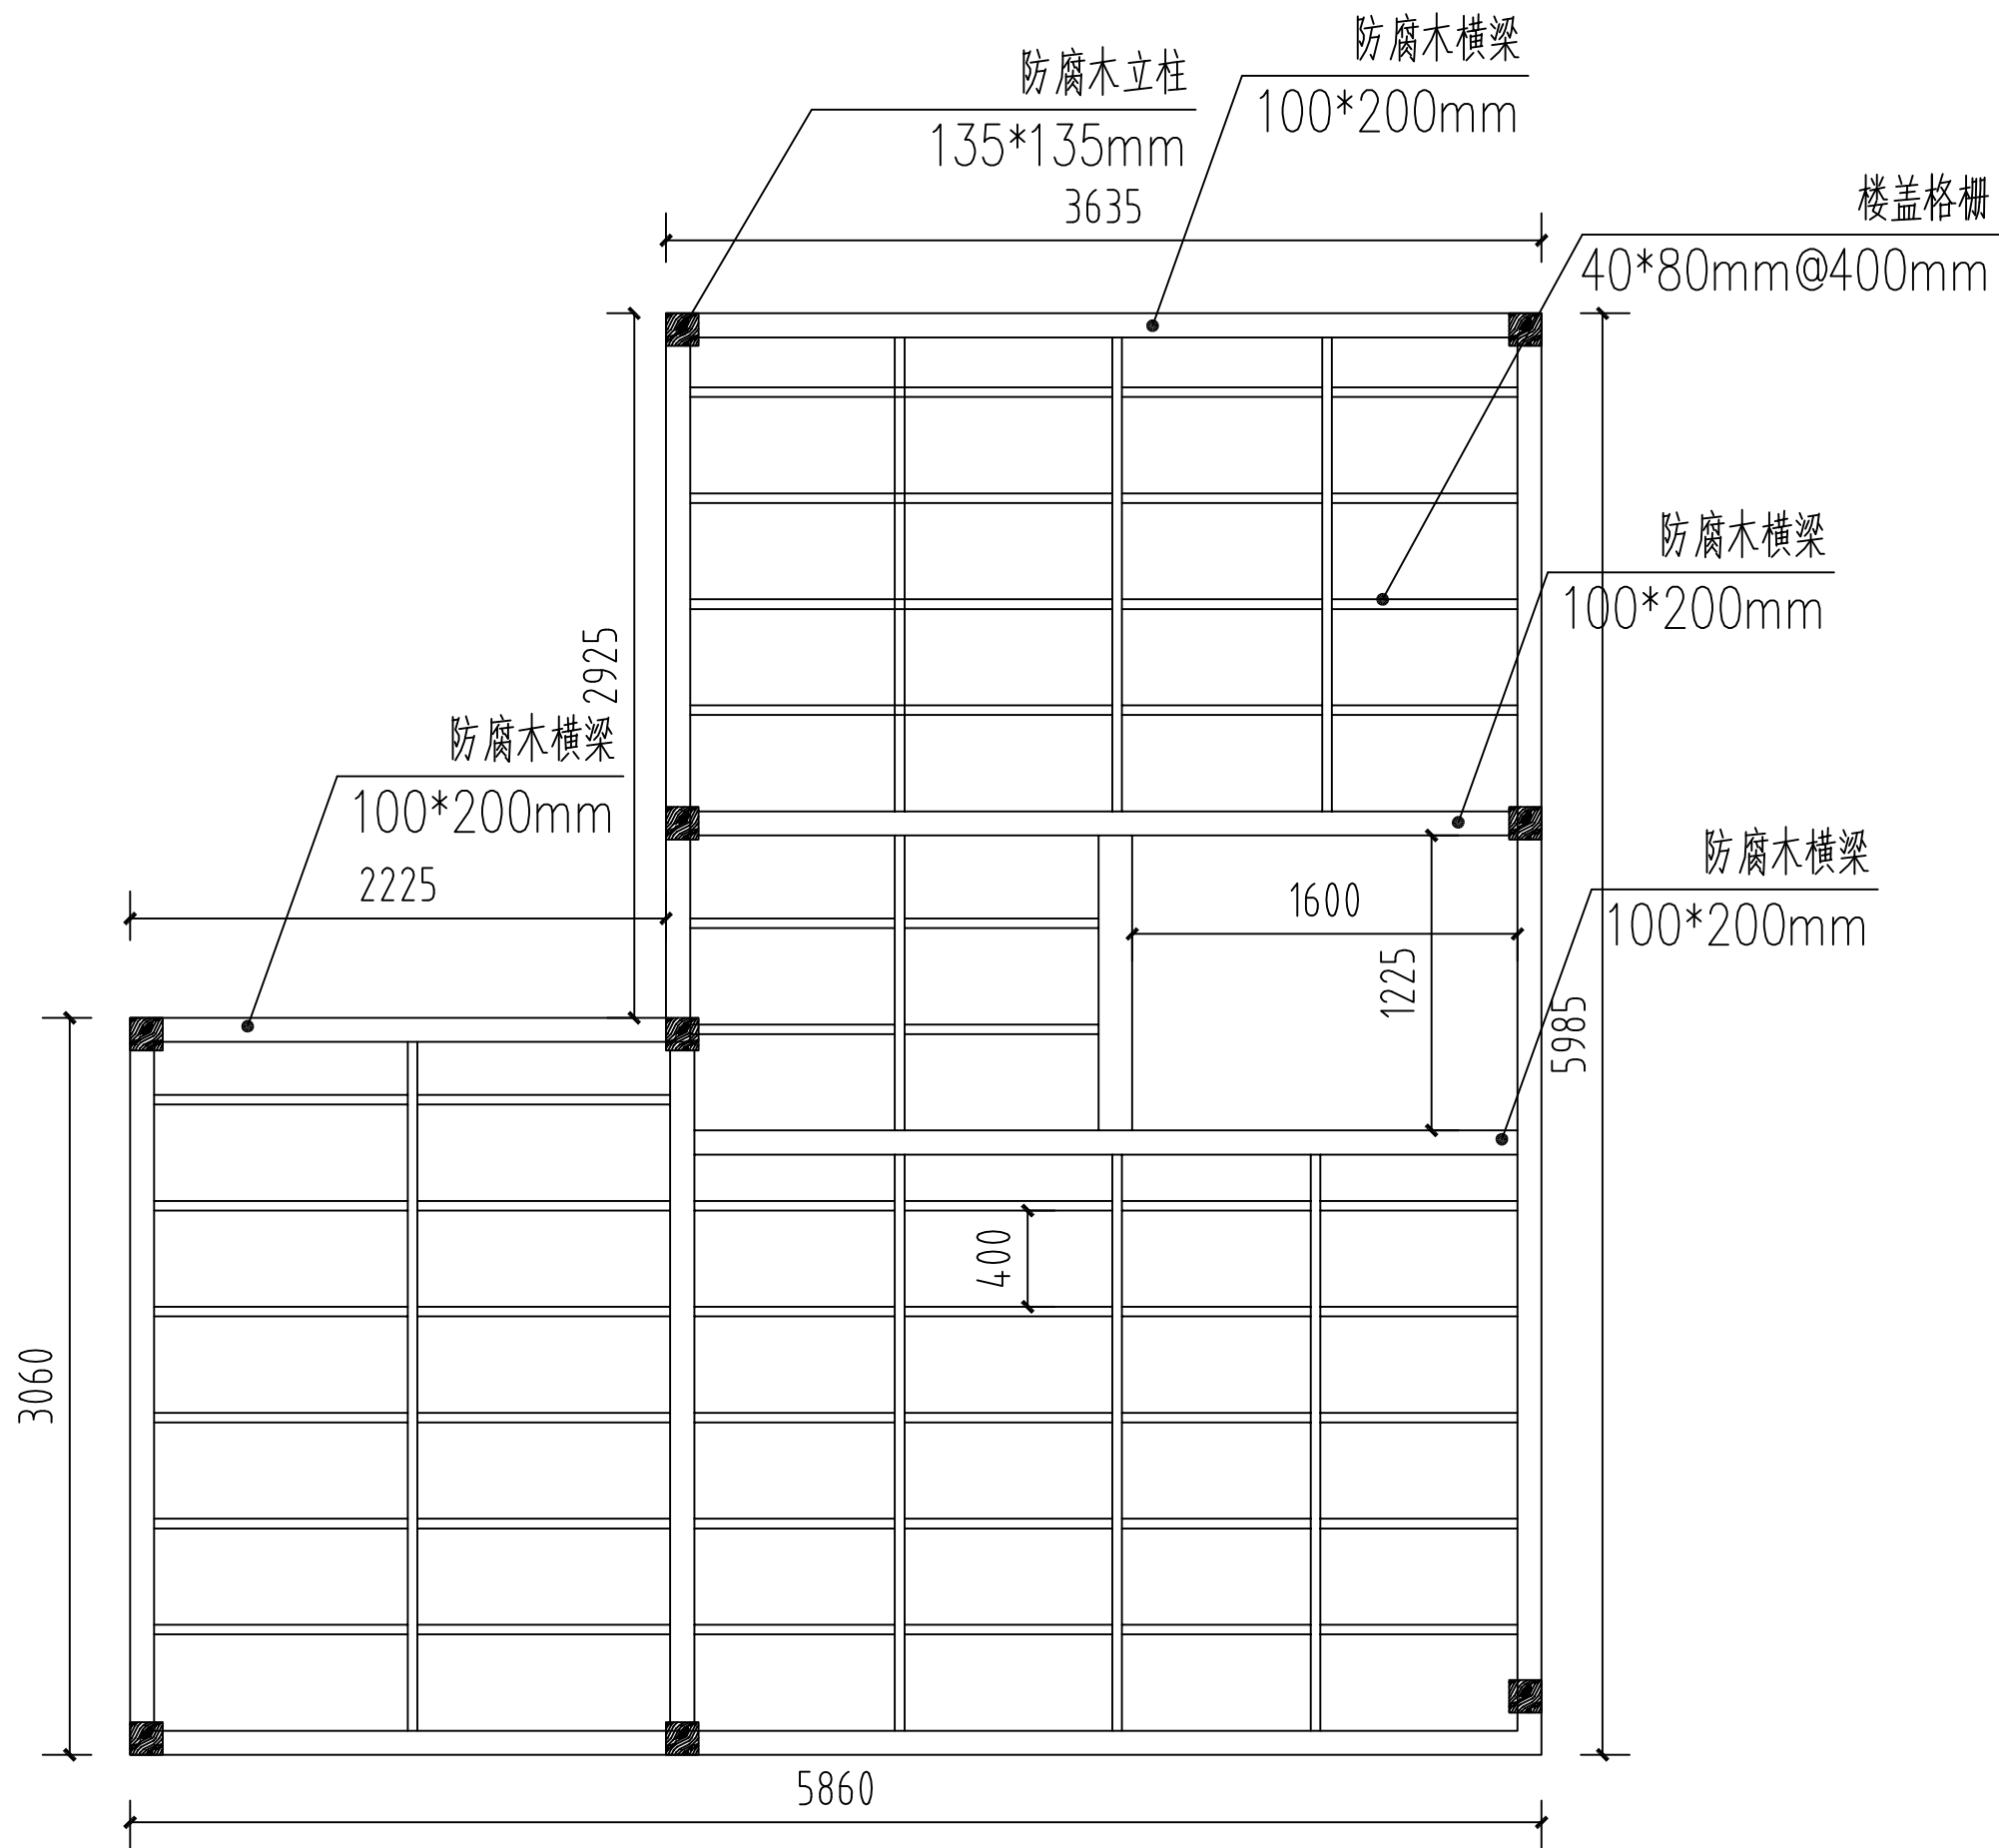


阁楼楼盖格栅龙骨平面图 1: 30

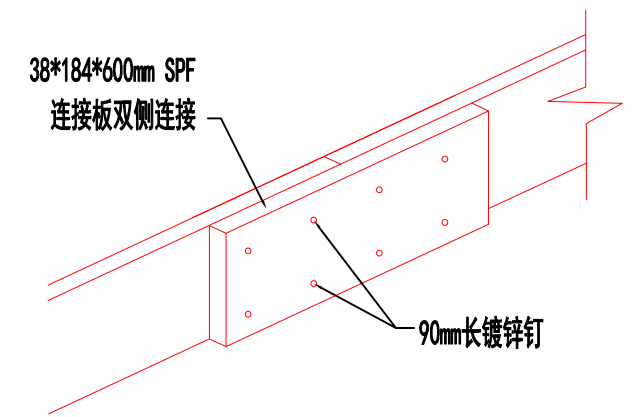

格栅接长连接详图


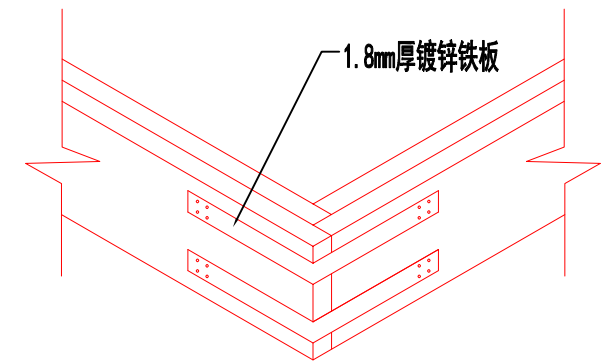


格栅拐角连接详图

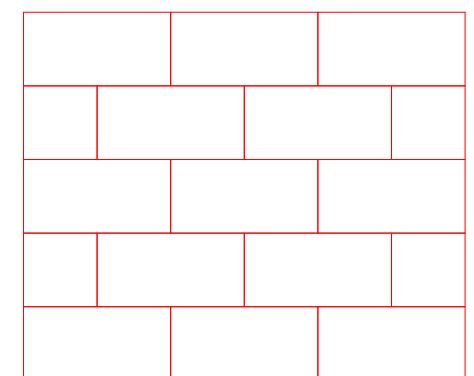

楼面OSB地板排布示意图


1. 所有楼面OSB地板厚度为18.3mm。
2. 地板固定用钉为镀锌钉，施钉间距为：沿板边150mm，板中300mm。
3. 地板固定之前，在格栅上涂结构用胶固定。

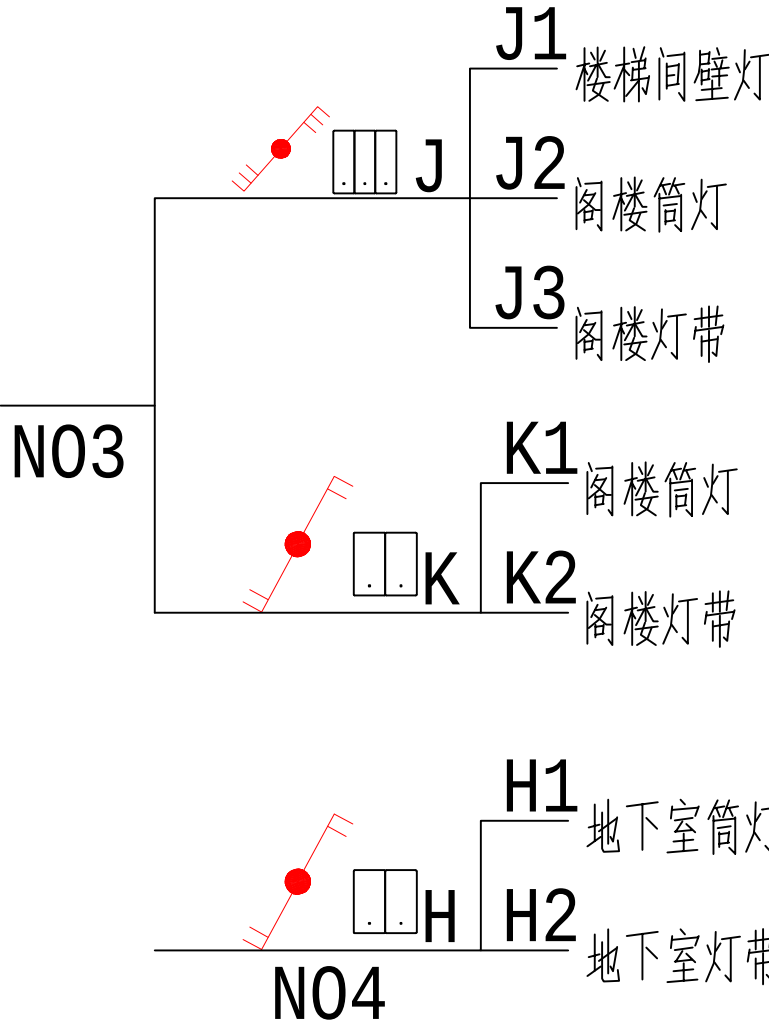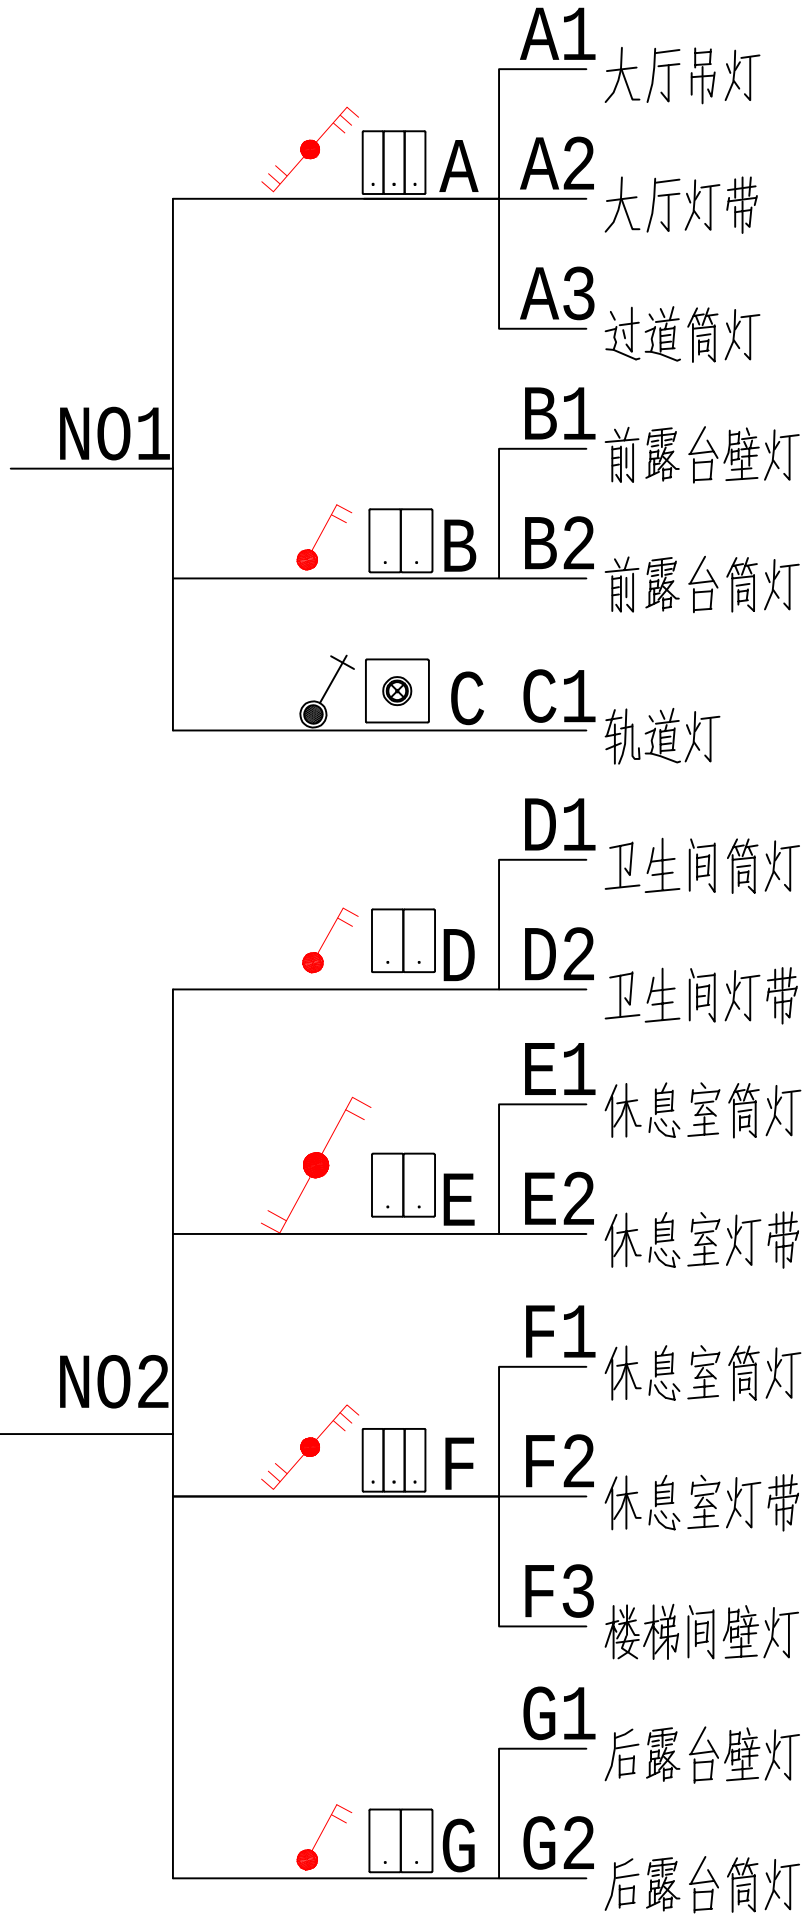


灯具图例	
吊灯	
轨道射灯	
轨道灯带	
筒灯	
壁灯	
暗藏LED灯管	
配电箱	

开关图例	
三联双控开关	
双联单控开关	
单联双控智能调光开关	
双联双控开关	


开关控制关系图

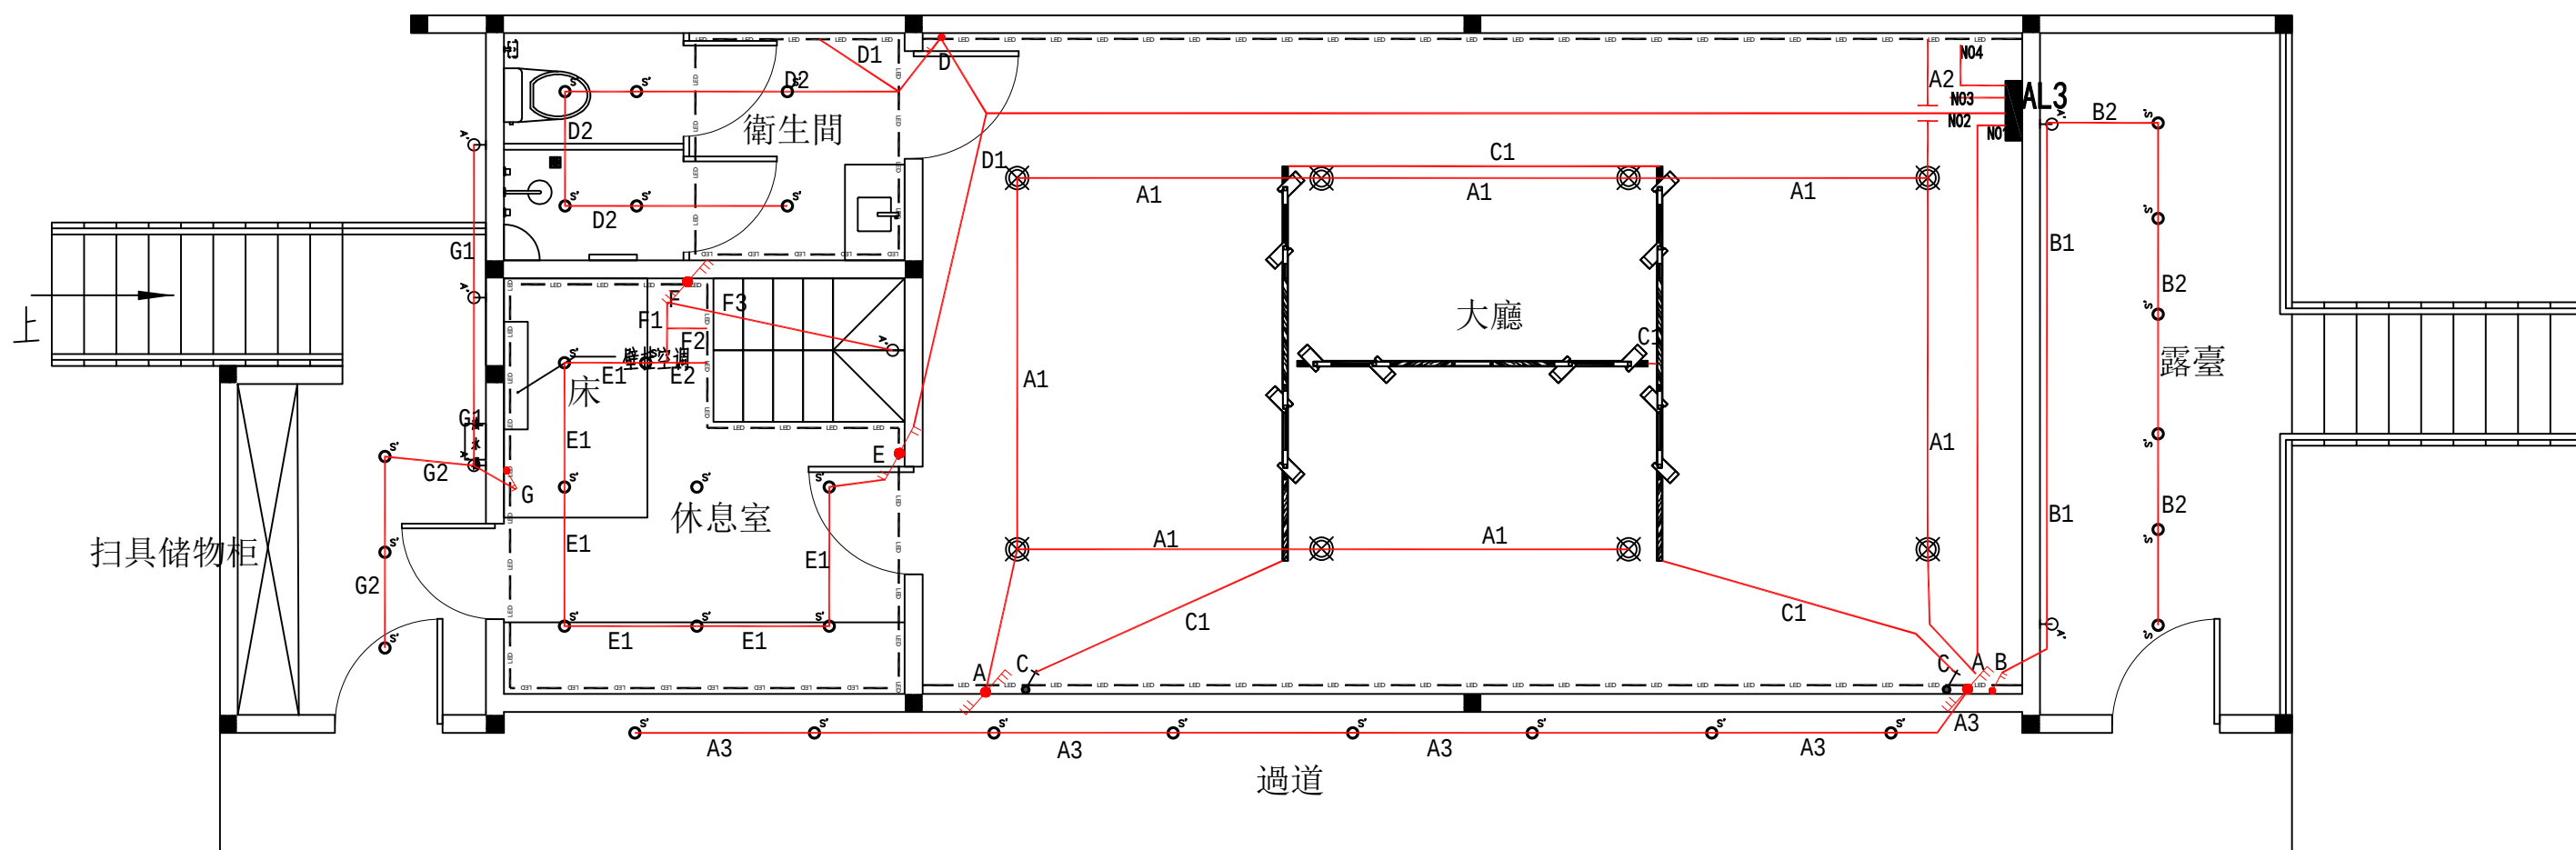


一楼照明平面图 1: 55

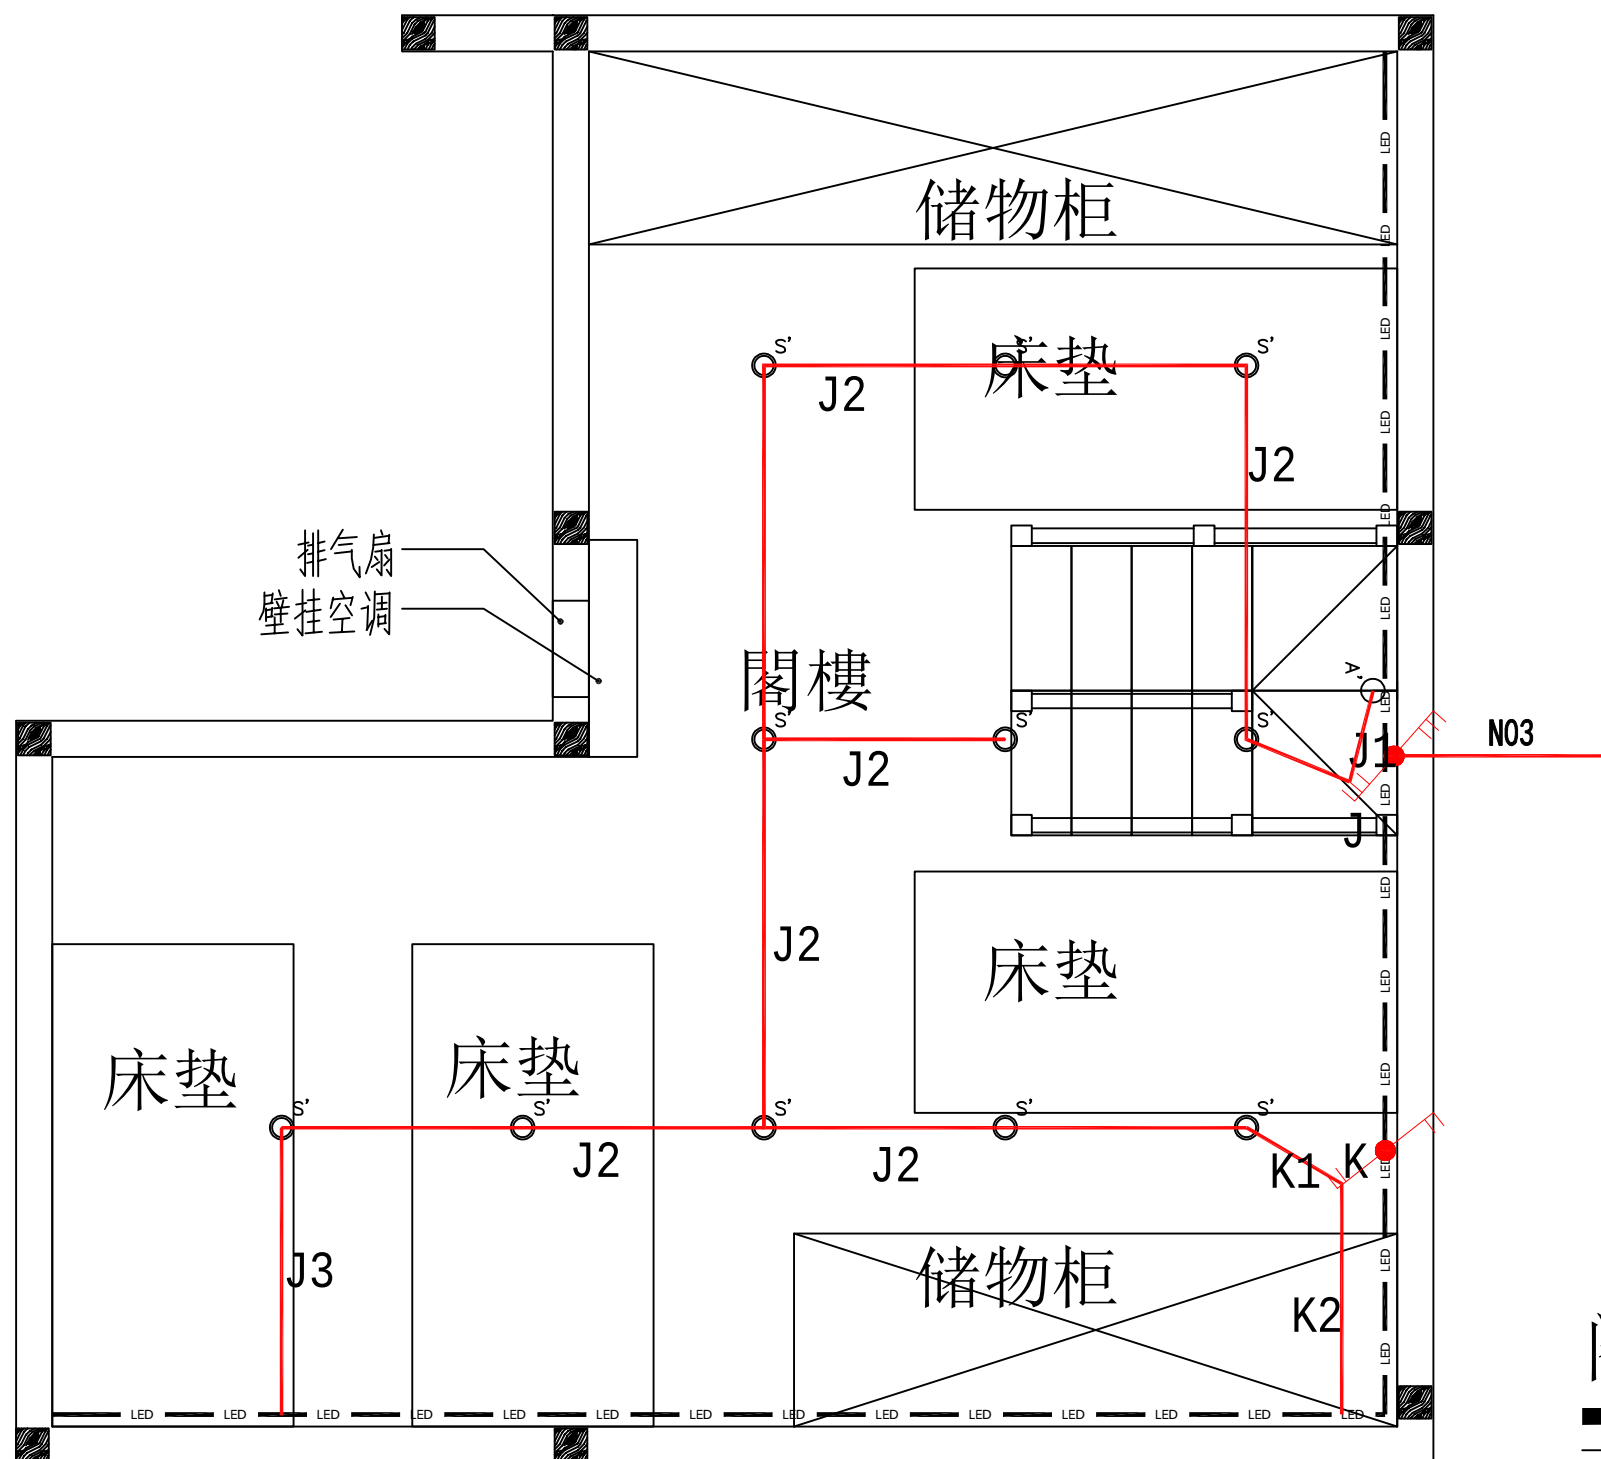


阁楼照明平面图 1: 30

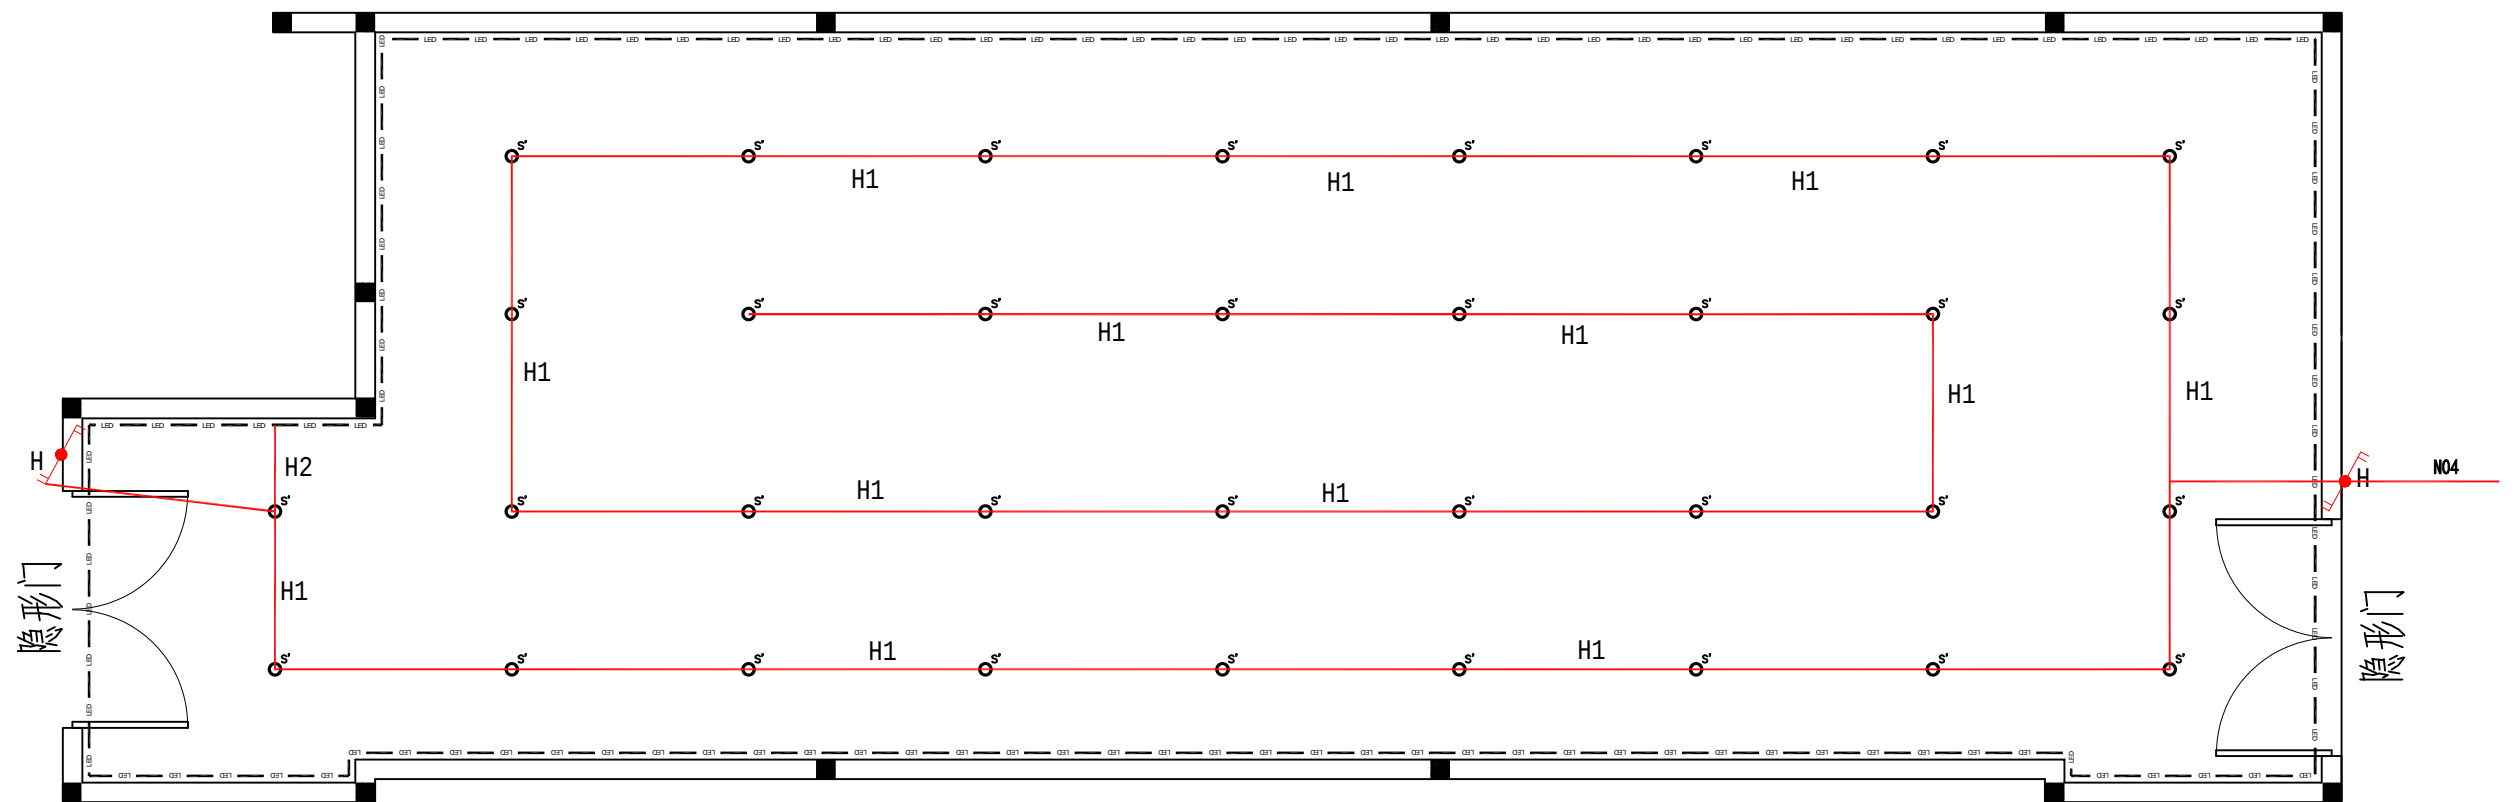

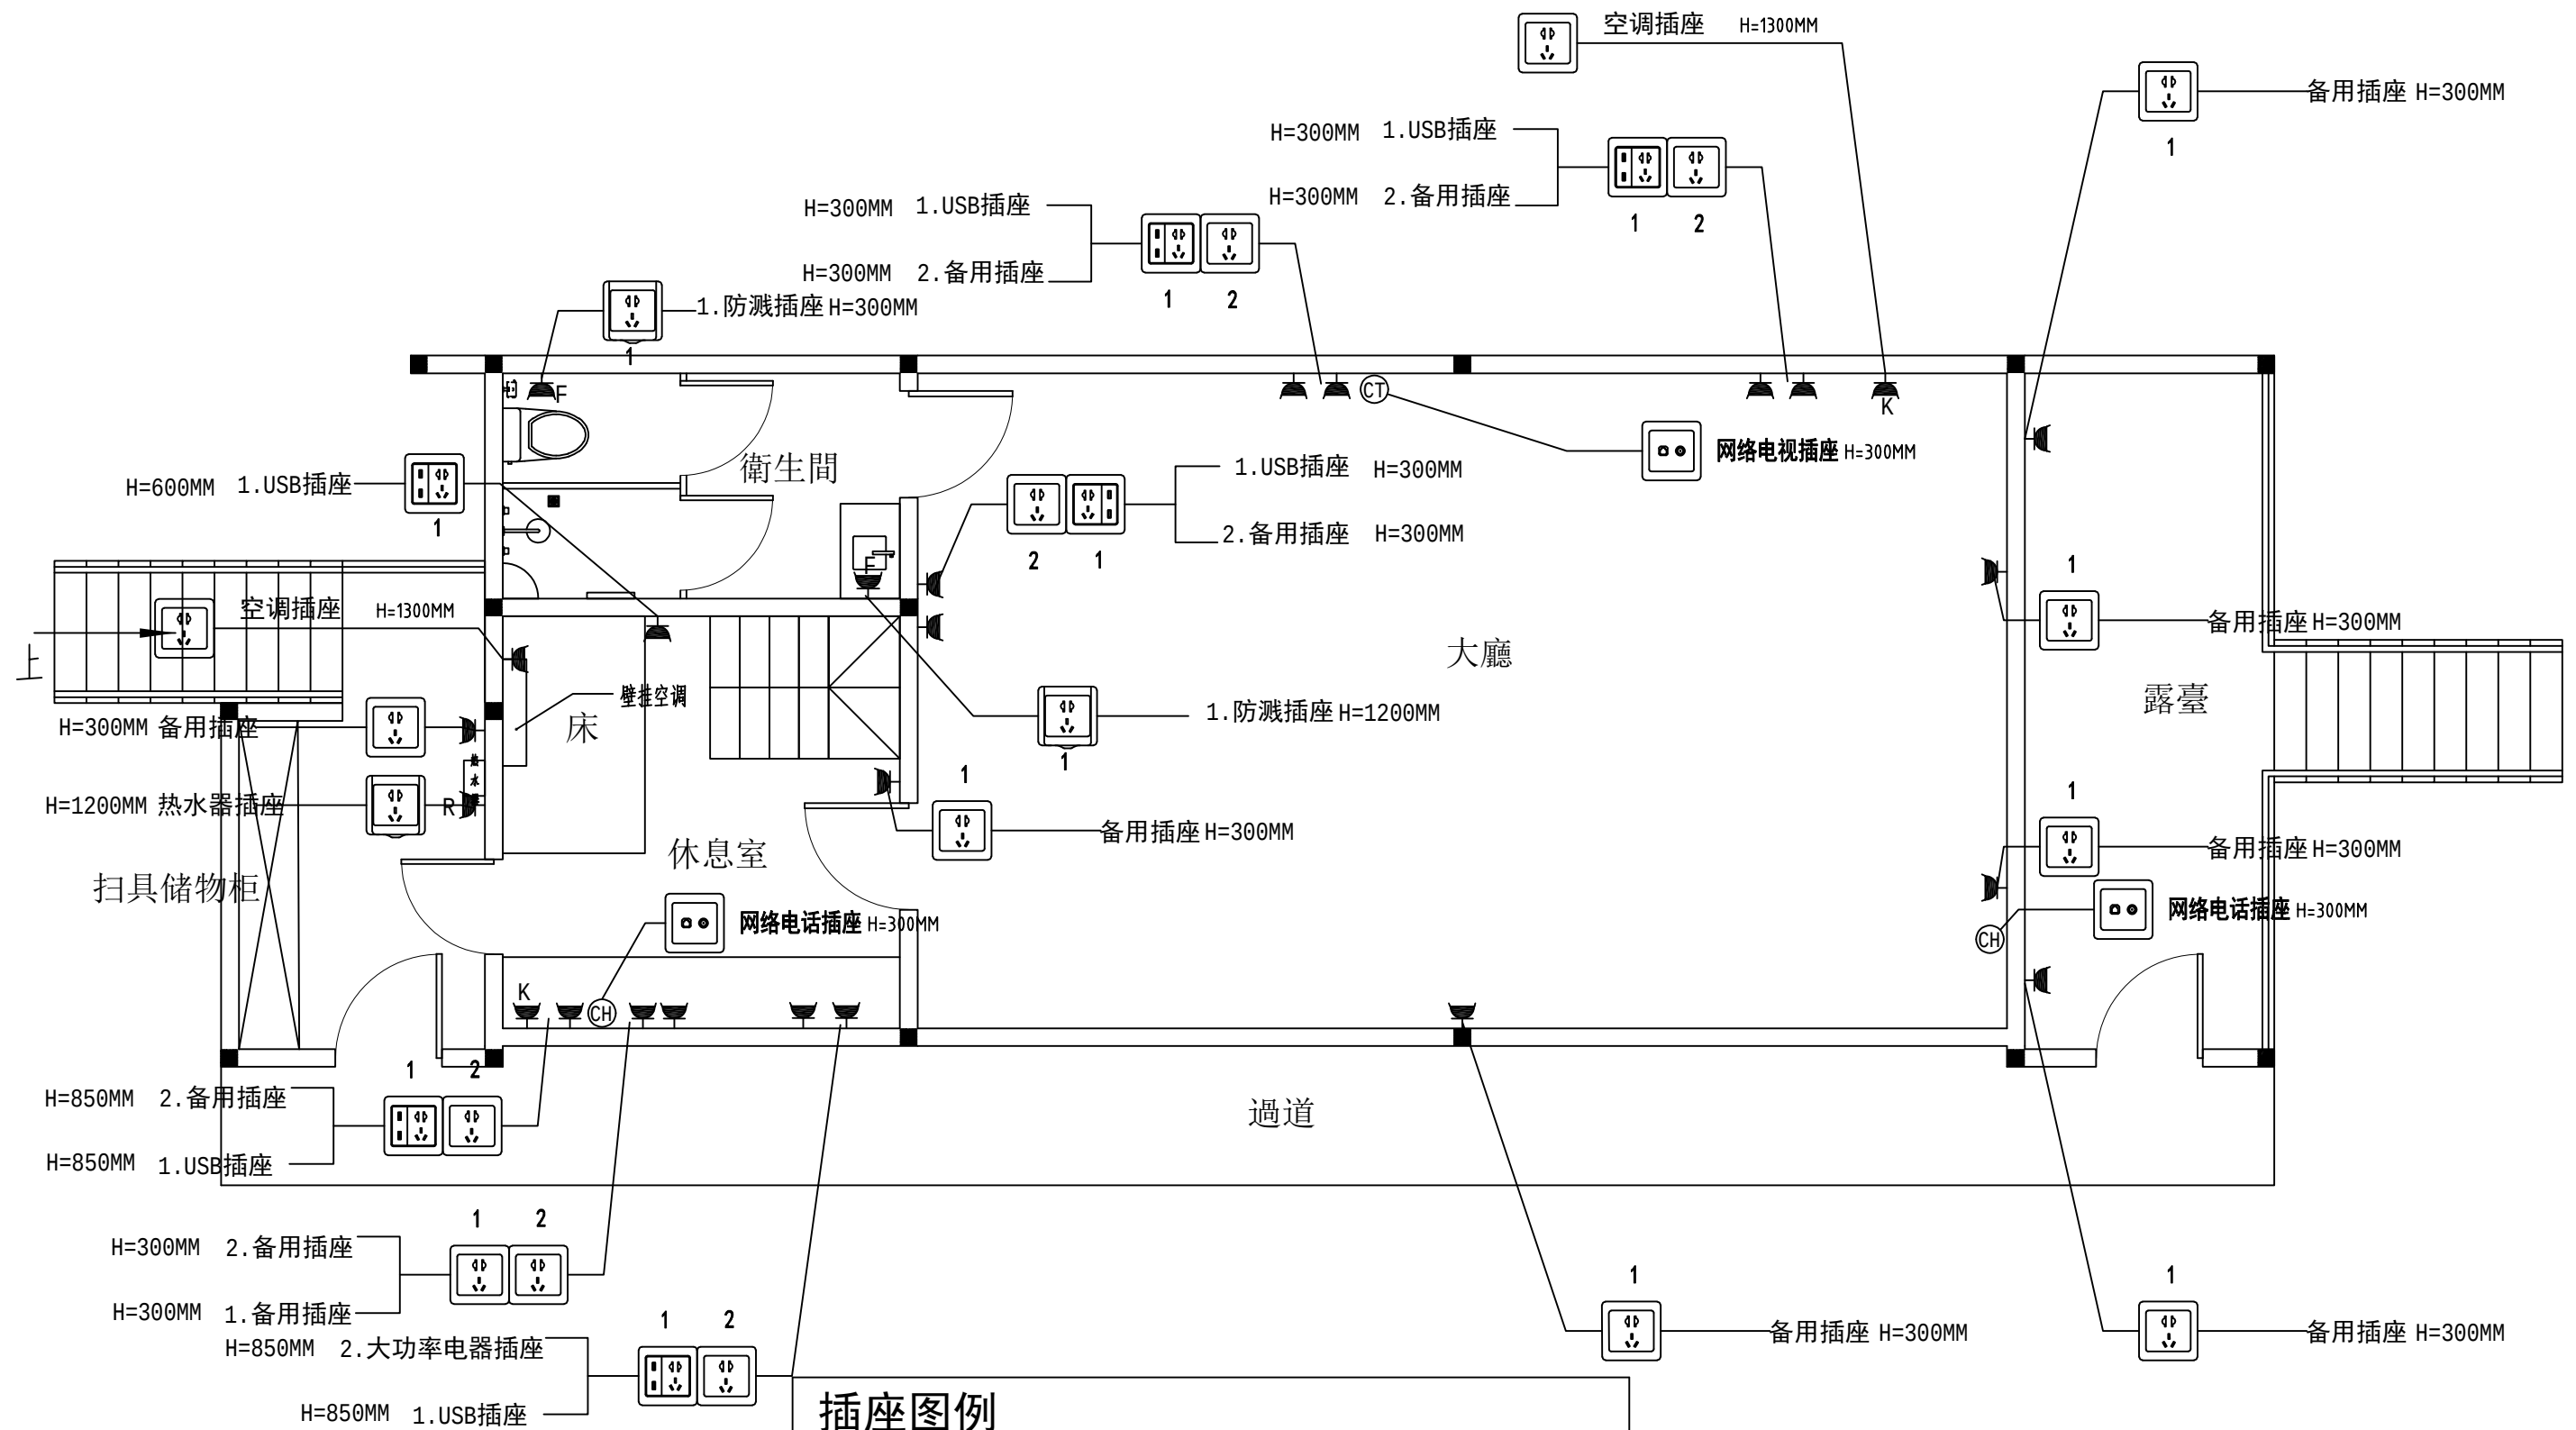

插座图例	
单相二、三极暗插座, 220/10A (安全型)	
防溅插座, 220/16A (防溅型)	
空调插座, 220/10A (安全型)	
热水器插座, 220/16A (防溅型)	
网络电话插座	
网络电视插座	


一楼插座平面图 1: 55

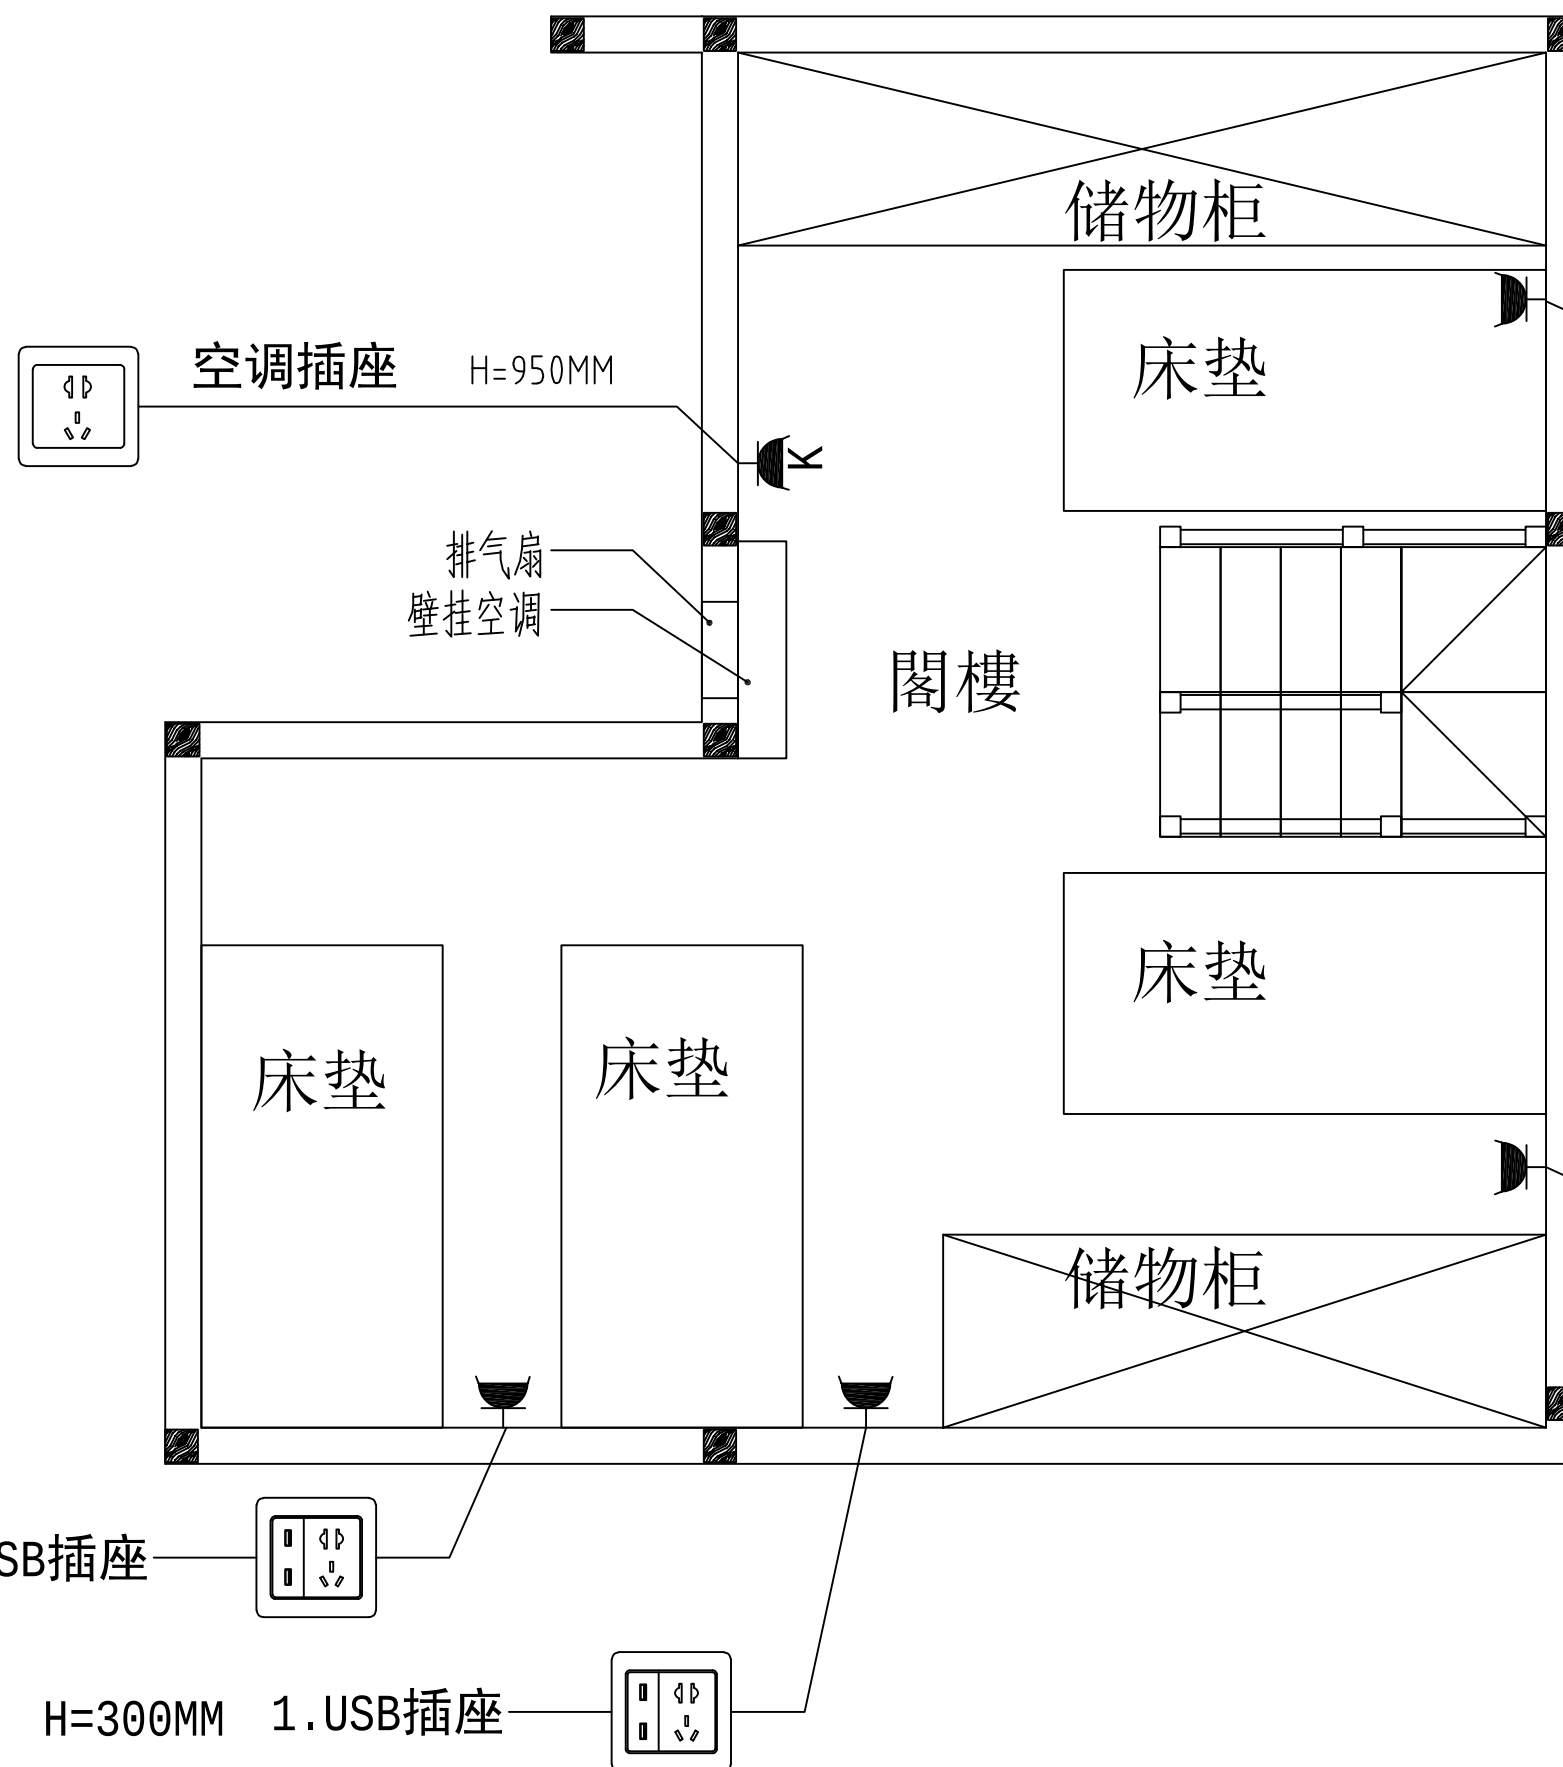

插座图例	
单相二、三极暗插座, 220/10A (安全型)	
防溅插座, 220/16A (防溅型)	
空调插座, 220/10A (安全型)	
网络电话插座	
网络电视插座	

阁楼插座平面图 1: 30


插座图例	
单相二、三极暗插座, 220/10A (安全型)	
防溅插座, 220/16A (防溅型)	
空调插座, 220/10A (安全型)	
网络电话插座	
网络电视插座	

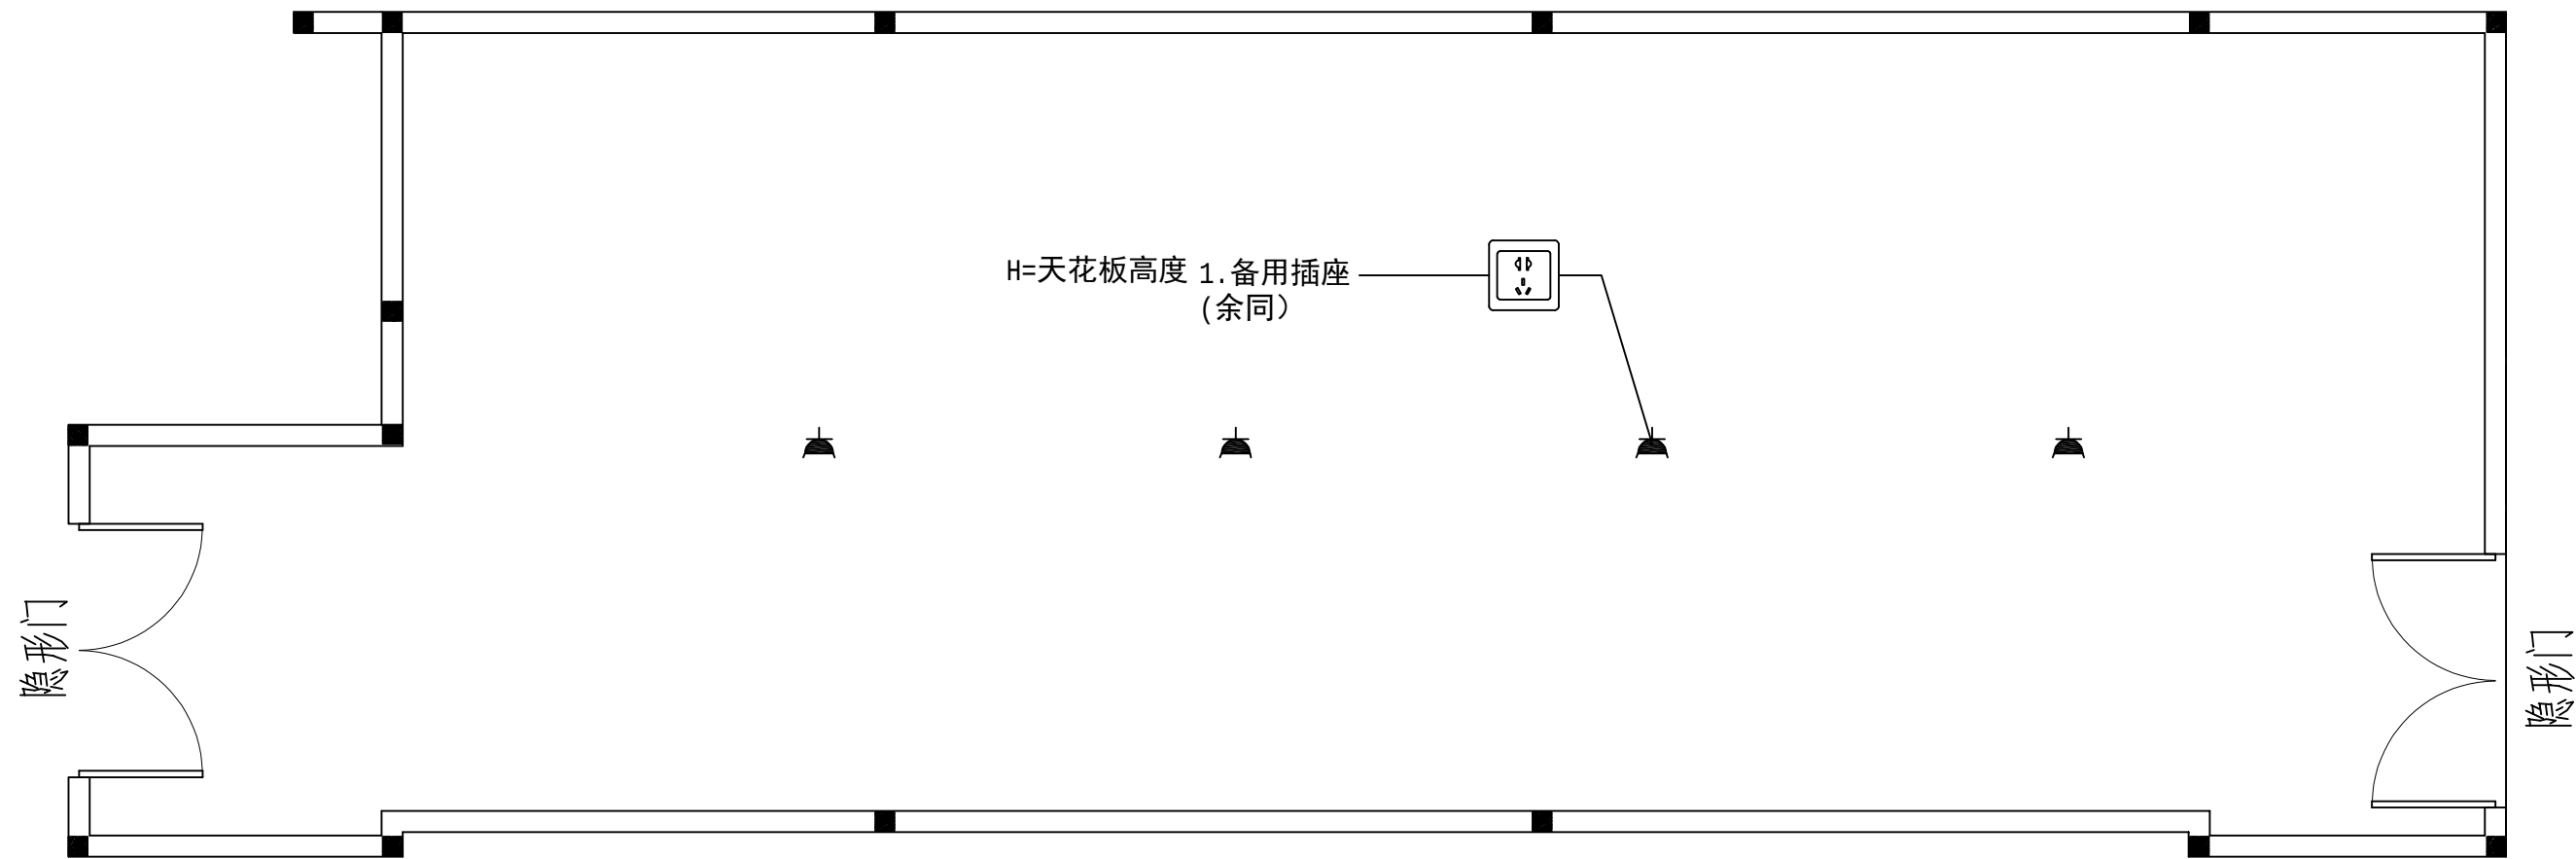


负一楼插座平面图 1: 50

图 例


	给水冷水管DN15		冷水供水点
	给水热水管DN20		热水供水点
	排水管DN75		
	地漏		

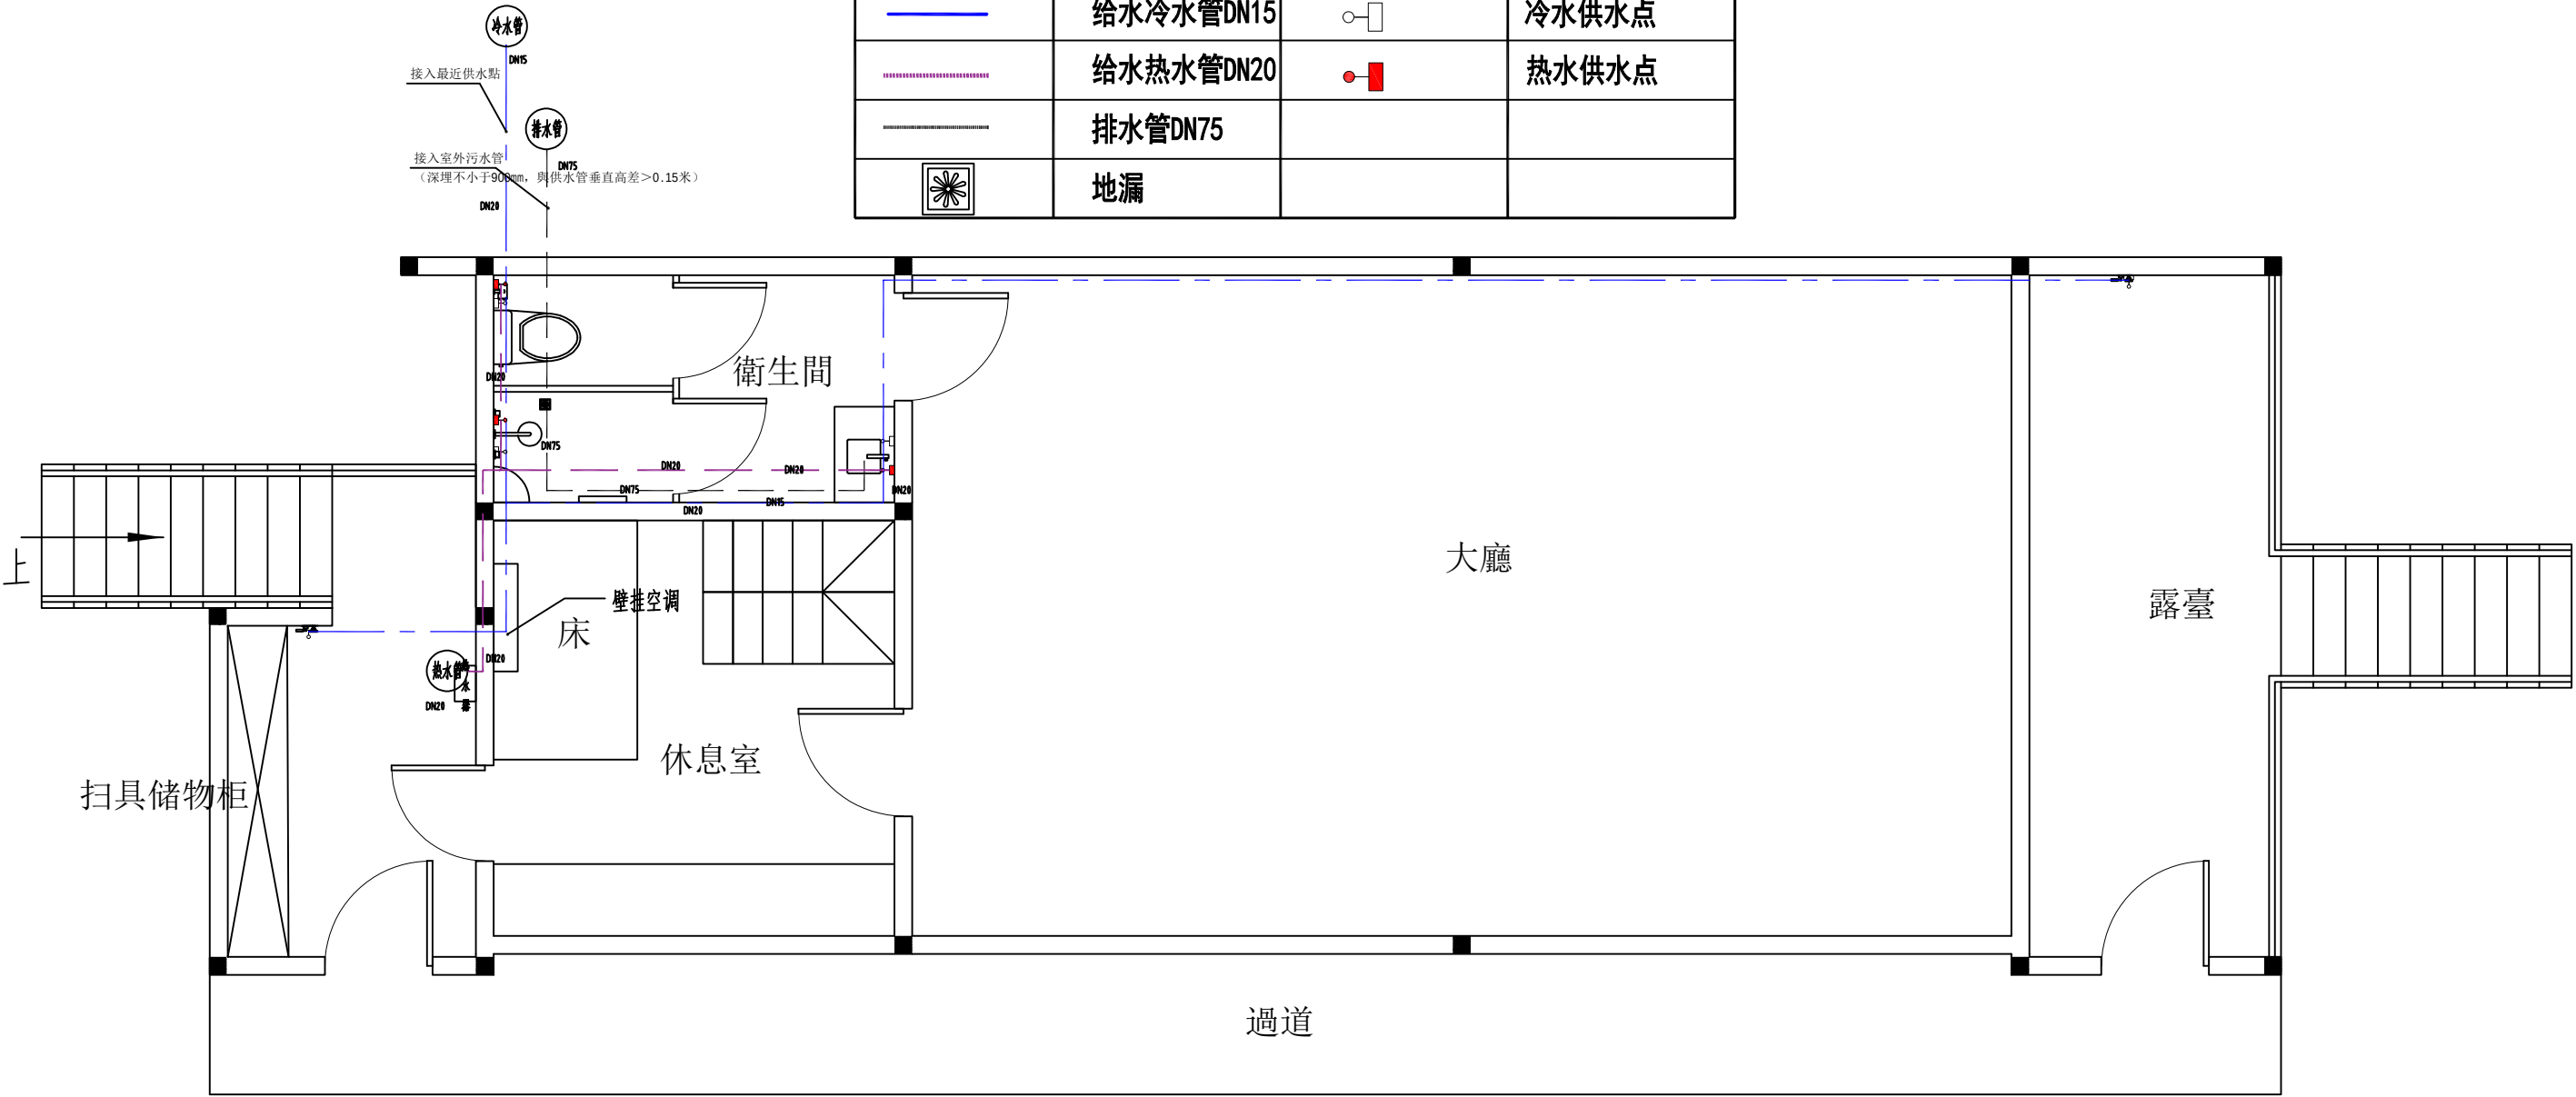


一楼给排水平面图 1: 50

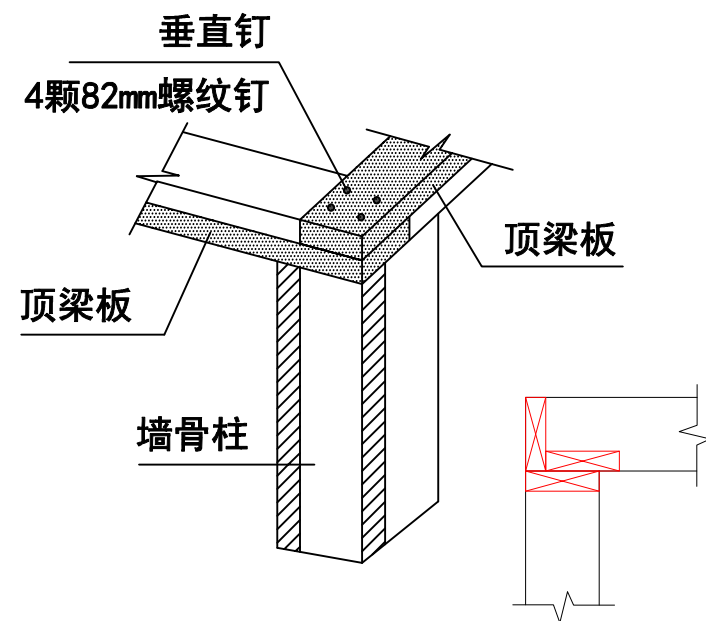


墙体转角连接详图

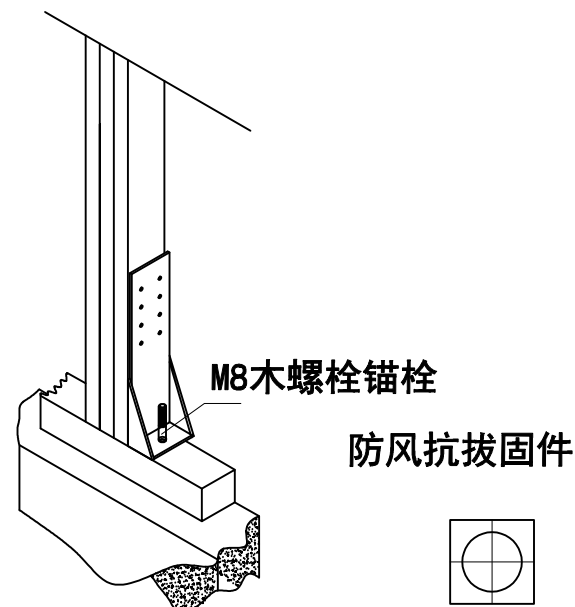

金属防风抗拔连接件大样

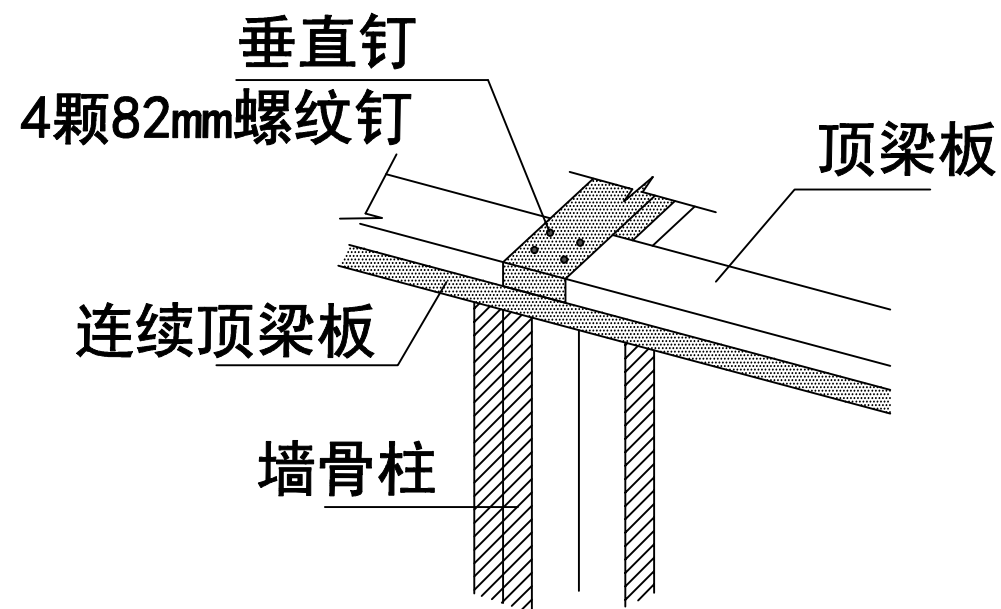

内、外墙体连接详图

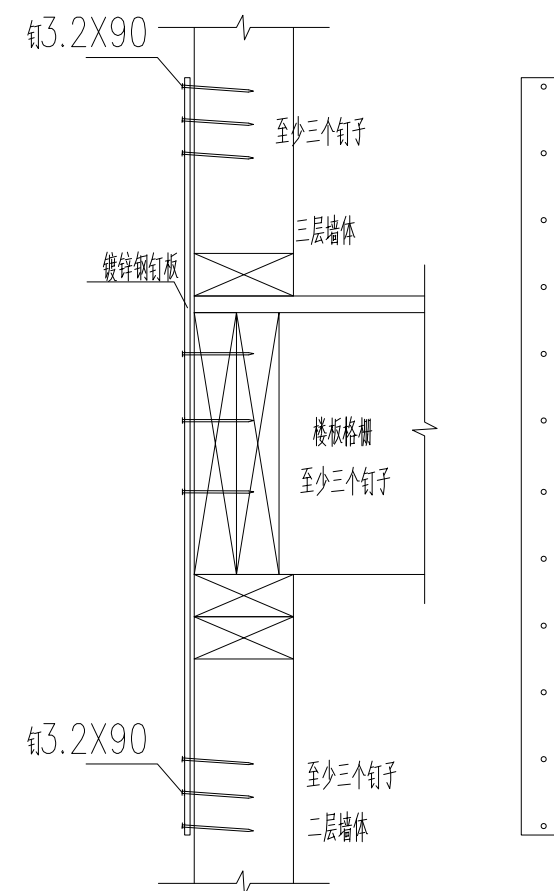


镀锌钢钉板=38X684X1.0
镀锌钢钉板间距小于或等于2000
镀锌钢钉板安装与基础和一层墙体处镀锌钢钉板相对应。



墙体楼板格栅连接详图

注意事项：


1. 沿所有一层墙体底部设置防腐木一道，界面分别为200*90mm、200*140mm，膨胀螺栓固定。
2. 墙体骨柱为40*80mm木材，均为结构二级材，中心间距600mm。
3. 所有外墙均铺设一层11.1mm厚OSB板，内墙卫生间墙体铺设11.1mmOSB板。

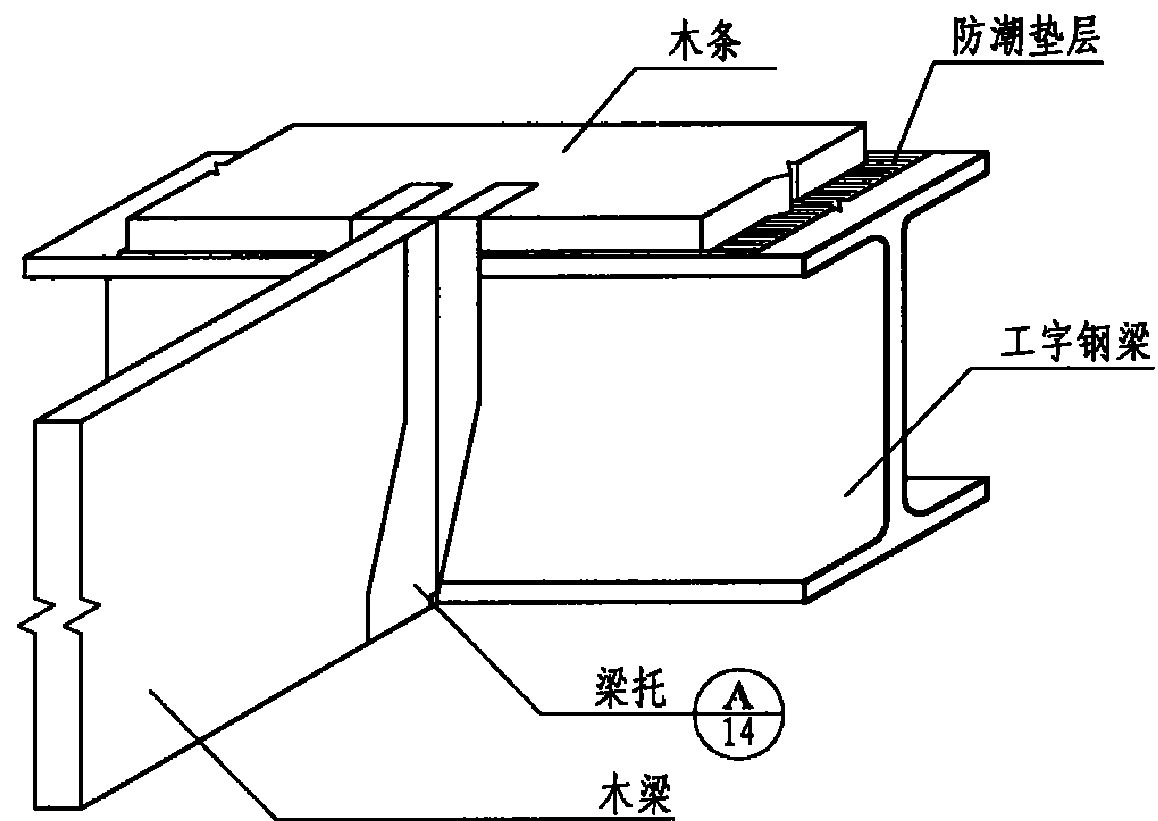

钢梁与木梁连接

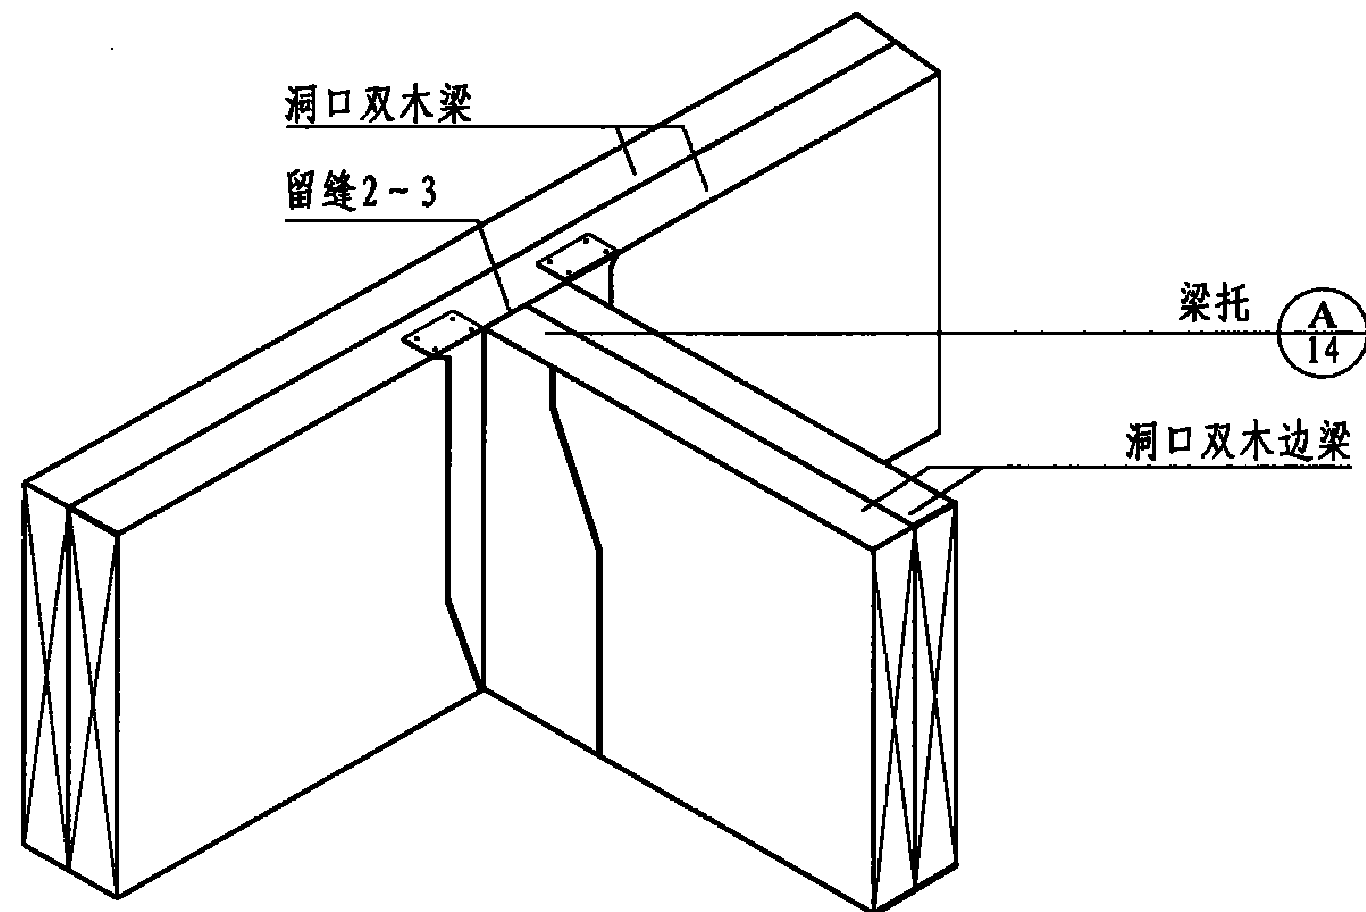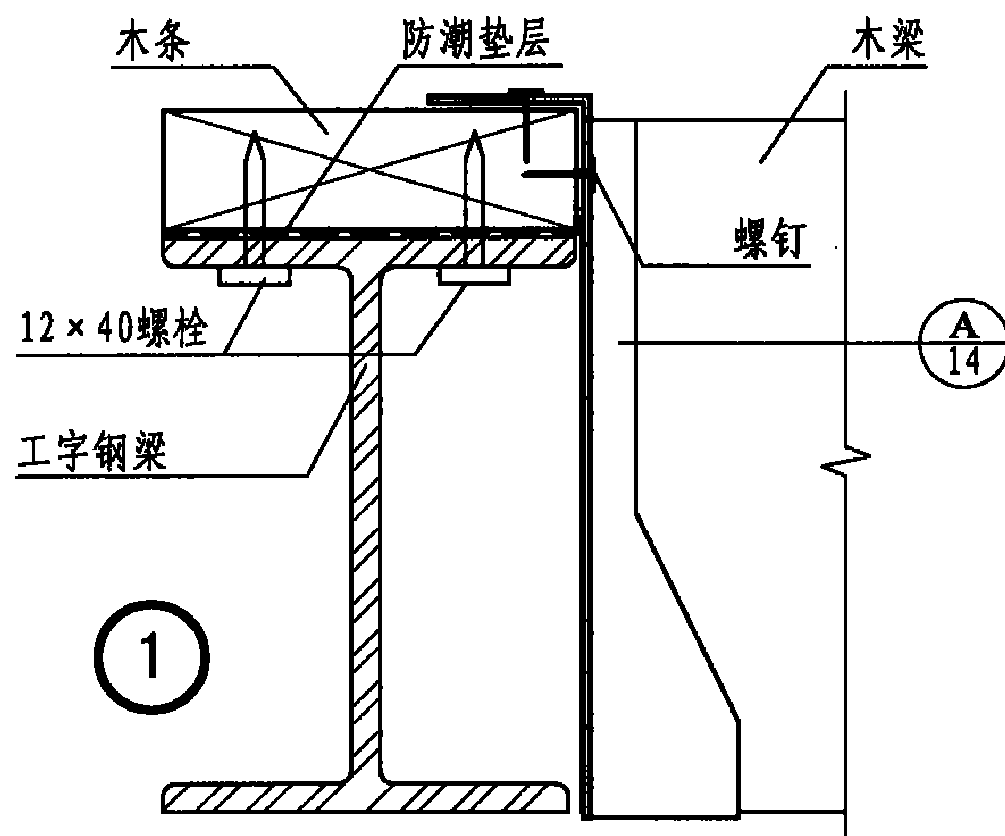

木梁与木梁连接

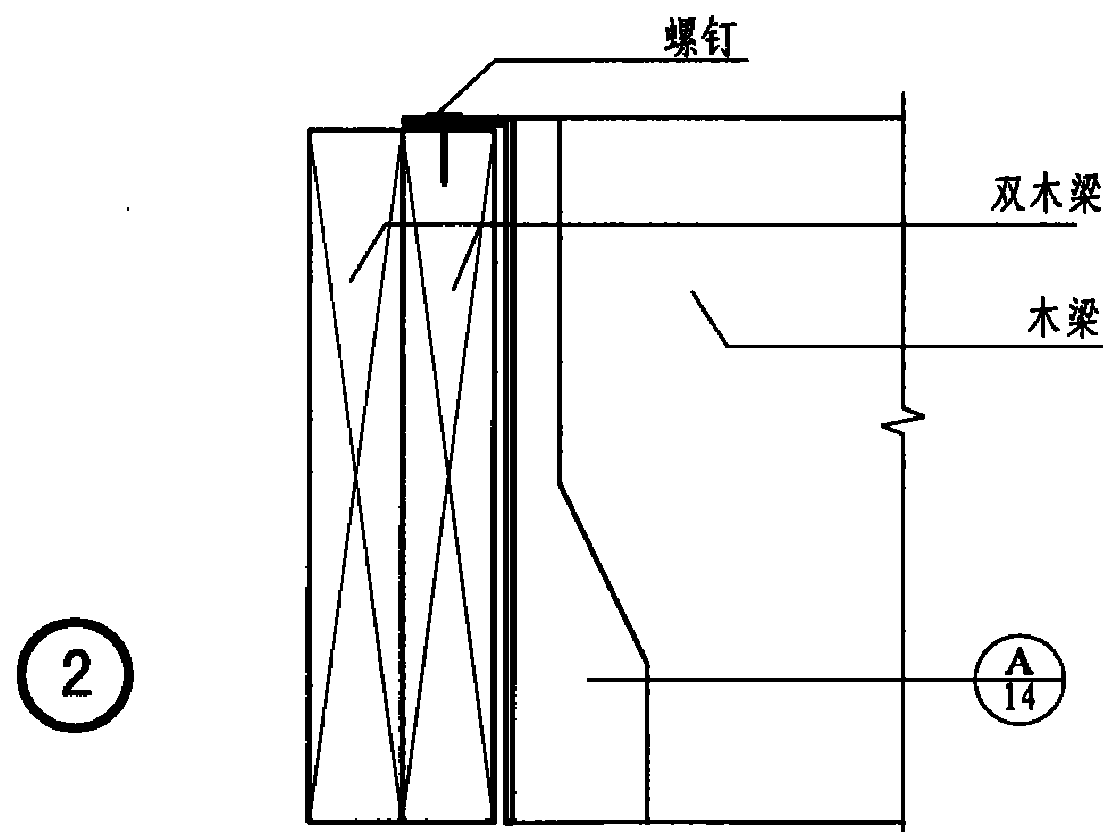

注：工字钢梁先钻孔，后用螺栓将钢梁于防腐木拧牢。